

APPELLATION SUN VALLEY AUDIO VIDEO INTEGRATION

AUDIOVISUAL SHOP DRAWINGS

MARSHALL INDUSTRIES • 1303 NORTH 39TH STREET, NAMPA, ID • 208.442.7222



www.marshallind.com

PROJECT INFORMATION

853

APPELLATION SUN VALLEY
AUDIO VIDEO INTEGRATION

CUSTOMER NAME:	CUSTOMER NUMBER:
HARRIMAN SUN VALLEY HOTEL	APH001
SITE NAME:	SITE NUMBER:
HARRIMAN SUN VALLEY HOTEL	72338311
SITE ADDRESS:	
300 E RIVER ST KETCHUM, ID 83353	

00 E RIVER ST
CHUM, ID 83353

SALES PERSON: JEREMY WADDELL	ENGINEERED BY: ADAM HANDY
DRAFTER: ELI ANDERSON	PROJECT MANAGER: JEREMY WADDELL

DRAWING SET INFORMATION

PHASE: _____

SUBMITTAL _____

PUBLISH DATE: _____

11/20/2025 _____

PLOT SIZE: _____

ARCH FULL BLEED E (36.00 X 48.00 INCHES) _____

PLOT SCALE: _____

1" = 1'-0" _____

APPROVED BY: _____

SHEET REVISION INFORMATION

C	REVISION DATE:	11/20/2025
	REVISION DESCRIPTION:	RESUBMITTAL

REVISION & ISSUE HISTORY

[illegible]

APPELLATION SUN VALLEY

GENERAL DRAWINGS

TABLE OF CONTENTS

AV000


FILE NAME: AV000.DWG

ENCLOSURE LEGEND		
------------------	--	--

SYM	TYPE	GANG	DESCRIPTION	ELEVATION	QTY
PROJECT SPECIFIC WALL BOXES					
A		1	3" DEEP BACKBOX	FIELD DETERMINED	5
B		1	3" DEEP BACKBOX	+11' AFF	4
D		1	SPEAKER LOCATION	FIELD DETERMINED	6
E		1	LANDSCAPE SPEAKER	FIELD DETERMINED	9
F		1	LANDSCAPE SUBWOOFER	FIELD DETERMINED	1
G	CHIEF PAC526FWP2		DISPLAY LOCATION	60" AFF	3
H					
I					
J					
K					
L					
M					
N					
O					
P					
Q					
T					
U					
V					
W					
X					


TABLE BOXES					
A					
B					
C					
D					
E					
F					
G					
H					
I					
J					
K					
L					

EQUIPMENT RACKS					
A	MIDDLE ATLANTIC CWR-26-26VD	0	26RU EQUIPMNET RACK		3
B					
C					
D					
E					
F					
G					
H					
I					
J					
K					
L					

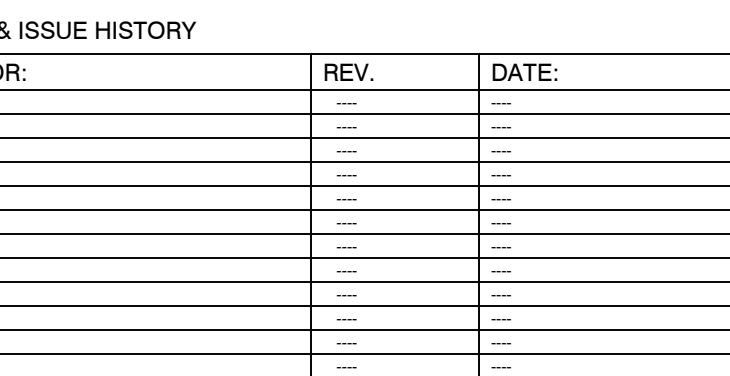


AV001


AV100/AV200 WIRE PATH AND ENCLOSURE EXAMPLE

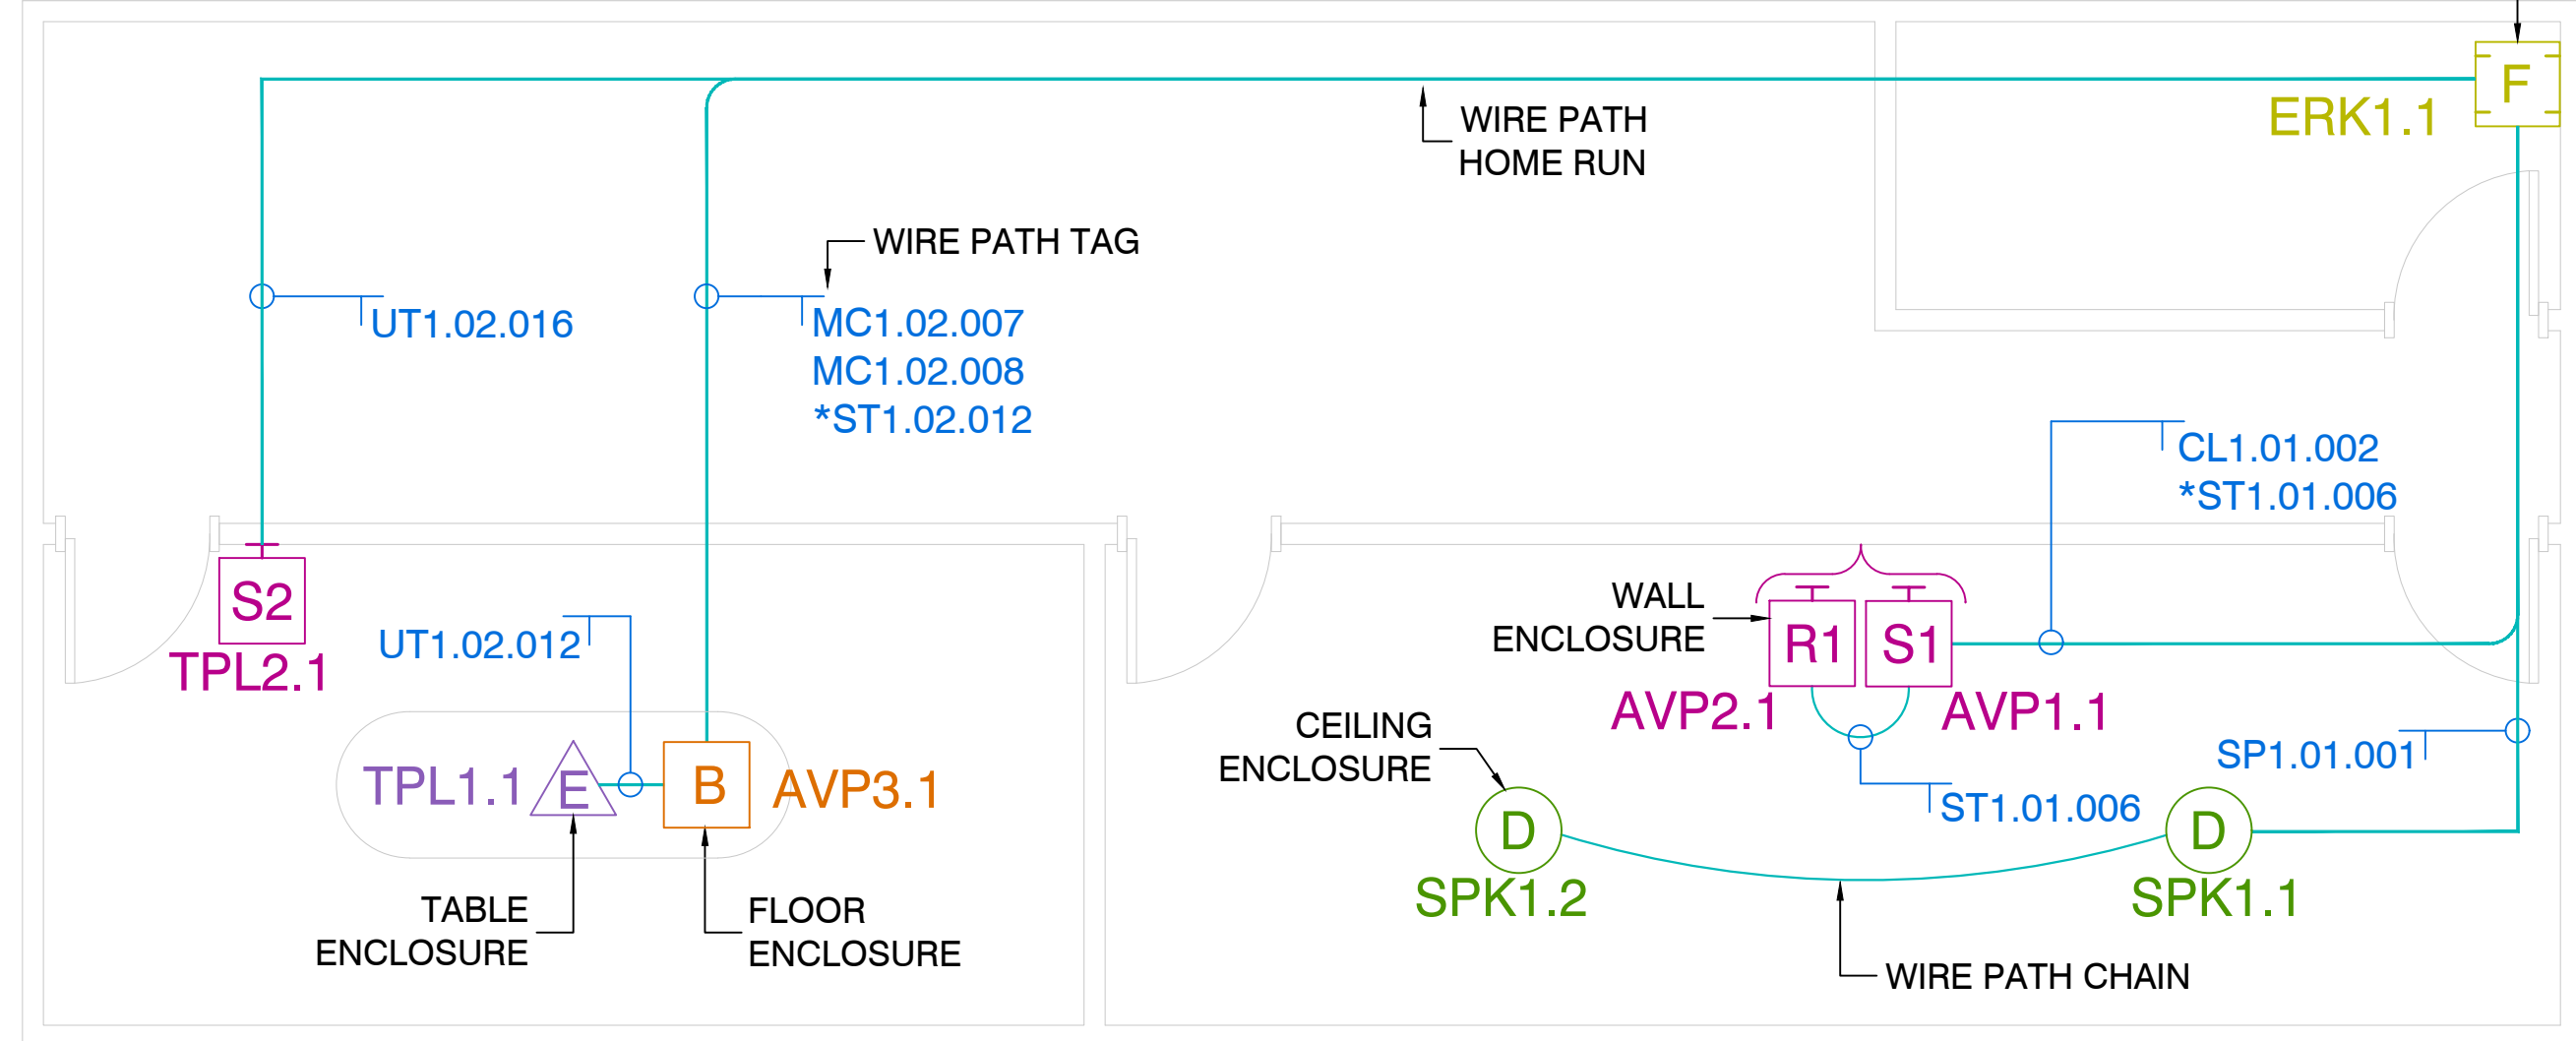


LOCATION EXAMPLE

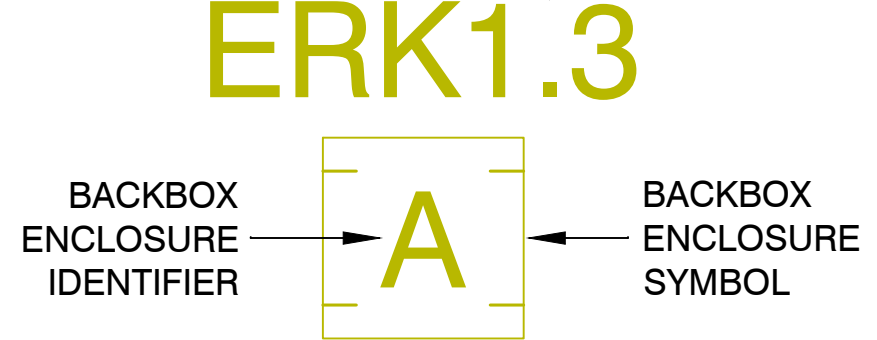


WIRE PATH TAG EXAMPLE	

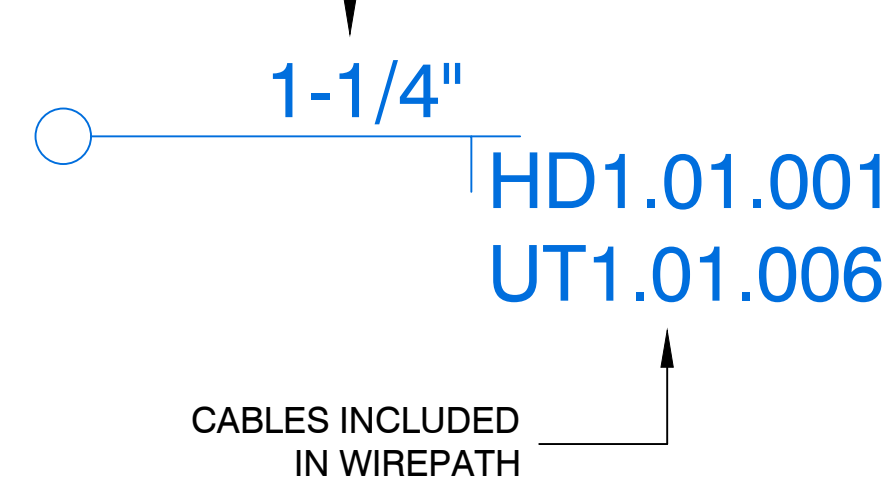

AV300 EQUIPMENT PLACEMENT EXAMPLE

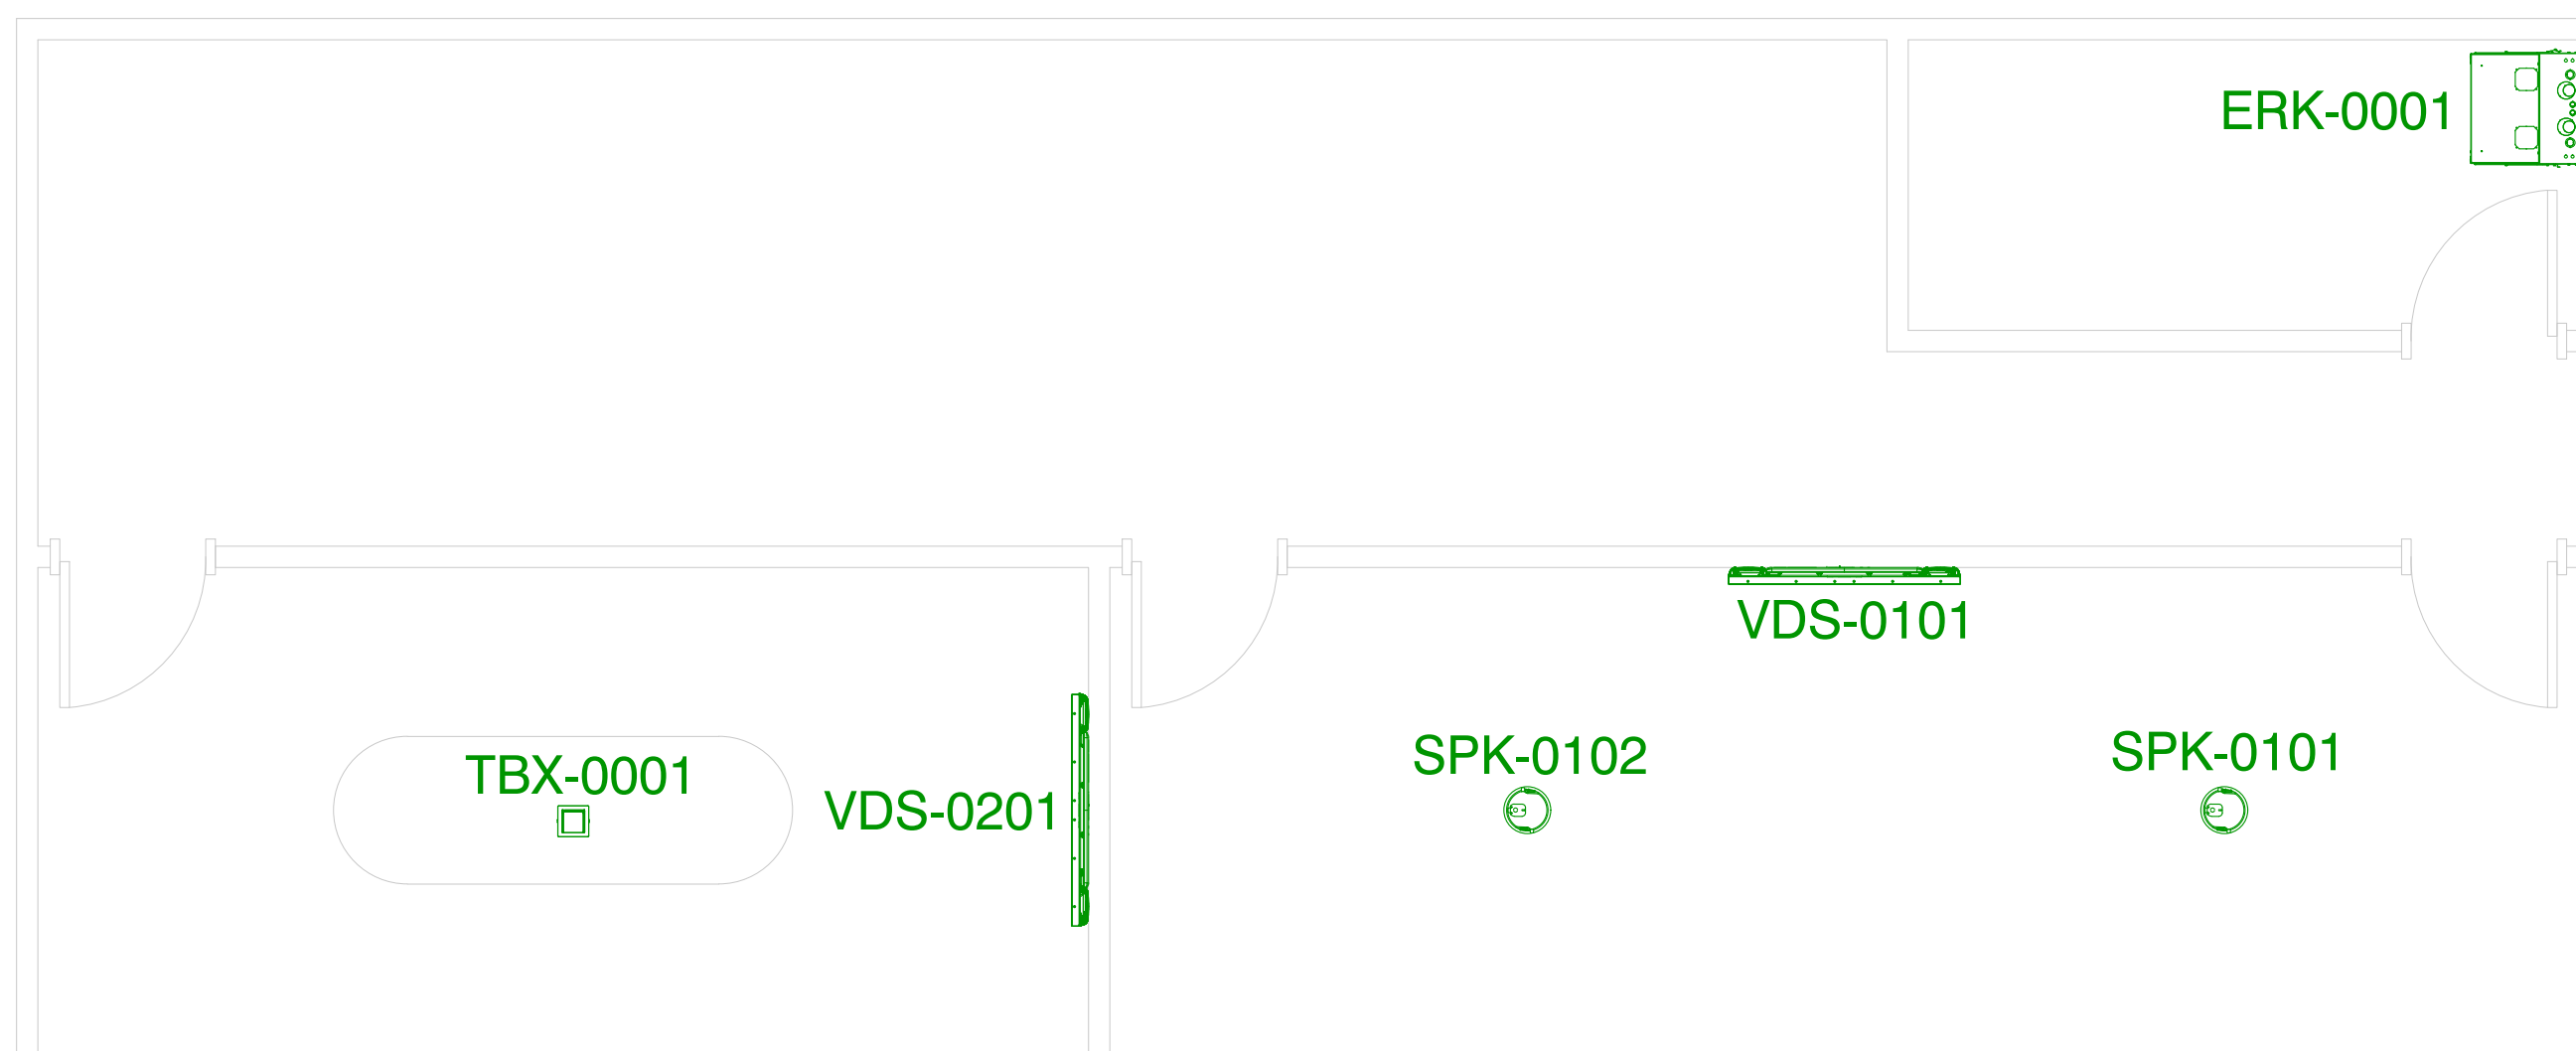

EQUIPMENT BLOCK EXAMPLE

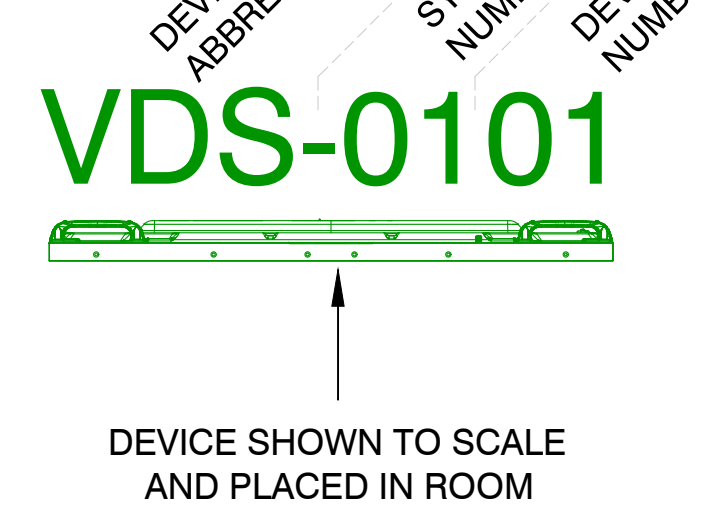


FILE NAME: A:\000.DWG

ABRV.	DESCRIPTION
AAP	AMPLIFIED AUDIO PANEL
ACP	AUDIO CONTROL PLATE
ACU	ACOUSTIC MATERIAL
ADC	AUDIO CONFERENCING
ALS	ASSISTED LISTENING SYSTEM
AMP	AMPLIFIER
AMS	ASSET MANAGEMENT
ANN	ANNOTATOR
ANT	ANTENNA
ARS	AUDIO RESPONSE SYSTEM
ASP	AUDIO SIGNAL PROCESSOR
AVF	AUDIO/VIDEO FURNITURE
AVL	AUDIO/VIDEO LIFT
AVP	AUDIO/VIDEO PANEL
AVT	AUDIO/VIDEO PANEL
BAG	EQUIPMENT BAG
BGM	BACKGROUND MUSIC SYSTEM
BOB	BREAK OUT BOX
CAM	CAMERA
CBX	CEILING BOX
CCU	CAMERA CONTROL UNIT
CLK	CLOCK
CNT	CONTROLLER
CNV	CONVERTER
COD	ENCODER/DECODER
CPU	COMPUTER
CRD	CARD/MODULE/INSERT
DAR	DIGITAL AUDIO RECORDER
DMP	DIGITAL MEDIA PLAYER
DMR	DIGITAL MEDIA RECORDER
DMT	DIGITAL MEDIA TRANSMISSION
DOC	DOCUMENT CAMERA
DSP	DIGITAL SIGNAGE SYSTEM
DTP	DISTANCE TRANSPORT
DVR	DIGITAL VIDEO RECORDER
DWR	DRAWER
EFX	EFFECTS PROCESSOR
EMI	IR/RF EMITTER
ENC	CHASSIS/CARD ENCLOSURE
ERK	EQUIPMENT RACK
FAN	FAN
FBX	FLOOR BOX
GUI	GRAPHICAL USER INTERFACE
ICS	INTERCOM SYSTEM
IFB	INTERUPTED FOLDBACK
INT	INTERFACE
IWB	WHITE BOARD
KPD	KEYPAD CONTROL
LEN	LENS
LGT	LIGHTING SYSTEM
MDI	MIDI CONTROLLER
MIC	MICROPHONE
MIX	MIXER
MOD	MODULATOR/DEMODULATOR
MON	MONITOR
MSG	MESSAGING SYSTEMS
MSK	SOUND MASKING SYSTEM
MTR	MAGNETIC TAPE RECORDER
NCS	NURSE CALL SYSTEM
NMD	NETWORK MEDIA DEVICE
NVR	NETWORK VIDEO RECORDER
NWD	NETWORK DEVICE
ODR	OPTICAL DISK RECORDER
PAS	PUBLIC ADDRESS SYSTEM

ABRV.	DESCRIPTION
PGS	PAGING SYSTEM
PPL	PATCH PANEL
PRJ	PROJECTOR
PWR	POWER DEVICE
REM	REMOTE CONTROL
RMK	RACK MOUNT KIT
ROB	ROBOTIC SYSTEM
RTS	DISCUSSION SYSTEM
SBX	STAGE BOX/SNAKE
SCN	PROJECTION SCREEN
SCP	PROJECTION SCREEN CONTROL PLATE
SCR	SCALER/SCAN CONVERTER
SNS	SENSOR DEVICE
SOF	SOFTWARE
SPK	SPEAKER
SPT	RF SPLITTER
SWT	SWITCHER
TBX	TABLE BOX
TEL	TELEPHONES
TMP	TAPE MEDIA PLAYER
TPL	TOUCH PANEL
TRX	TRANSMITTER/RECIEVER
UPS	UNINTERRUPTABLE POWER SUPPLY
VDC	VIDEO CONFERENCING
VDS	VIDEO DISPLAY
VSP	VIDEO SIGNAL PROCESSOR
VWS	VIDEO WALL SYSTEM
WAP	WIRELESS ACCESS POINT
WBX	WALL BOX
WMR	WIRELESS TX/RX
XDA	DISTRIBUTION AMPLIFIER
XMR	TRANSFORMER
XXX	UNKNOWN

CABLE LEGEND				
ID	MAKE	MODEL	DESCRIPTION	PLENUM
CONTROL				
CL1	WEST PENN	25510BGY	CONTROL CABLE	
CL2				
CL3				
CL4				
CL5				
COAX				
CX1	WEST PENN	2584BK	ANTENNA CABLE	
CX2				
CX3				
CX4				
CX5				
FIBER OPTIC				
FB1				
FB2				
FB3				
FB4				
HDMI				
HD1			3' HDMI CABLE	
HD2			6' HDMI CABLE	
HD3			10' HDMI CABLE	
HD4			15' HDMI CABLE	
HD5			30' HDMI CABLE	
HD6				
HD7				
HD8				
MICROPHONE OR LINE LEVEL AUDIO				
MC1	WEST PENN	25291BBK	MIC/LINE CABLE	
MC2				
MC3				
MC4				
MC5				
MULTI-FUNCTION				
MF1				
MF2				
MF3				
MF4				
POWER				
PW1				
PW2				
PW3				
PW4				
PW5				
SPECIAL				
SL1				
SL2				
SL3				
SL4				
SPEAKER				
SP1	WEST PENN	25225BGY	16AWG SPEAKER CABLE	
SP2				
SP3				
SP4				
SP5				
SHIELDED TWISTED PAIR				
ST1	CRESTRON	DM-CBL-8G-P-SP1000	HDBASET CABLE	
ST2				
ST3				
ST4				
ST5				
USB				
US1				
US2				
US3				
US4				
US5				
UNSHIELDED TWISTED PAIR				
UT1	WEST PENN	254246ABK	DATA CABLE	
UT2				
UT3				
UT4				
UT5				

AV800 SINGLE LINE DIAGRAM EXAMPLE

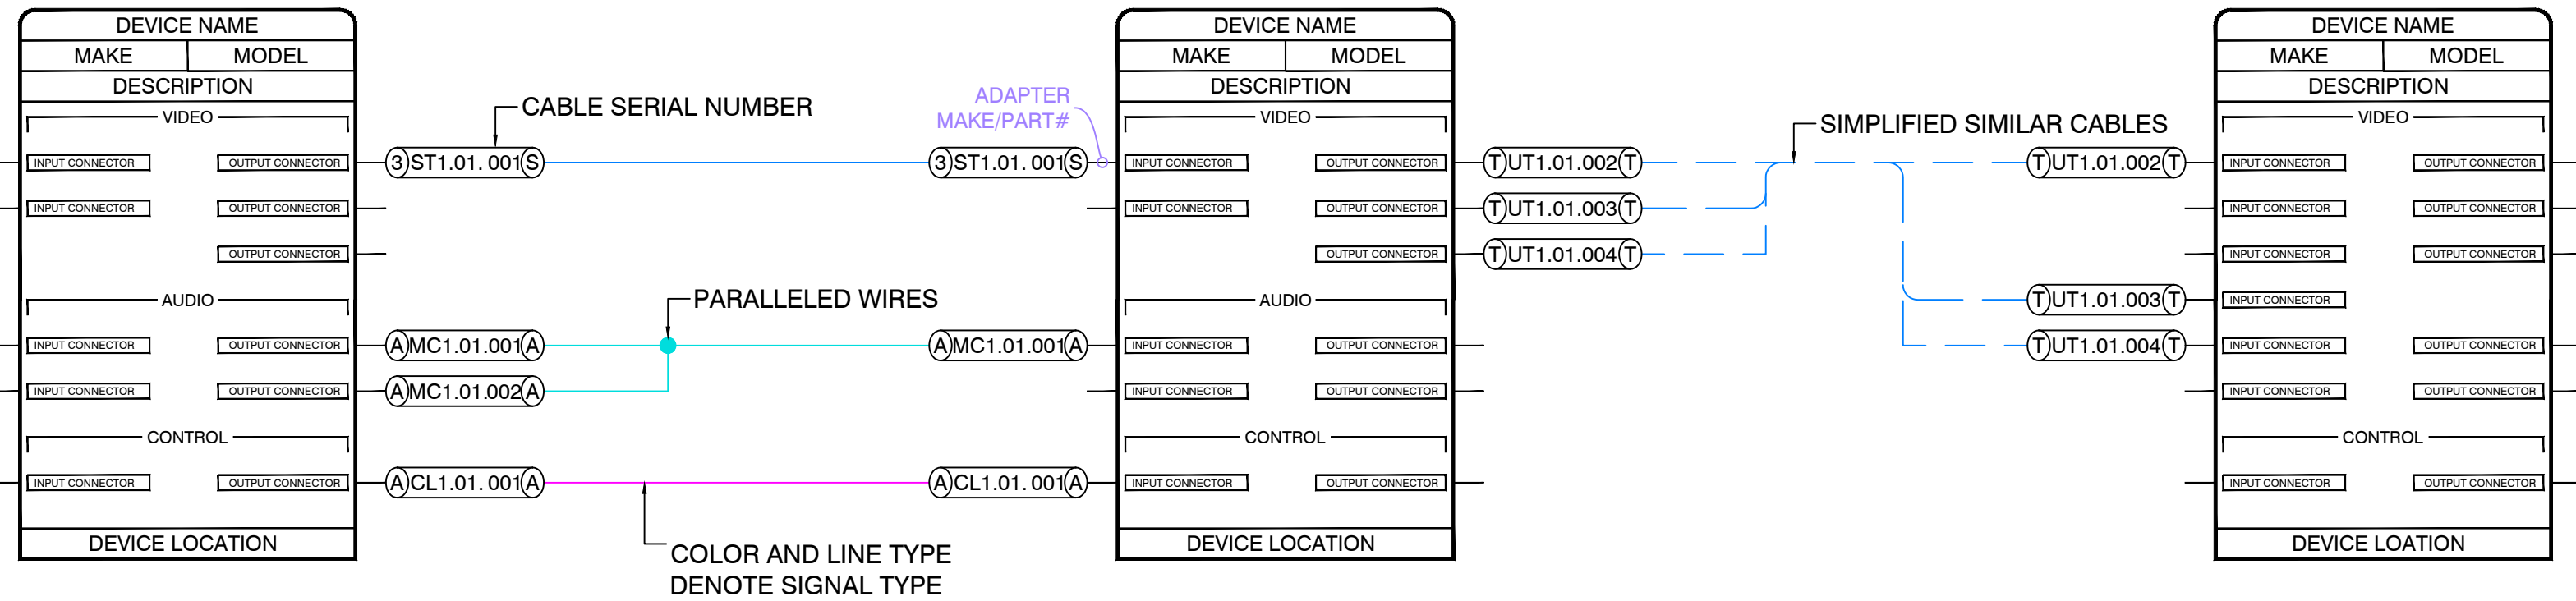

AV800 CABLE SERIAL NUMBER EXAMPLE

FROM NMD-0001/AV803

TO SWT-0002/AV801

CALLOUT TO DETAIL ON AV004

OUTPUT CONNECTOR TYPE

CABLE TYPE

SYSTEM DRAWING NUMBER

CABLE NUMBER

INPUT CONNECTOR TYPE

SOURCE DEVICE DESIGNATION

SOURCE DEVICE DRAWING

DESTINATION DESIGNATION

DESTINATION DEVICE DRAWING

LINE DESIGNATIONS KEY

— BULK - AUDIO

- - - PATCH - AUDIO

— BULK - VIDEO

- - - PATCH - VIDEO

— BULK - CONTROL

- - - PATCH - CONTROL

— BULK - GENERIC

- - - PATCH - GENERIC

AV002

FILE NAME: AV000.DWG



PROJECT INFORMATION

5853

APPELLATION SUN VALLEY
AUDIO VIDEO INTEGRATION

CUSTOMER NAME:	HARRIMAN SUN VALLEY HOTEL	CUSTOMER NUMBER:	APH001
SITE NAME:	HARRIMAN SUN VALLEY HOTEL	SITE NUMBER:	72398311

SITE ADDRESS:
300 E RIVER ST
KETCHUM, ID 83353

SALES PERSON:	JEREMY WADDELL	ENGINEERED BY:	ADAM HANDY
DRAWN BY:	ELU ANDERSON	PROJECT MANAGER:	JEREMY WADDELL

DRAWING SET INFORMATION

PHASE:	SUBMITTAL
PUBLISH DATE:	11/20/2025
PLOT SIZE:	ARCH FULL BLEED E (36.00 X 48.00 INCHES)
PLOT SCALE:	1" = 1'-0"
APPROVED BY:	----

SHEET REVISION INFORMATION

REVISION:	REVISION DATE:	----
----	REVISION DESCRIPTION:	----

REVISION & ISSUE HISTORY	REV.	DATE:
1	1	11/20/2025
2	2	11/20/2025
3	3	11/20/2025
4	4	11/20/2025
5	5	11/20/2025
6	6	11/20/2025
7	7	11/20/2025
8	8	11/20/2025
9	9	11/20/2025
10	10	11/20/2025
11	11	11/20/2025
12	12	11/20/2025
13	13	11/20/2025
14	14	11/20/2025
15	15	11/20/2025
16	16	11/20/2025
17	17	11/20/2025
18	18	11/20/2025
19	19	11/20/2025
20	20	11/20/2025

APPELLATION SUN VALLEY
GENERAL DRAWINGS
AV LEGENDS AND KEYS
STRUCTURED CABLING

SHEET CABLE LEGEND				
ABBREV	MAKE	MODEL	DESCRIPTION	QTY
SP1	WEST PENN	25225BGY	16AWG SPEAKER CABLE	1
ST1	CRESTRON	DM-CBL-8G-P-SP1000	HDBASET CABLE	1
UT1	WEST PENN	254246ABK	DATA CABLE	11

SHEET ENCLOSURE LEGEND						
LOCATION	SYM	GANG	DESCRIPTION	ELEVATION	SHEET	DETAIL
AVP4	[Symbol]	1	3" DEEP BACKBOX	RECEPTACLE HEIGHT	AV701	4
AVP6	[Symbol]	3	3" DEEP BACKBOX	SWITCH HEIGHT	AV701	6
ERK1	[Symbol]	0	26RU EQUIPMNET RACK		AV901	1
SPK6	[Symbol]	1	SPEAKER LOCATION	FIELD DETERMINED		
TPL2	[Symbol]	2	3" DEEP BACKBOX	SWITCH HEIGHT	AV701	2
VDS2	[Symbol]	1	3" DEEP BACKBOX	FIELD DETERMINED		



PROJECT INFORMATION

5853	
APPELLATION SUN VALLEY	
AUDIO VIDEO INTEGRATION	
CUSTOMER NAME:	HARRIMAN SUN VALLEY HOTEL
CUSTOMER NUMBER:	APH001
SITE NAME:	HARRIMAN SUN VALLEY HOTEL
SITE NUMBER:	72338311
SITE ADDRESS:	300 E RIVER ST KETCHUM, ID 83353
SALES PERSON:	JEREMY WADDELL
ENGINEERED BY:	ADAM HANDY
DRAWN BY:	EU ANDERSON
PROJECT MANAGER:	JEREMY WADDELL

DRAWING SET INFORMATION

PHASE:	SUBMITTAL
PUBLISH DATE:	11/20/2025
PLOT SIZE:	ARCH FULL BLEED E (36.00 X 48.00 INCHES)
PLOT SCALE:	1" = 1'-0"
APPROVED BY:	

SHEET REVISION INFORMATION

REVISION:	REVISION DATE:	11/20/2025
C	REVISION DESCRIPTION:	RESUBMITTAL
REVISION & ISSUE HISTORY		
ISSUED FOR:	REV.	DATE
ARCHITECTURAL UPDATES	1	11/20/2025
	2	
	3	
	4	
	5	
	6	
	7	
	8	
	9	
	10	




1 PARKING LEVEL - FLOOR PLAN
SCALE: 1/8" = 1'-0"

APPELLATION SUN VALLEY
WIREPATH AND BACKBOXES
LEVEL P1

AV101

SHEET CABLE LEGEND				
ABBREV	MAKE	MODEL	DESCRIPTION	QTY
HD4			15' HDMI CABLE	6
HD5			30' HDMI CABLE	2
MC1	WEST PENN	25291BBK	MIC/LINE CABLE	4
SP1	WEST PENN	25225BGY	16AWG SPEAKER CABLE	2
ST1	CRESTRON	DM-CBL-8G-P-SP1000	HDBASET CABLE	2
UT1	WEST PENN	254246ABK	DATA CABLE	16

SHEET ENCLOSURE LEGEND					
LOCATION	SYM	GANG	DESCRIPTION	ELEVATION	SHEET
AVP3	[B]	3	3" DEEP BACKBOX	SWITCH HEIGHT	AV701
AVP4	[B]				AV701
AVP5	[B]	2	3" DEEP BACKBOX	RECEPTACLE HEIGHT	AV701
AVP6	[B]	3	3" DEEP BACKBOX	SWITCH HEIGHT	AV701
DME1	[B]	1	3" DEEP BACKBOX	+11' AFF	
ERK2	[E]	0	26RU EQUIPMNET RACK		
SPK3	[E]	1	LANDSCAPE SPEAKER	FIELD DETERMINED	
SPK4	[E]	1	LANDSCAPE SUBWOOFER	FIELD DETERMINED	
TPL2	[B]	2	3" DEEP BACKBOX	SWITCH HEIGHT	AV701
VDS1	[B]	1	3" DEEP BACKBOX	FIELD DETERMINED	
VDS3	[B]		DISPLAY LOCATION	60" AFF	

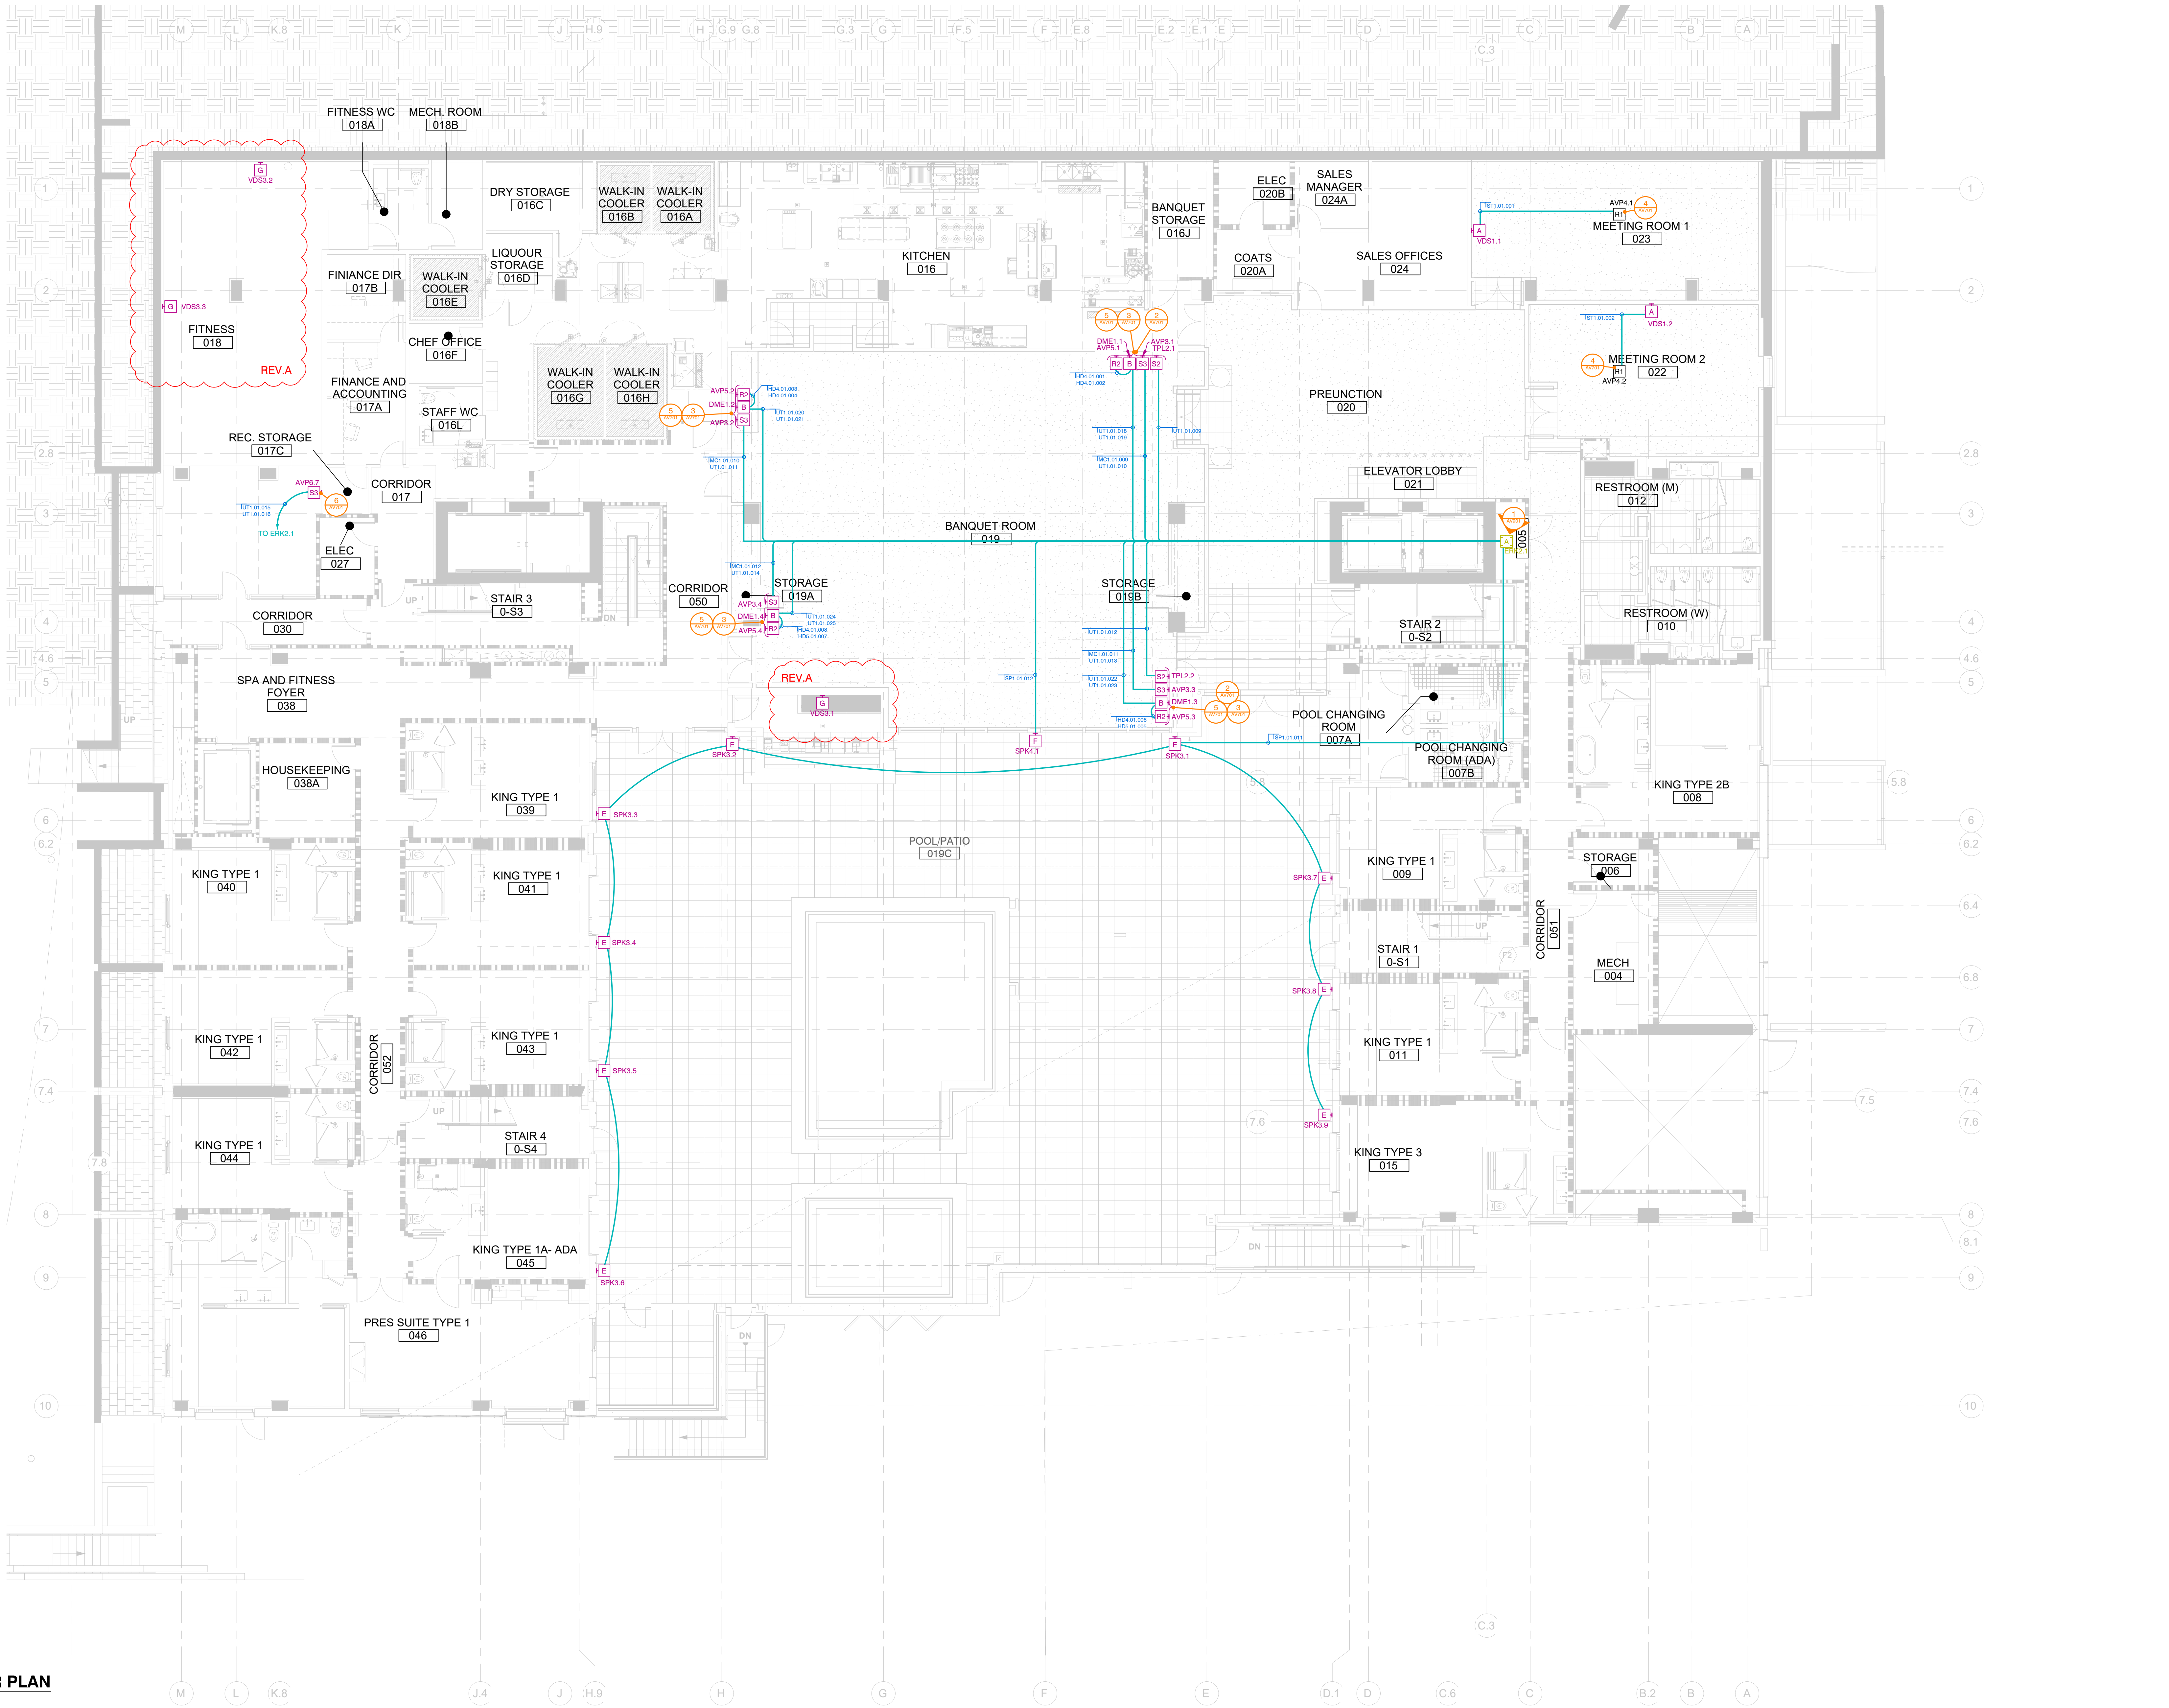

1 MAIN LEVEL - FLOOR PLAN
SCALE: 1/8" = 1'-0"



PROJECT INFORMATION

5853
APPELLATION SUN VALLEY
AUDIO VIDEO INTEGRATION

CUSTOMER NAME:	HARRIMAN SUN VALLEY HOTEL	CUSTOMER NUMBER:	APH001
SITE NAME:	HARRIMAN SUN VALLEY HOTEL	SITE NUMBER:	72338311
SITE ADDRESS:	300 E RIVER ST KETCHUM, ID 83353		
SALES PERSON:	JEREMY WADDELL	ENGINEERED BY:	ADAM HANDY
DRAWN:	ELI ANDERSON	PROJECT MANAGER:	JEREMY WADDELL

DRAWING SET INFORMATION

PHASE:	SUBMITTAL
PUBLISH DATE:	11/20/2025
PLOT SIZE:	ARCH FULL BLEED E (36.00 X 48.00 INCHES)
PLOT SCALE:	1" = 1'-0"
APPROVED BY:	---


SHEET REVISION INFORMATION

REVISION:	REVISION DATE:	10/10/2025
A	REVISION DESCRIPTION:	RESUBMITTAL
REVISION & ISSUE HISTORY		
ISSUED FOR:	REV.	DATE:


APPELLATION SUN VALLEY
WIREPATH AND BACKBOXES
LEVEL 1

AV102

SHEET ENCLOSURE LEGEND						
LOCATION	SYM	GANG	DESCRIPTION	ELEVATION	SHEET	DETAIL
ERK2	Ⓜ	0	26RU EQUIPMNET RACK			
SPK1	Ⓢ	0	6" SELF ENCLOSED SPEAKER	FLUSH IN CEILING		
SPK2	Ⓢ	0	8" SELF ENCLOSED SUBWOOFER	FLUSH IN CEILING		

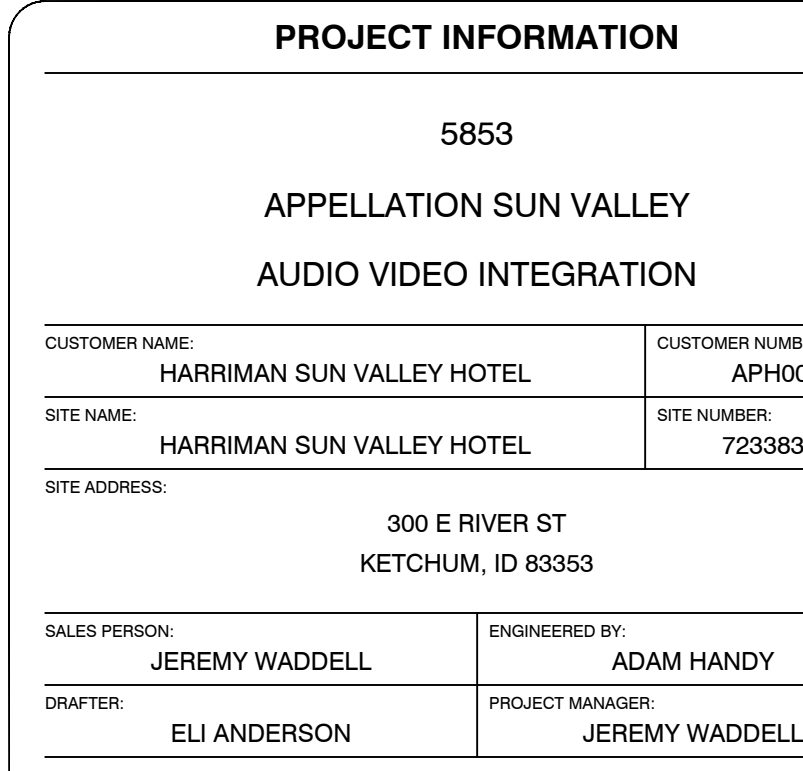

DRAWING SET INFORMATION	
PHASE:	SUBMITTAL
PUBLISH DATE:	11/20/2025
PLOT SIZE:	ARCH FULL BLEED E (36.00 X 48.00 INCHES)
PLOT SCALE:	1" = 1'-0"
APPROVED BY:	*****

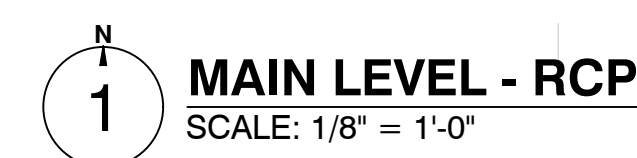[illegible]

APPELLATION SUN VALLEY

REFLECTED CEILING

LEVEL 1

AV202


FILE NAME: AV100.DWG

SHEET ENCLOSURE LEGEND						
LOCATION	SYM	GANG	DESCRIPTION	ELEVATION	SHEET	DETAIL
ERK3		0	26RU EQUIPMNET RACK			
SPK1		0	6" SELF ENCLOSED SPEAKER	FLUSH IN CEILING		
SPK2		0	8" SELF ENCLOSED SUBWOOFER	FLUSH IN CEILING		



CUSTOMER NAME: HARRIMAN SUN VALLEY HOTEL		CUSTOMER NUMBER: APH001	
SITE NAME: HARRIMAN SUN VALLEY HOTEL		SITE NUMBER: 72338311	
SITE ADDRESS: 300 E RIVER ST KETCHUM, ID 83353			
SALES PERSON: JEREMY WADDELL		ENGINEERED BY: ADAM HANDY	
DRAFTER: ELI ANDERSON		PROJECT MANAGER: JEREMY WADDELL	

DRAWING SET INFORMATION	
PHASE:	SUBMITTAL
PUBLISH DATE:	11/20/2025
PLOT SIZE:	ARCH FULL BLEED E (36.00 X 48.00 INCHES)
PLOT SCALE:	1' = 1'-0"
APPROVED BY:	

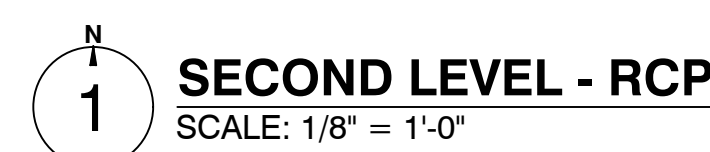[illegible]

APPELLATION SUN VALLEY


REFLECTED CEILING

LEVEL 2

AV203


FILE NAME: AV100.DWG

DESIGNATION	DESCRIPTION	LOCATION
TPL-0101	TOUCH PANEL	TPL1.1

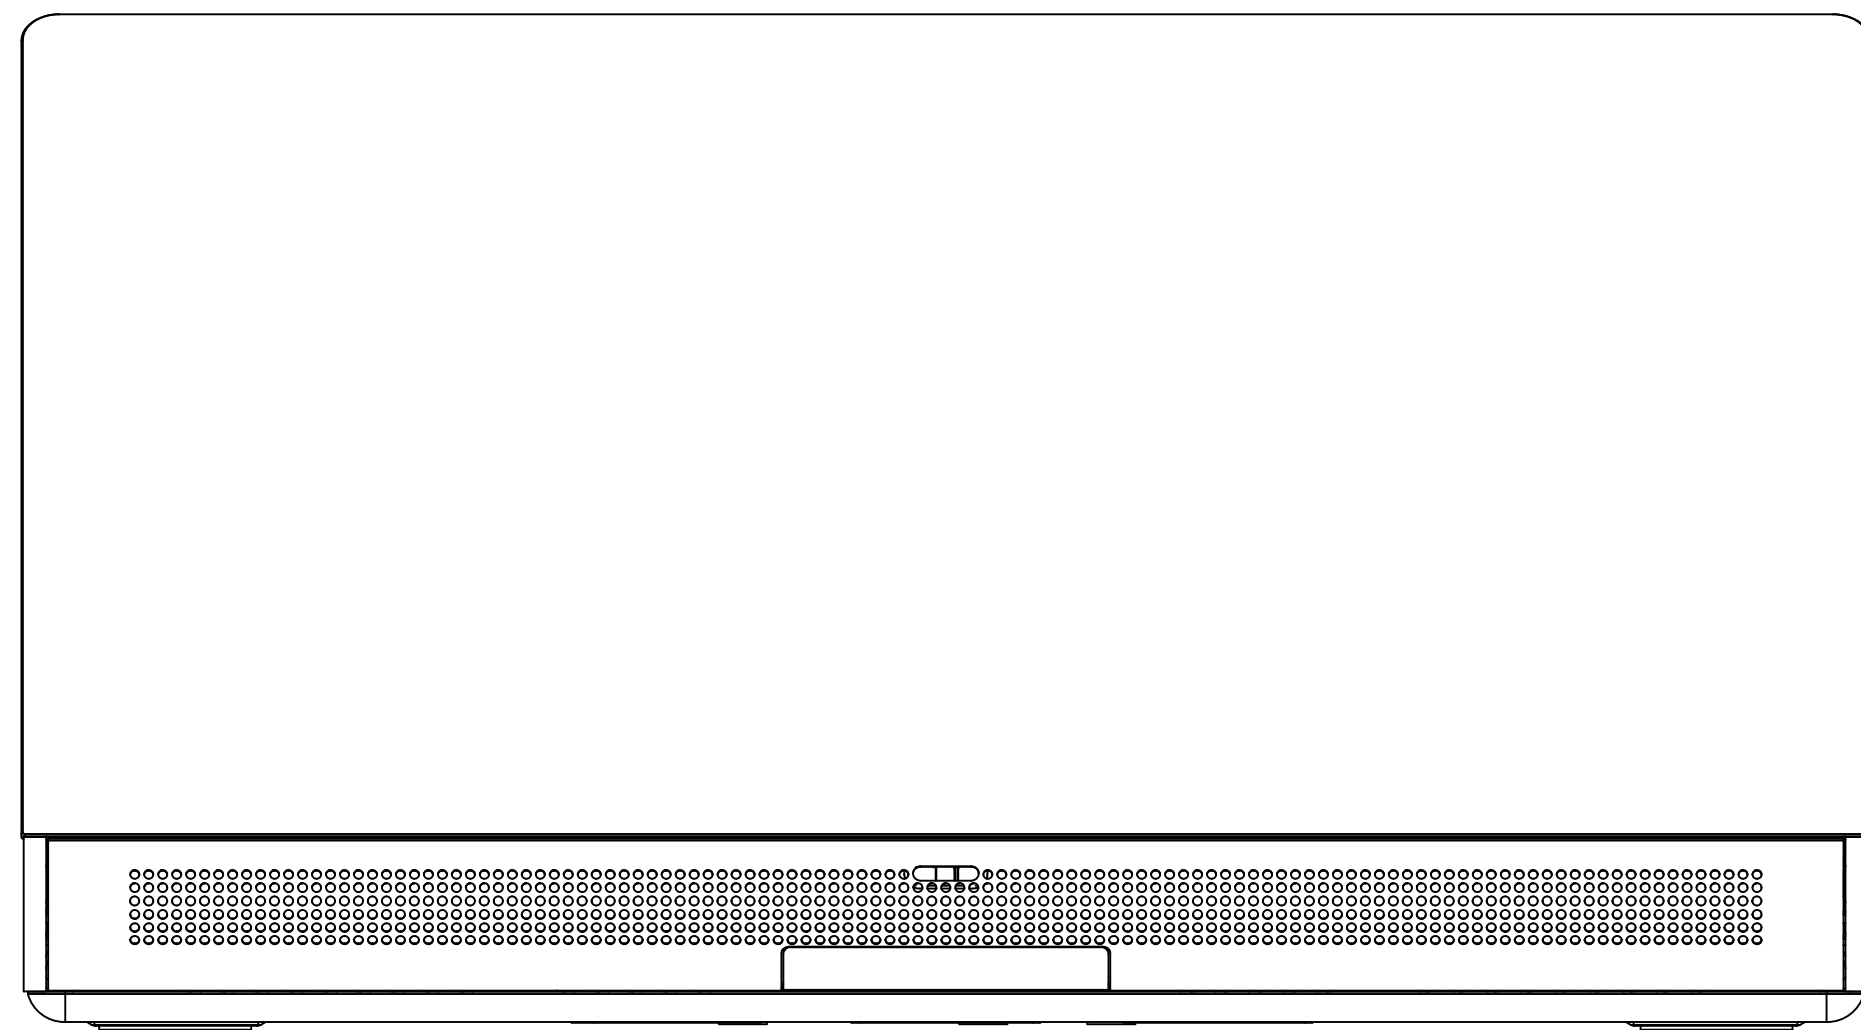


1 TPL1
CRESTRON TS-1070
SCALE: 1" = 1'-0"

DESIGNATION	DESCRIPTION	LOCATION
TPT-0101	MEETING ROOM 1 DM TX	AVP4.1
TPT-0102	MEETING ROOM 2 DM TX	AVP4.2
TPT-0103	PRIVATE DINING DM TX	AVP4.3
TPT-0104	PRIVATE DINING DM TX	AVP4.5
TPT-0105	EMPLOYEE CAFE DM TX	AVP4.4

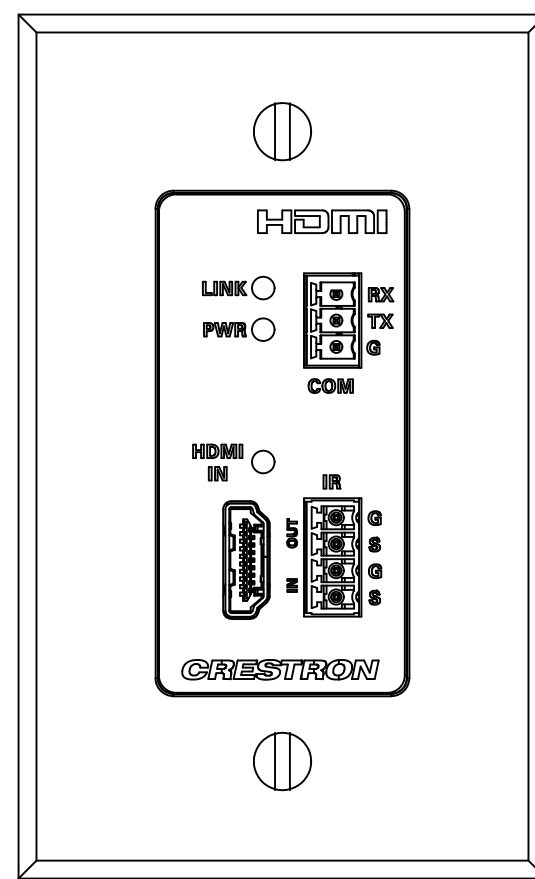


4 **AVP4**
CRESTRON HD-TXC-4KZ-101-1G-W
SCALE: 1" = 1'-0"

DESIGNATION	DESCRIPTION	LOCATION
TPL-0102	TOUCH PANEL	TPL2.1
TPL-0103	TOUCH PANEL	TPL2.2

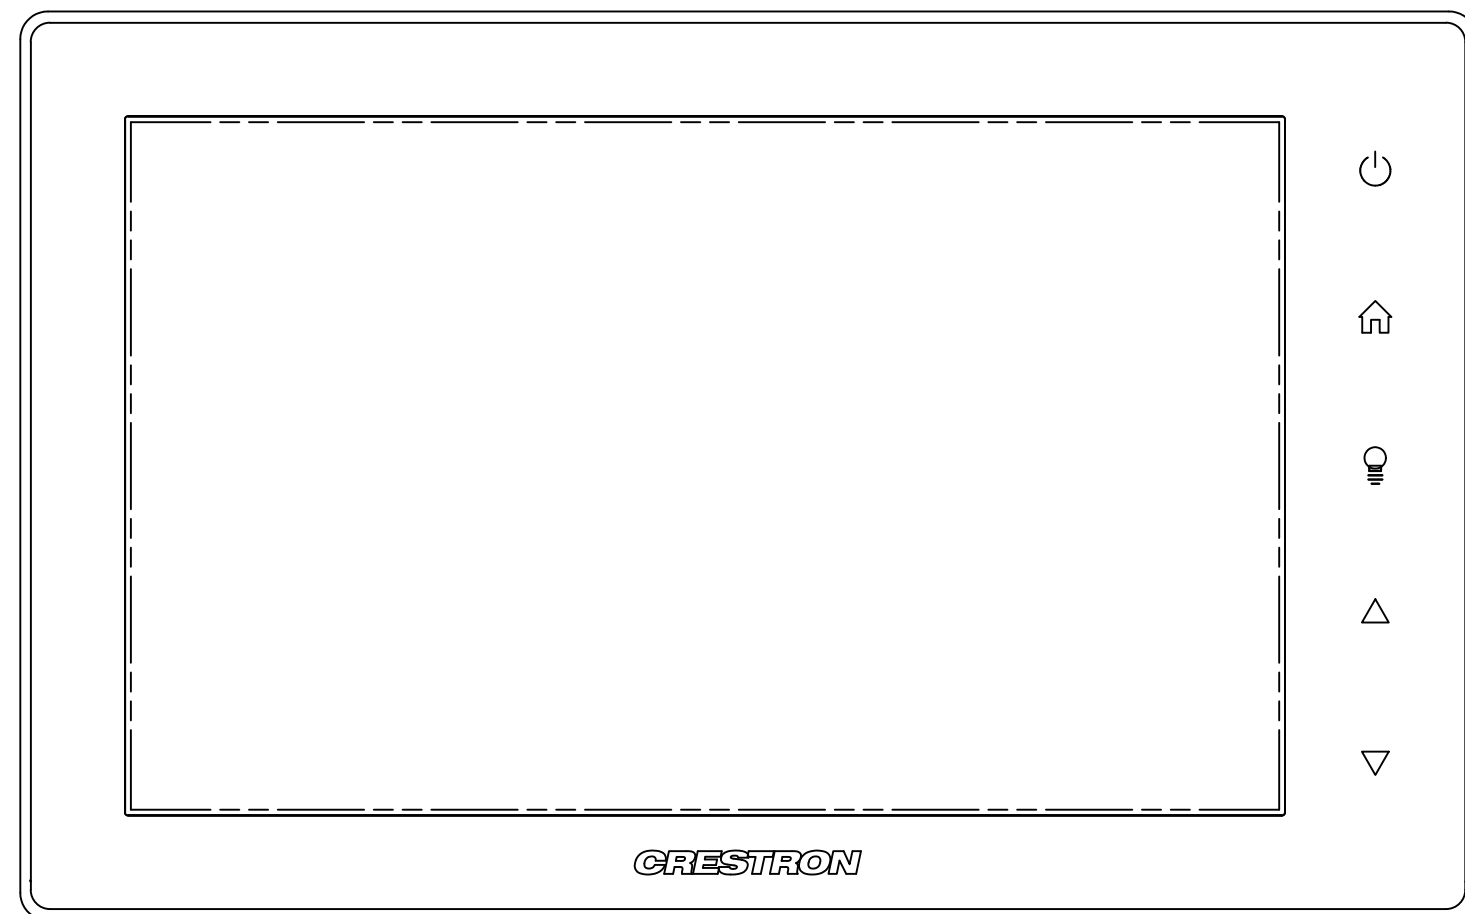


2 TPL2
CRESTRON TSW-750-W-S
SCALE: 1' = 1'-0"

DESIGNATION	DESCRIPTION	LOCATION
AVP-0111	BANQUET NORTH HDMI INPUT	AVP.1
AVP-0112	BANQUET NORTH HDMI OUTPUT	
AVP-0113	BANQUET NORTH HDMI INPUT	AVP.2
AVP-0114	BANQUET NORTH HDMI OUTPUT	
AVP-0115	HDMI INPUT	AVP.3
AVP-0116	HDMI OUTPUT	
AVP-0117	BANQUET SOUTH HDMI INPUT	AVP.4
AVP-0118	BANQUET SOUTH HDMI OUTPUT	

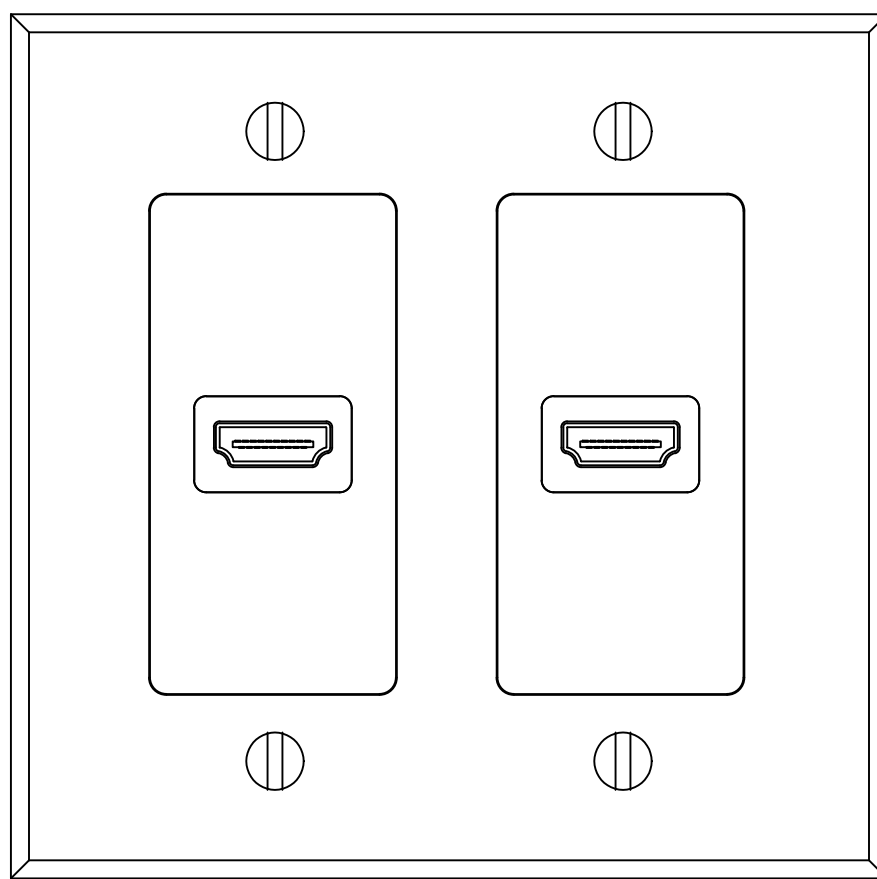


5 AVP5
DUAL C2G 41043 FOR HDMI INPUT/OUTPUT
SCALE: 1' = 1'-0"

DESIGNATION	DESCRIPTION	LOCATION
AVP-0106	BANQUET NORTH BLUETOOTH RX	AVP3.1
MIP-0101	BANQUET NORTH AUX AUDIO	
AVP-0107	BANQUET NORTH BLUETOOTH RX	AVP3.2
MIP-0102	BANQUET NORTH AUX AUDIO	
AVP-0108	BANQUET SOUTH BLUETOOTH RX	AVP3.3
MIP-0103	BANQUET SOUTH AUX AUDIO	
AVP-0109	BANQUET SOUTH BLUETOOTH RX	AVP3.4
MIP-0104	BANQUET SOUTH AUX AUDIO	

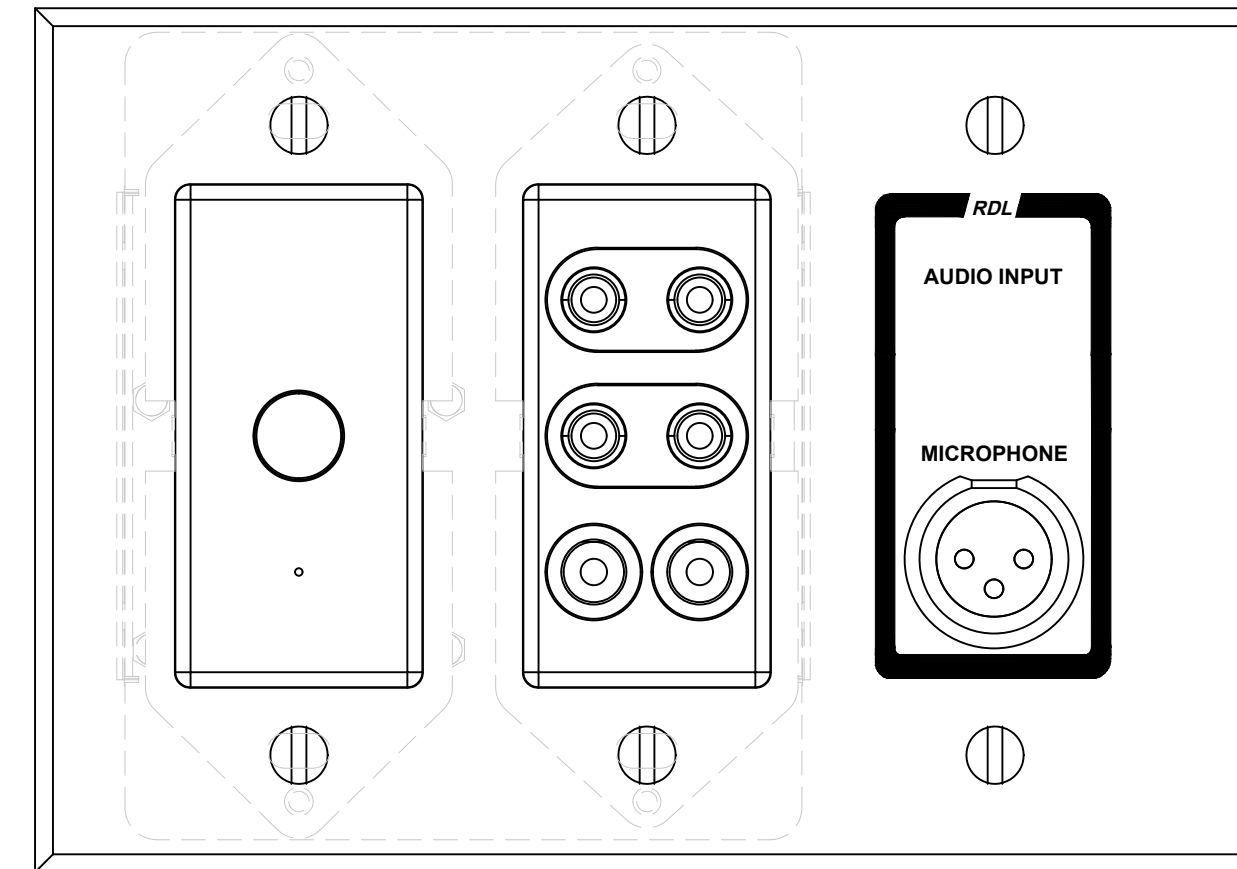

3 AVP3
DUAL C2G 41043 FOR HDMI INPUT/OUTPUT
SCALE: 1' = 1'-0"

DESIGNATION	DESCRIPTION	LOCATION
AVP-0121	SAUNA 1 BLUETOOTH RX	AVP6.2
CNT-0103	SAUNA 1 CONTROLLER	
AVP-0122	SAUNA 2 BLUETOOTH RX	AVP6.3
CNT-0104	SAUNA 2 CONTROLLER	
AVP-0123	SAUNA 3 BLUETOOTH RX	AVP6.4
CNT-0105	SAUNA 3 CONTROLLER	
AVP-0124	SAUNA 4 BLUETOOTH RX	AVP6.5
CNT-0106	SAUNA 4 CONTROLLER	
AVP-0125	SAUNA 5 BLUETOOTH RX	AVP6.6
CNT-0107	SAUNA 5 CONTROLLER	
AVP-0105	FITNESS BLUETOOTH RX	AVP6.7
CNT-0108	FITNESS CONTROLLER	
AVP-0101	PRIVATE DINING BLUETOOTH RX	AVP6.8
CNT-0109	PRIVATE DINING CONTROLLER	
AVP-0102	RESTAURANT AND BAR BLUETOOTH RX	AVP6.9
CNT-0110	RESTAURANT AND BAR CONTROLLER	
AVP-0103	ADVENTURE CLUB BLUETOOTH RX	AVP6.10
CNT-0111	ADVENTURE CLUB CONTROLLER	
AVP-0104	BAKERY BLUETOOTH RX	AVP6.11
CNT-0112	BAKERY CONTROLLER	
AVP-0126	SERVICE CORRIDOR BLUETOOTH RX	AVP6.12
CNT-0114	SERVICE CORRIDOR CONTROLLER	

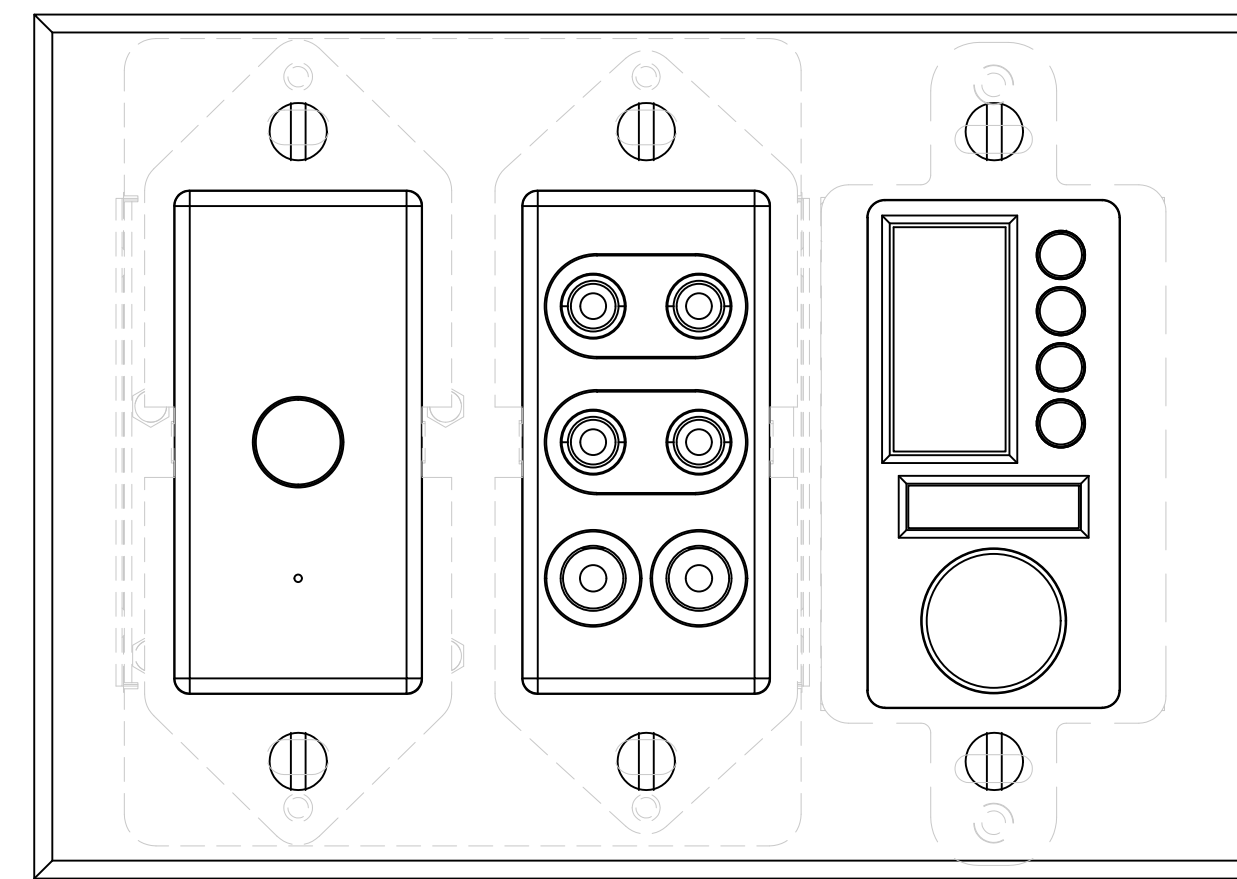

6 AVP6
SYMETRIX XIO BLUETOOTH RCA-3.5 WITH SYMETRIX 80-0171
SCALE: 1' = 1'-0"



www.marshallind.com

PROJECT INFORMATION

5853

APPELLATION SUN VALLEY
AUDIO VIDEO INTEGRATION

CUSTOMER NAME: HARRIMAN SUN VALLEY HOTEL		CUSTOMER NUMBER: APH0001
SITE NAME: HARRIMAN SUN VALLEY HOTEL		SITE NUMBER: 72383311
SITE ADDRESS: 300 E RIVER ST KETCHUM, ID 83353		
SALES PERSON: JEREMY WADDELL		ENGINEERED BY: ADAM HANDY
DRAWN BY: ELI ANDERSON		PROJECT MANAGER: JEREMY WADDELL

DRAWING SET INFORMATION

PHASE:	SUBMITTAL
PUBLISH DATE:	11/20/2025
PLOT SIZE:	ARCH FULL BLEED E (36.00 X 48.00 INCHES)
PLOT SCALE:	1" = 1'-0"
APPROVED BY:	

SHEET REVISION INFORMATION

C	REVISION DATE:	11/20/2025
	REVISION DESCRIPTION:	RESUBMITTAL

[illegible]

APPELLATION SUN VALLEY


PLATE DETAILS


UTILIZED PLATES



AV701

FILE NAME: AV700.DWG



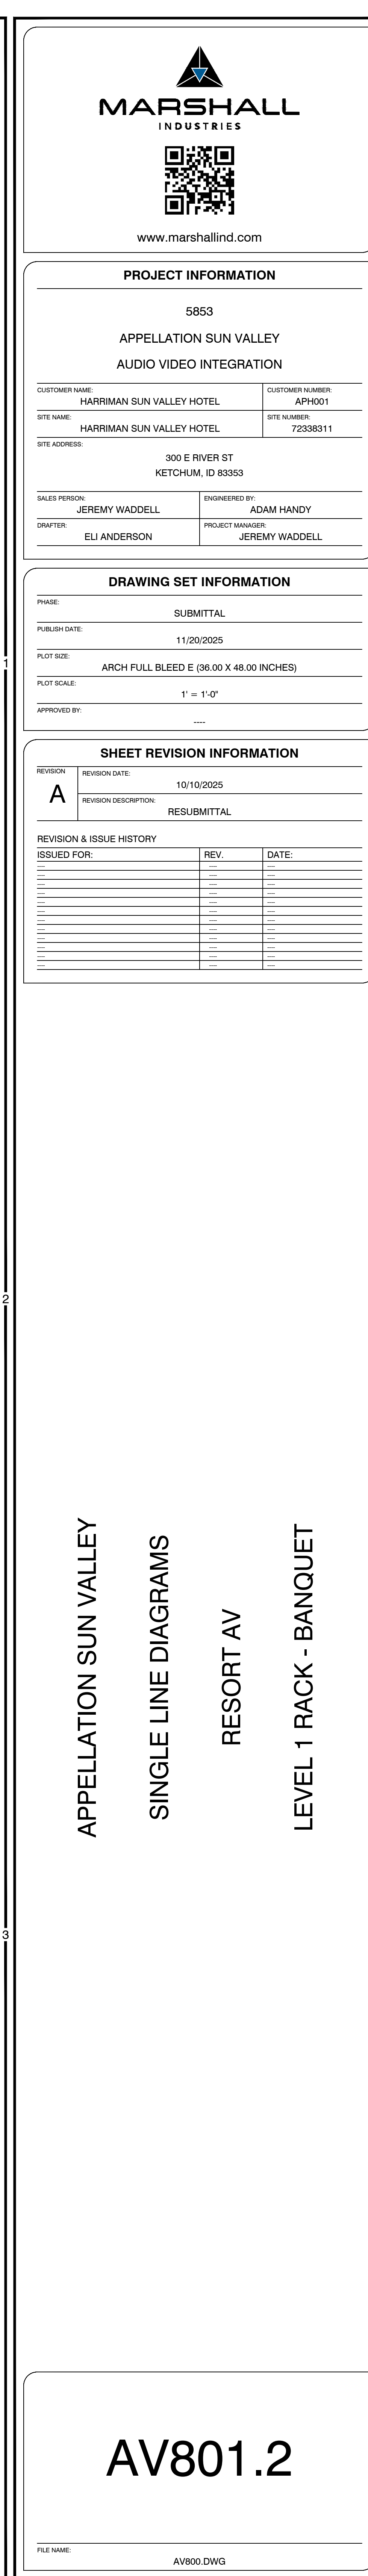

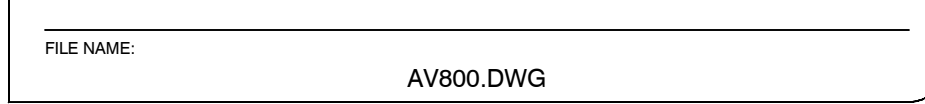

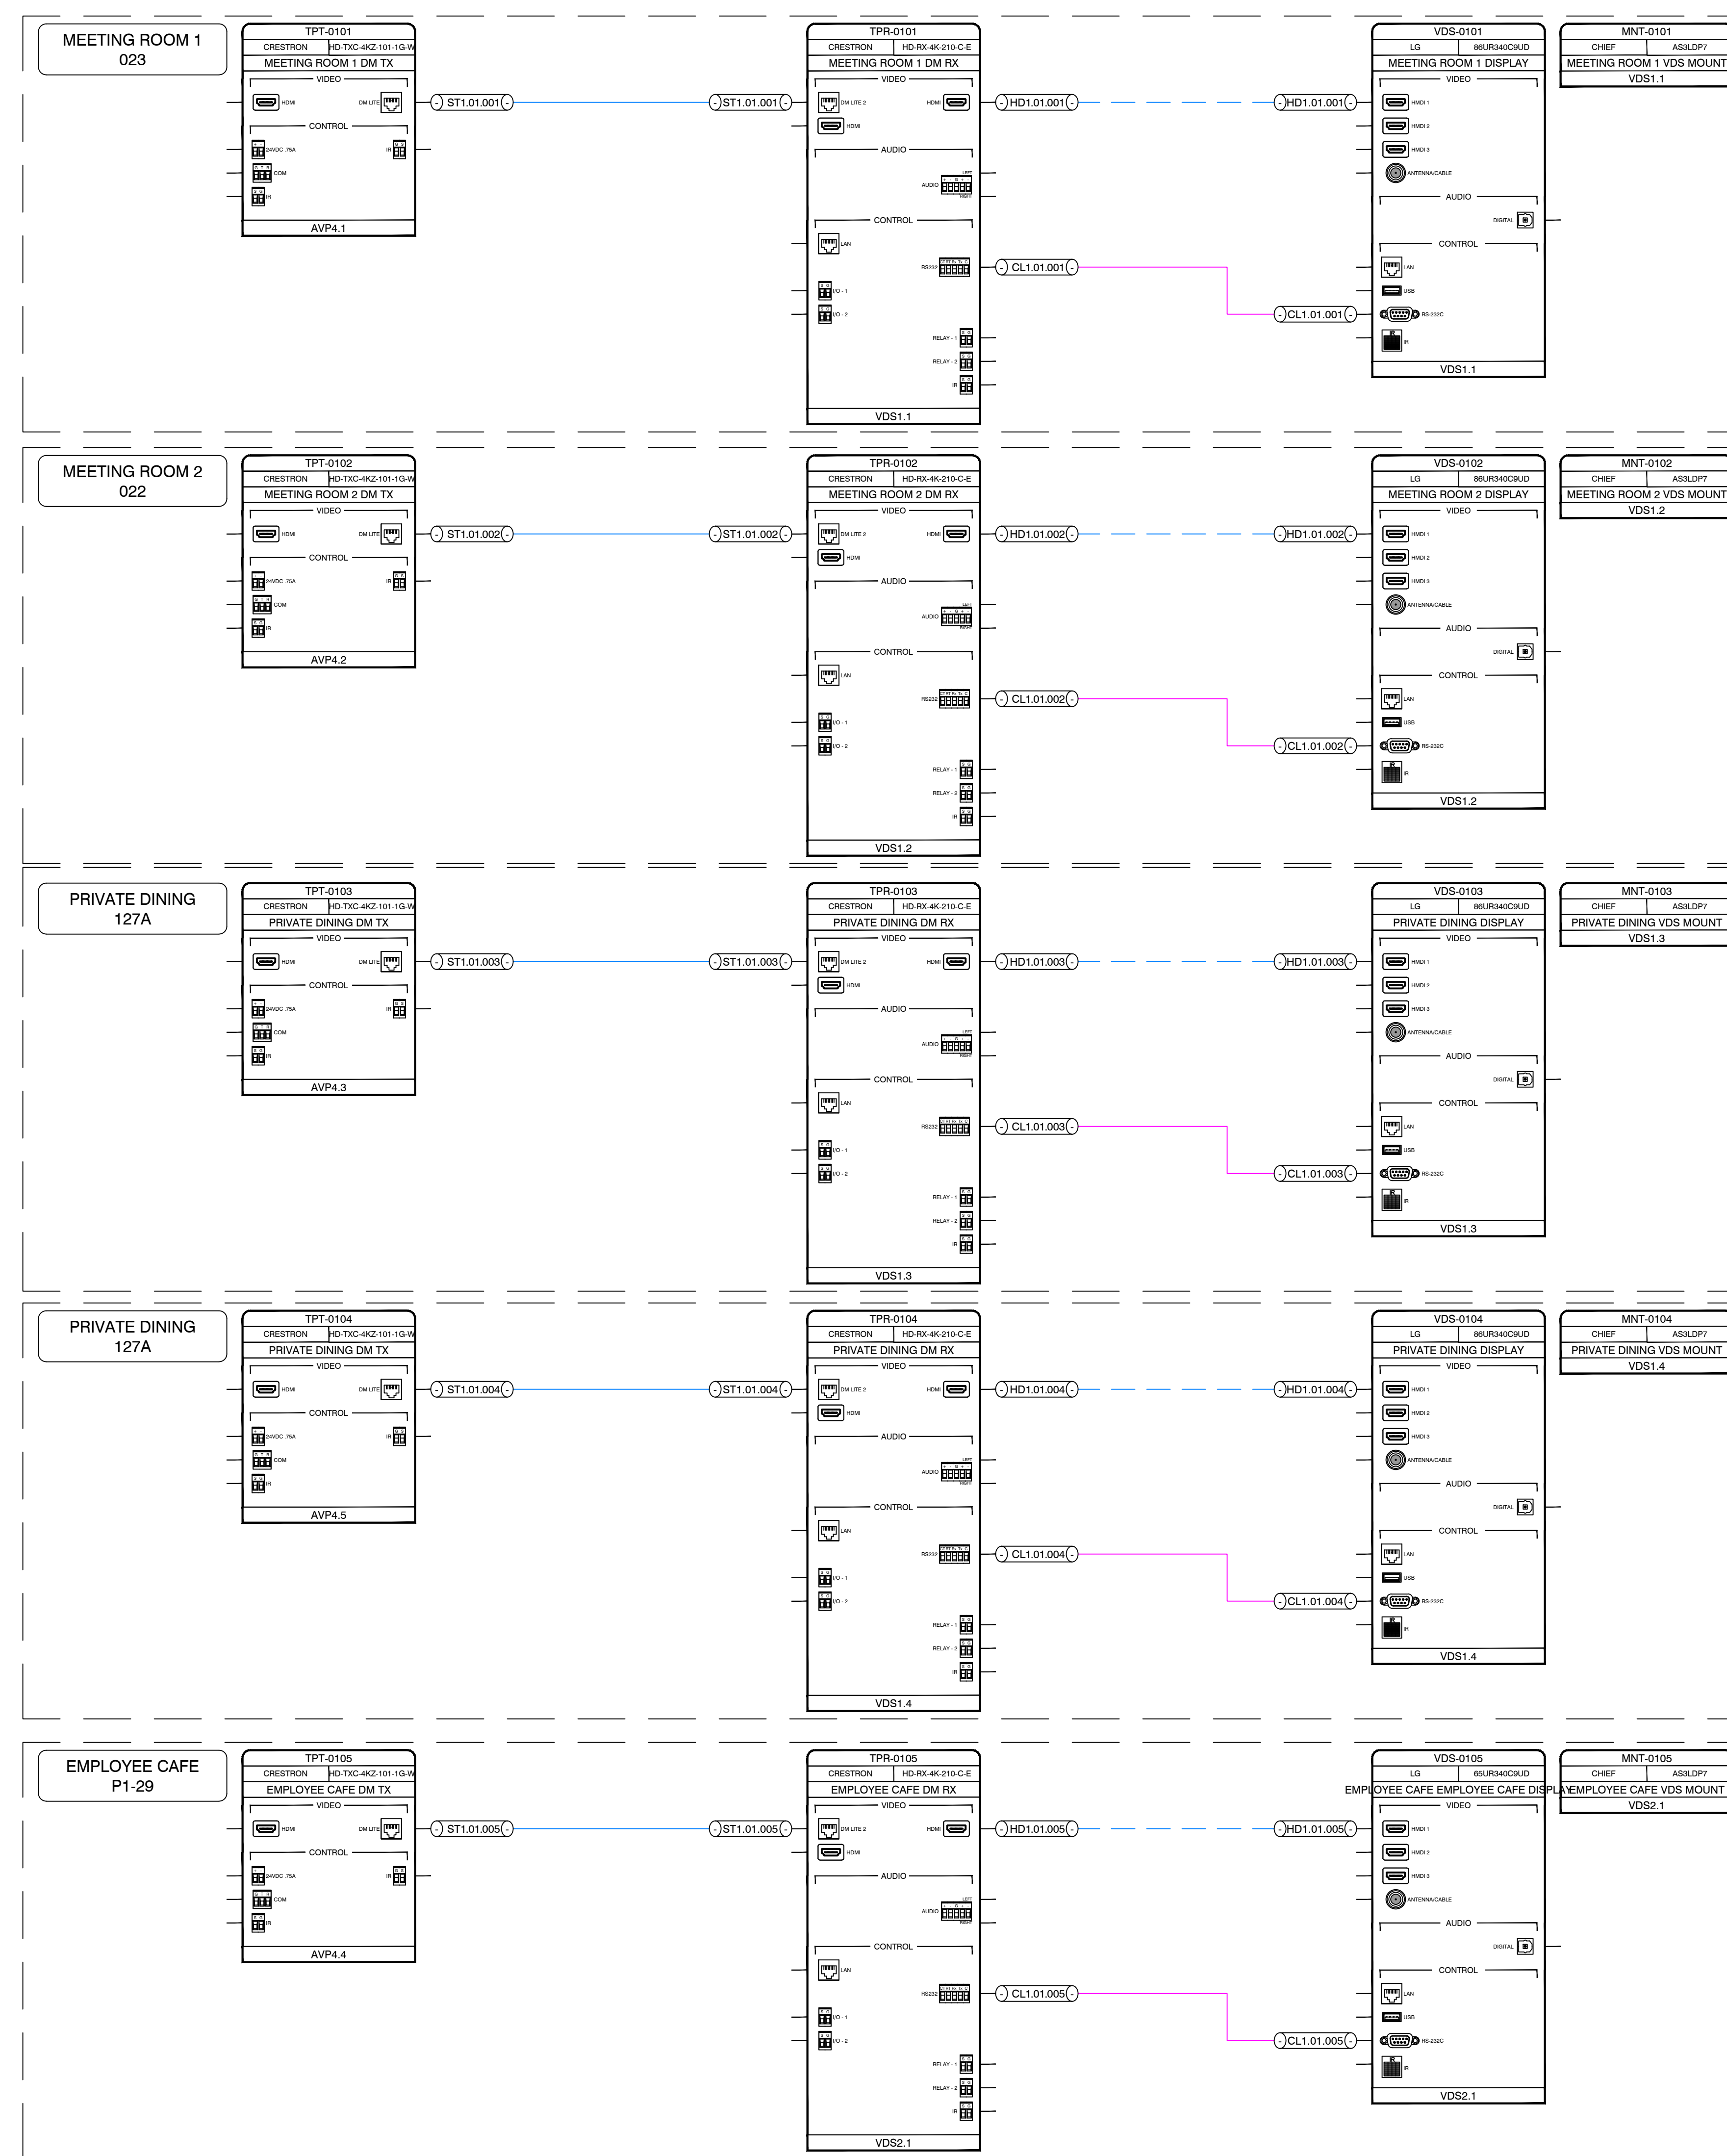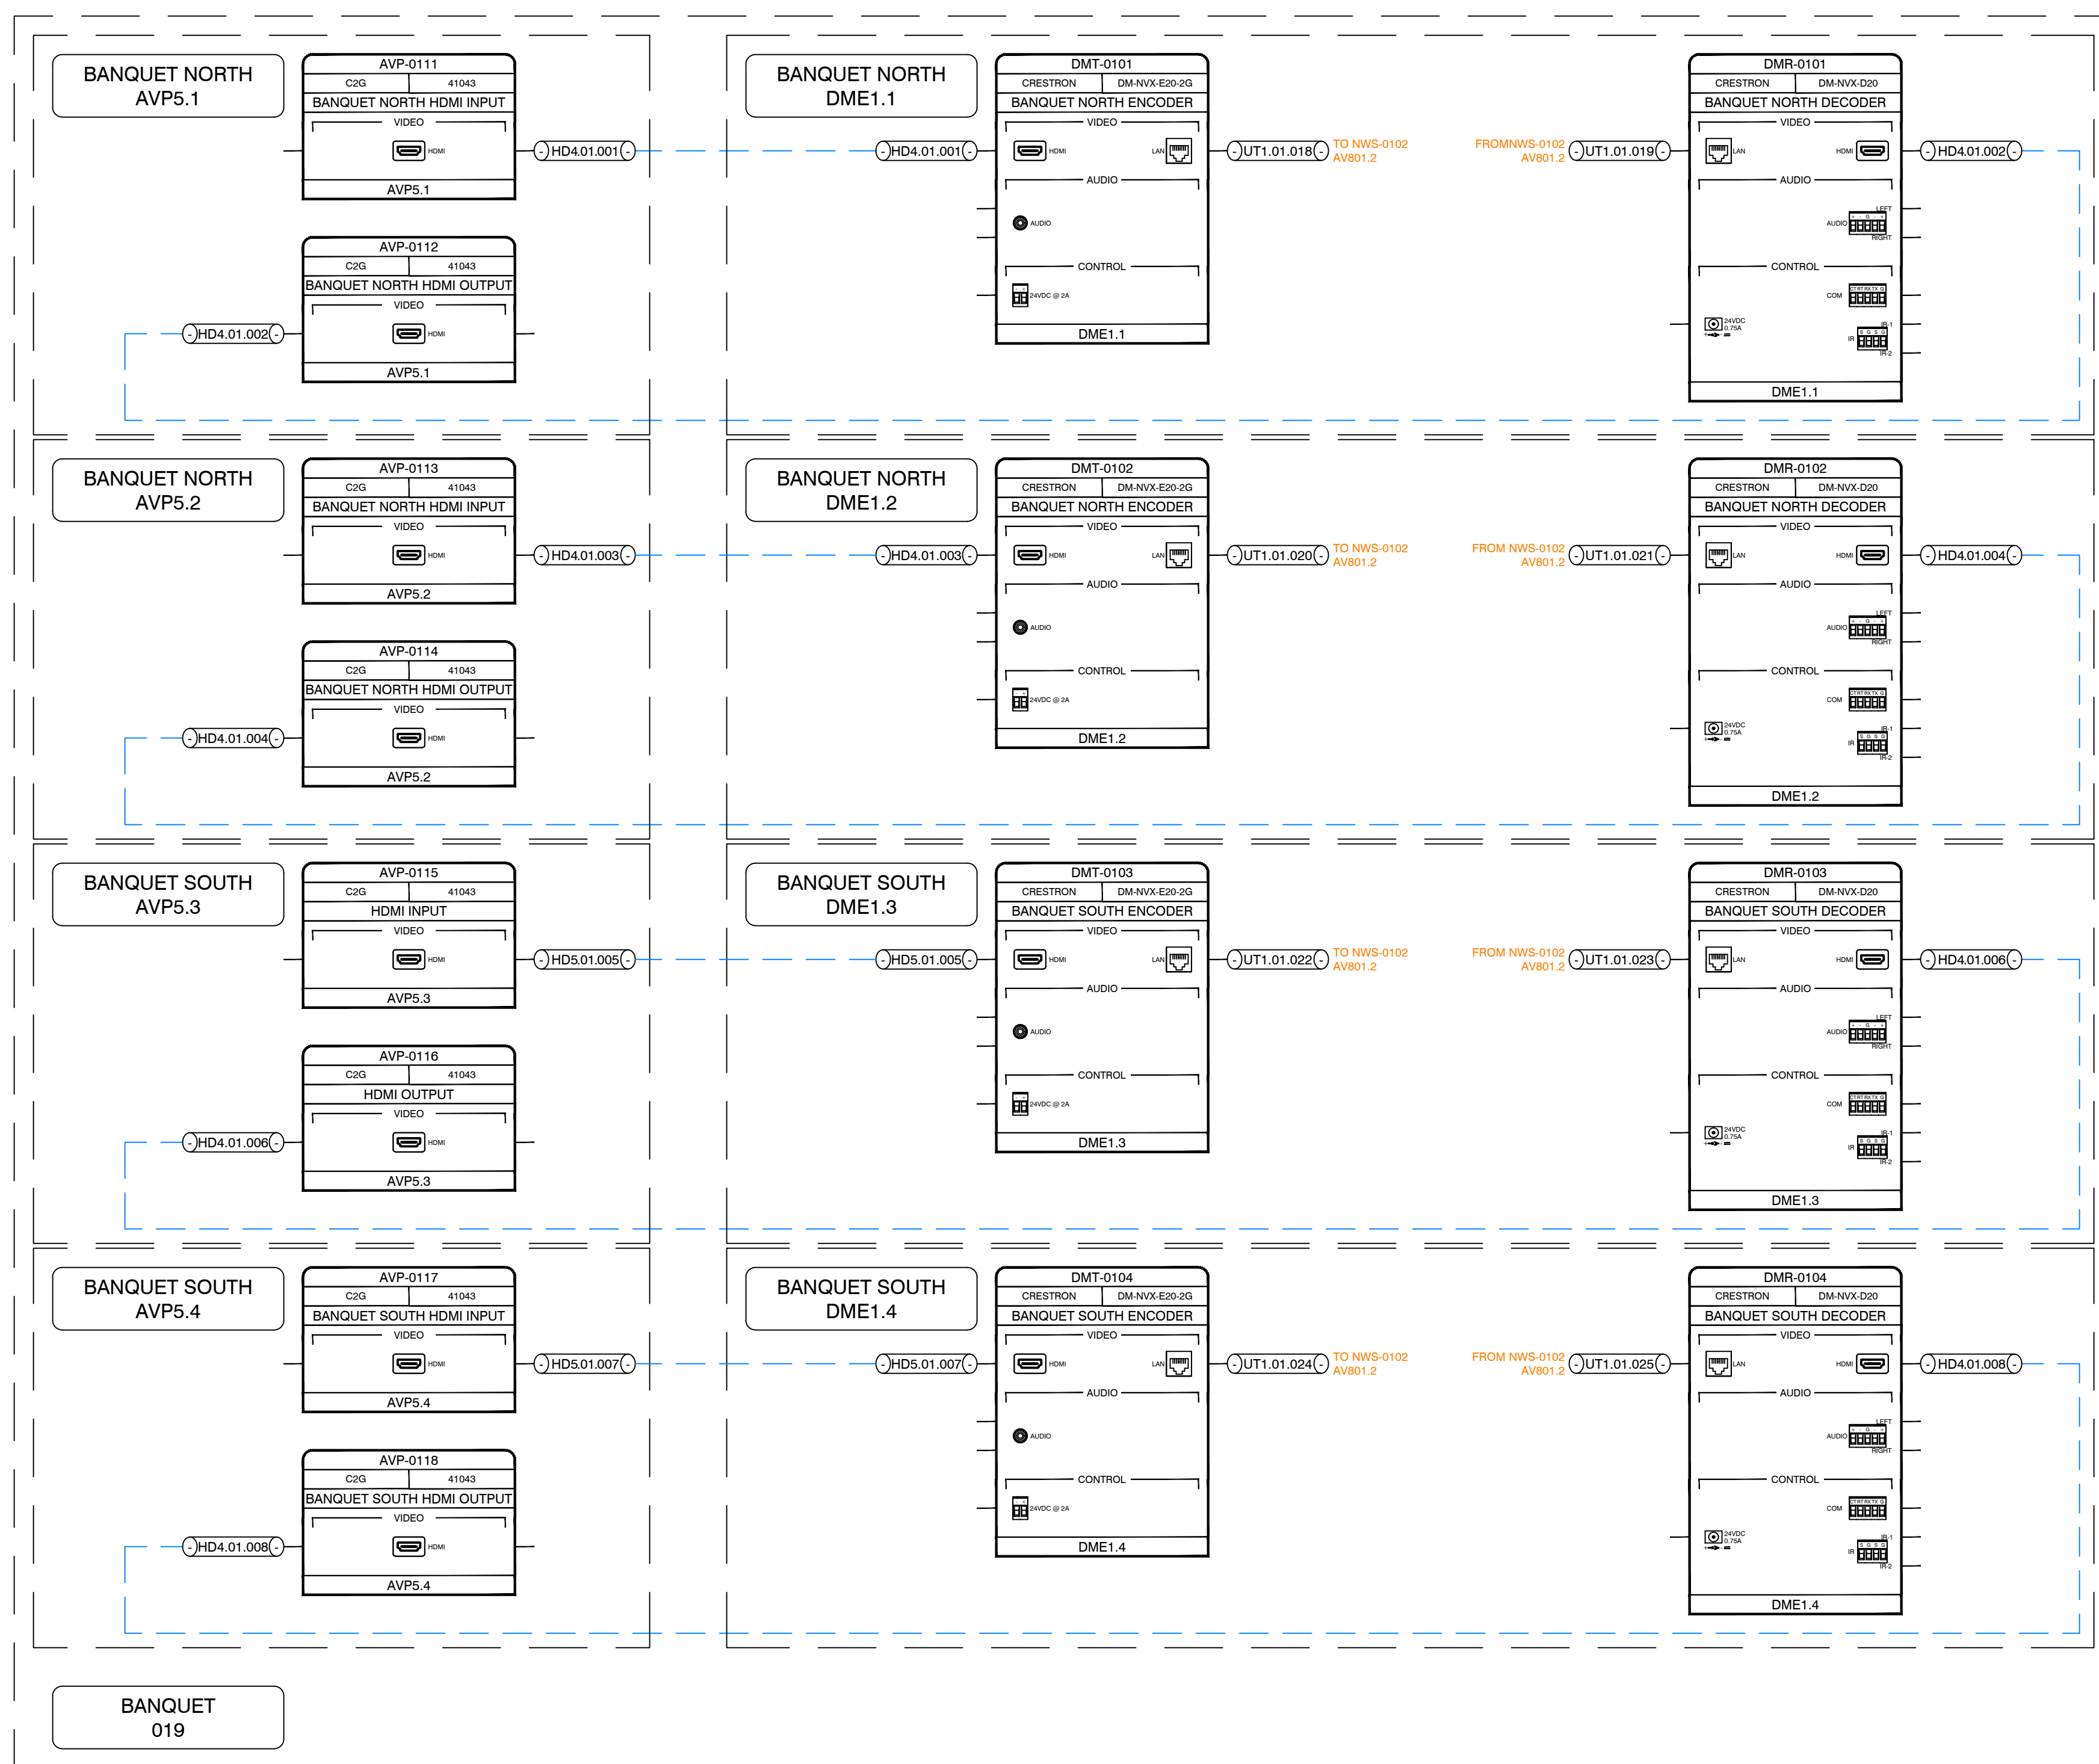[illegible]

NUM		NOTES	LINE DESIGNATIONS KEY	
①	-			BULK - AUDIO
②	-			PATCH - AUDIO
③	-			BULK - VIDEO
④	-			PATCH - VIDEO
⑤	-			BULK - CONTROL
⑥	-			PATCH - CONTROL
⑥	-			BULK - GENERIC
⑦	-			PATCH - GENERIC

