

# APPELLATION SUN VALLEY AUDIO VIDEO INTEGRATION

# AUDIOVISUAL SHOP DRAWINGS

MARSHALL INDUSTRIES • 1303 NORTH 39TH STREET, NAMPA, ID • 208.442.7222



www.marshallind.com

## PROJECT INFORMATION

853

APPELLATION SUN VALLEY  
AUDIO VIDEO INTEGRATION

|                                                      |                            |
|------------------------------------------------------|----------------------------|
| CUSTOMER NAME:<br>HARRIMAN SUN VALLEY HOTEL          | CUSTOMER NUMBER:<br>APH001 |
| SITE NAME:<br>HARRIMAN SUN VALLEY HOTEL              | SITE NUMBER:<br>72338311   |
| SITE ADDRESS:<br>300 E RIVER ST<br>KETCHUM, ID 83353 |                            |

|                                        |                                           |
|----------------------------------------|-------------------------------------------|
| SALES PERSON:<br><b>JEREMY WADDELL</b> | ENGINEERED BY:<br><b>ADAM HANDY</b>       |
| DRAFTER:<br><b>ELI ANDERSON</b>        | PROJECT MANAGER:<br><b>JEREMY WADDELL</b> |

### DRAWING SET INFORMATION

|               |                                          |
|---------------|------------------------------------------|
| PHASE:        | CONSTRUCTION                             |
| PUBLISH DATE: | 5/18/2026                                |
| PLOT SIZE:    | ARCH FULL BLEED E (36.00 X 48.00 INCHES) |
| PLOT SCALE:   | 1' = 1'-0"                               |
| APPROVED BY:  |                                          |

### SHEET REVISION INFORMATION

|          |                       |
|----------|-----------------------|
| REVISION | REVISION DATE:        |
| *****    | REVISION DESCRIPTION: |

#### REVISION & ISSUE HISTORY

[illegible]

# TABLE OF CONTENTS

| REV                            | DRAWING NUMBER | TITLE               | DESCRIPTION               | APP BY |
|--------------------------------|----------------|---------------------|---------------------------|--------|
| AV000 - GENERAL DRAWINGS       |                |                     |                           |        |
|                                | AV000          | TABLE OF CONTENTS   |                           |        |
|                                | AV001          | AV LEGENDS AND KEYS | ROUGH-IN                  |        |
|                                | AV002          | AV LEGENDS AND KEYS | STRUCTURED CABLING        |        |
| AV100 - WIREPATH AND BACKBOXES |                |                     |                           |        |
|                                | AV101          | LEVEL P1            |                           |        |
|                                | AV102          | LEVEL 1             |                           |        |
|                                | AV103          | LEVEL 2             |                           |        |
| AV200 - REFLECTED CEILING      |                |                     |                           |        |
|                                | AV201          | LEVEL P1            |                           |        |
|                                | AV202          | LEVEL 1             |                           |        |
|                                | AV203          | LEVEL 2             |                           |        |
| AV700 - PLATE DETAILS          |                |                     |                           |        |
|                                | AV701          | UTILIZED PLATES     |                           |        |
| AV800 - SINGLE LINE DIAGRAMS   |                |                     |                           |        |
|                                | AV801.1        | RESORT AV           | LEVEL P1 RACK - SPA       |        |
|                                | AV801.2        | RESORT AV           | LEVEL 1 RACK - BANQUET    |        |
|                                | AV801.3        | RESORT AV           | LEVEL 2 RACK - RESTAURANT |        |
|                                | AV801.4        | RESORT AV           | VIDEO SYSTEM FUNCTIONAL   |        |
| AV900 - ENCLOSURE ELEVATIONS   |                |                     |                           |        |
|                                | AV901          | UTILIZED RACKS      |                           |        |

APPELLATION SUN VALLEY

GENERAL DRAWINGS

TABLE OF CONTENTS

AV000

FILE NAME: AV000.DWG





| ENCLOSURE LEGEND            |  |                                                       |  |                   |  |                     |    |                  |    |     |    |  |  |  |
|-----------------------------|--|-------------------------------------------------------|--|-------------------|--|---------------------|----|------------------|----|-----|----|--|--|--|
| SYM                         |  | DESCRIPTION                                           |  | ELEVATION         |  | QTY                 |    |                  |    |     |    |  |  |  |
| COMMONLY USED WALL BOXES    |  |                                                       |  |                   |  | 1G                  | 2G | 3G               | 4G | 5G  | 6G |  |  |  |
| C#                          |  | GENERIC 3" DEEP BACKBOX.<br>REFER TO # FOR GANG SIZE. |  | COUNTER HEIGHT    |  | 0                   | 0  | 0                | 0  | 0   | 0  |  |  |  |
| R#                          |  |                                                       |  | RECEPTACLE HEIGHT |  | 3                   | 4  | 0                | 0  | 0   | 0  |  |  |  |
| S#                          |  |                                                       |  | SWITCH HEIGHT     |  | 0                   | 4  | 16               | 0  | 0   | 0  |  |  |  |
| SYM                         |  | TYPE                                                  |  | GANG              |  | DESCRIPTION         |    | ELEVATION        |    | QTY |    |  |  |  |
| PROJECT SPECIFIC WALL BOXES |  |                                                       |  |                   |  |                     |    |                  |    |     |    |  |  |  |
| A                           |  |                                                       |  | 1                 |  | 3" DEEP BACKBOX     |    | FIELD DETERMINED |    | 5   |    |  |  |  |
| B                           |  |                                                       |  | 1                 |  | 3" DEEP BACKBOX     |    | +11' AFF         |    | 4   |    |  |  |  |
| D                           |  |                                                       |  | 1                 |  | SPEAKER LOCATION    |    | FIELD DETERMINED |    | 6   |    |  |  |  |
| E                           |  |                                                       |  | 1                 |  | LANDSCAPE SPEAKER   |    | FIELD DETERMINED |    | 9   |    |  |  |  |
| F                           |  |                                                       |  | 1                 |  | LANDSCAPE SUBWOOFER |    | FIELD DETERMINED |    | 1   |    |  |  |  |
| G                           |  | CHIEF PAC526FWP2                                      |  |                   |  | DISPLAY LOCATION    |    | 60" AFF          |    | 3   |    |  |  |  |
| H                           |  |                                                       |  |                   |  |                     |    |                  |    |     |    |  |  |  |
| I                           |  |                                                       |  |                   |  |                     |    |                  |    |     |    |  |  |  |
| SYM           |  | TYPE              |  | GANG |  | DESCRIPTION                |  | ELEVATION        |  | QTY |  |
|---------------|--|-------------------|--|------|--|----------------------------|--|------------------|--|-----|--|
| CEILING BOXES |  |                   |  |      |  |                            |  |                  |  |     |  |
| A             |  | SONANCE PS-C63RTL |  | 0    |  | 6" SELF ENCLOSED SPEAKER   |  | FLUSH IN CEILING |  | 100 |  |
| B             |  | SONANCE PS-C83RWT |  | 0    |  | 8" SELF ENCLOSED SUBWOOFER |  | FLUSH IN CEILING |  | 6   |  |
| C             |  |                   |  |      |  |                            |  |                  |  |     |  |
| D             |  |                   |  |      |  |                            |  |                  |  |     |  |
| E             |  |                   |  |      |  |                            |  |                  |  |     |  |
| F             |  |                   |  |      |  |                            |  |                  |  |     |  |
| G             |  |                   |  |      |  |                            |  |                  |  |     |  |
| H             |  |                   |  |      |  |                            |  |                  |  |     |  |
| I             |  |                   |  |      |  |                            |  |                  |  |     |  |
| J             |  |                   |  |      |  |                            |  |                  |  |     |  |
| K             |  |                   |  |      |  |                            |  |                  |  |     |  |
| L             |  |                   |  |      |  |                            |  |                  |  |     |  |
| M             |  |                   |  |      |  |                            |  |                  |  |     |  |

| TABLE BOXES |  |  |  |  |  |  |  |  |  |  |  |
|-------------|--|--|--|--|--|--|--|--|--|--|--|
| A           |  |  |  |  |  |  |  |  |  |  |  |
| B           |  |  |  |  |  |  |  |  |  |  |  |
| C           |  |  |  |  |  |  |  |  |  |  |  |
| D           |  |  |  |  |  |  |  |  |  |  |  |
| E           |  |  |  |  |  |  |  |  |  |  |  |
| F           |  |  |  |  |  |  |  |  |  |  |  |
| G           |  |  |  |  |  |  |  |  |  |  |  |
| H           |  |  |  |  |  |  |  |  |  |  |  |
| I           |  |  |  |  |  |  |  |  |  |  |  |
| J           |  |  |  |  |  |  |  |  |  |  |  |
| K           |  |  |  |  |  |  |  |  |  |  |  |
| L           |  |  |  |  |  |  |  |  |  |  |  |

| SYM         |  | TYPE |  | GANG |  | DESCRIPTION |  | ELEVATION    |  | QTY |  |
|-------------|--|------|--|------|--|-------------|--|--------------|--|-----|--|
| FLOOR BOXES |  |      |  |      |  |             |  |              |  |     |  |
| A           |  |      |  | 1    |  |             |  | FINISH FLOOR |  | 0   |  |
| B           |  |      |  |      |  |             |  |              |  |     |  |
| C           |  |      |  |      |  |             |  |              |  |     |  |
| D           |  |      |  |      |  |             |  |              |  |     |  |
| E           |  |      |  |      |  |             |  |              |  |     |  |
| F           |  |      |  |      |  |             |  |              |  |     |  |
| G           |  |      |  |      |  |             |  |              |  |     |  |
| H           |  |      |  |      |  |             |  |              |  |     |  |
| I           |  |      |  |      |  |             |  |              |  |     |  |
| J           |  |      |  |      |  |             |  |              |  |     |  |
| K           |  |      |  |      |  |             |  |              |  |     |  |
| L           |  |      |  |      |  |             |  |              |  |     |  |
| M           |  |      |  |      |  |             |  |              |  |     |  |

| EQUIPMENT RACKS |  |                             |  |   |  |                     |  |  |  |   |  |
|-----------------|--|-----------------------------|--|---|--|---------------------|--|--|--|---|--|
| A               |  | MIDDLE ATLANTIC CWR-26-26VD |  | 0 |  | 26RU EQUIPMNET RACK |  |  |  | 3 |  |
| B               |  |                             |  |   |  |                     |  |  |  |   |  |
| C               |  |                             |  |   |  |                     |  |  |  |   |  |
| D               |  |                             |  |   |  |                     |  |  |  |   |  |
| E               |  |                             |  |   |  |                     |  |  |  |   |  |
| F               |  |                             |  |   |  |                     |  |  |  |   |  |
| G               |  |                             |  |   |  |                     |  |  |  |   |  |
| H               |  |                             |  |   |  |                     |  |  |  |   |  |
| I               |  |                             |  |   |  |                     |  |  |  |   |  |
| J               |  |                             |  |   |  |                     |  |  |  |   |  |
| K               |  |                             |  |   |  |                     |  |  |  |   |  |
| L               |  |                             |  |   |  |                     |  |  |  |   |  |

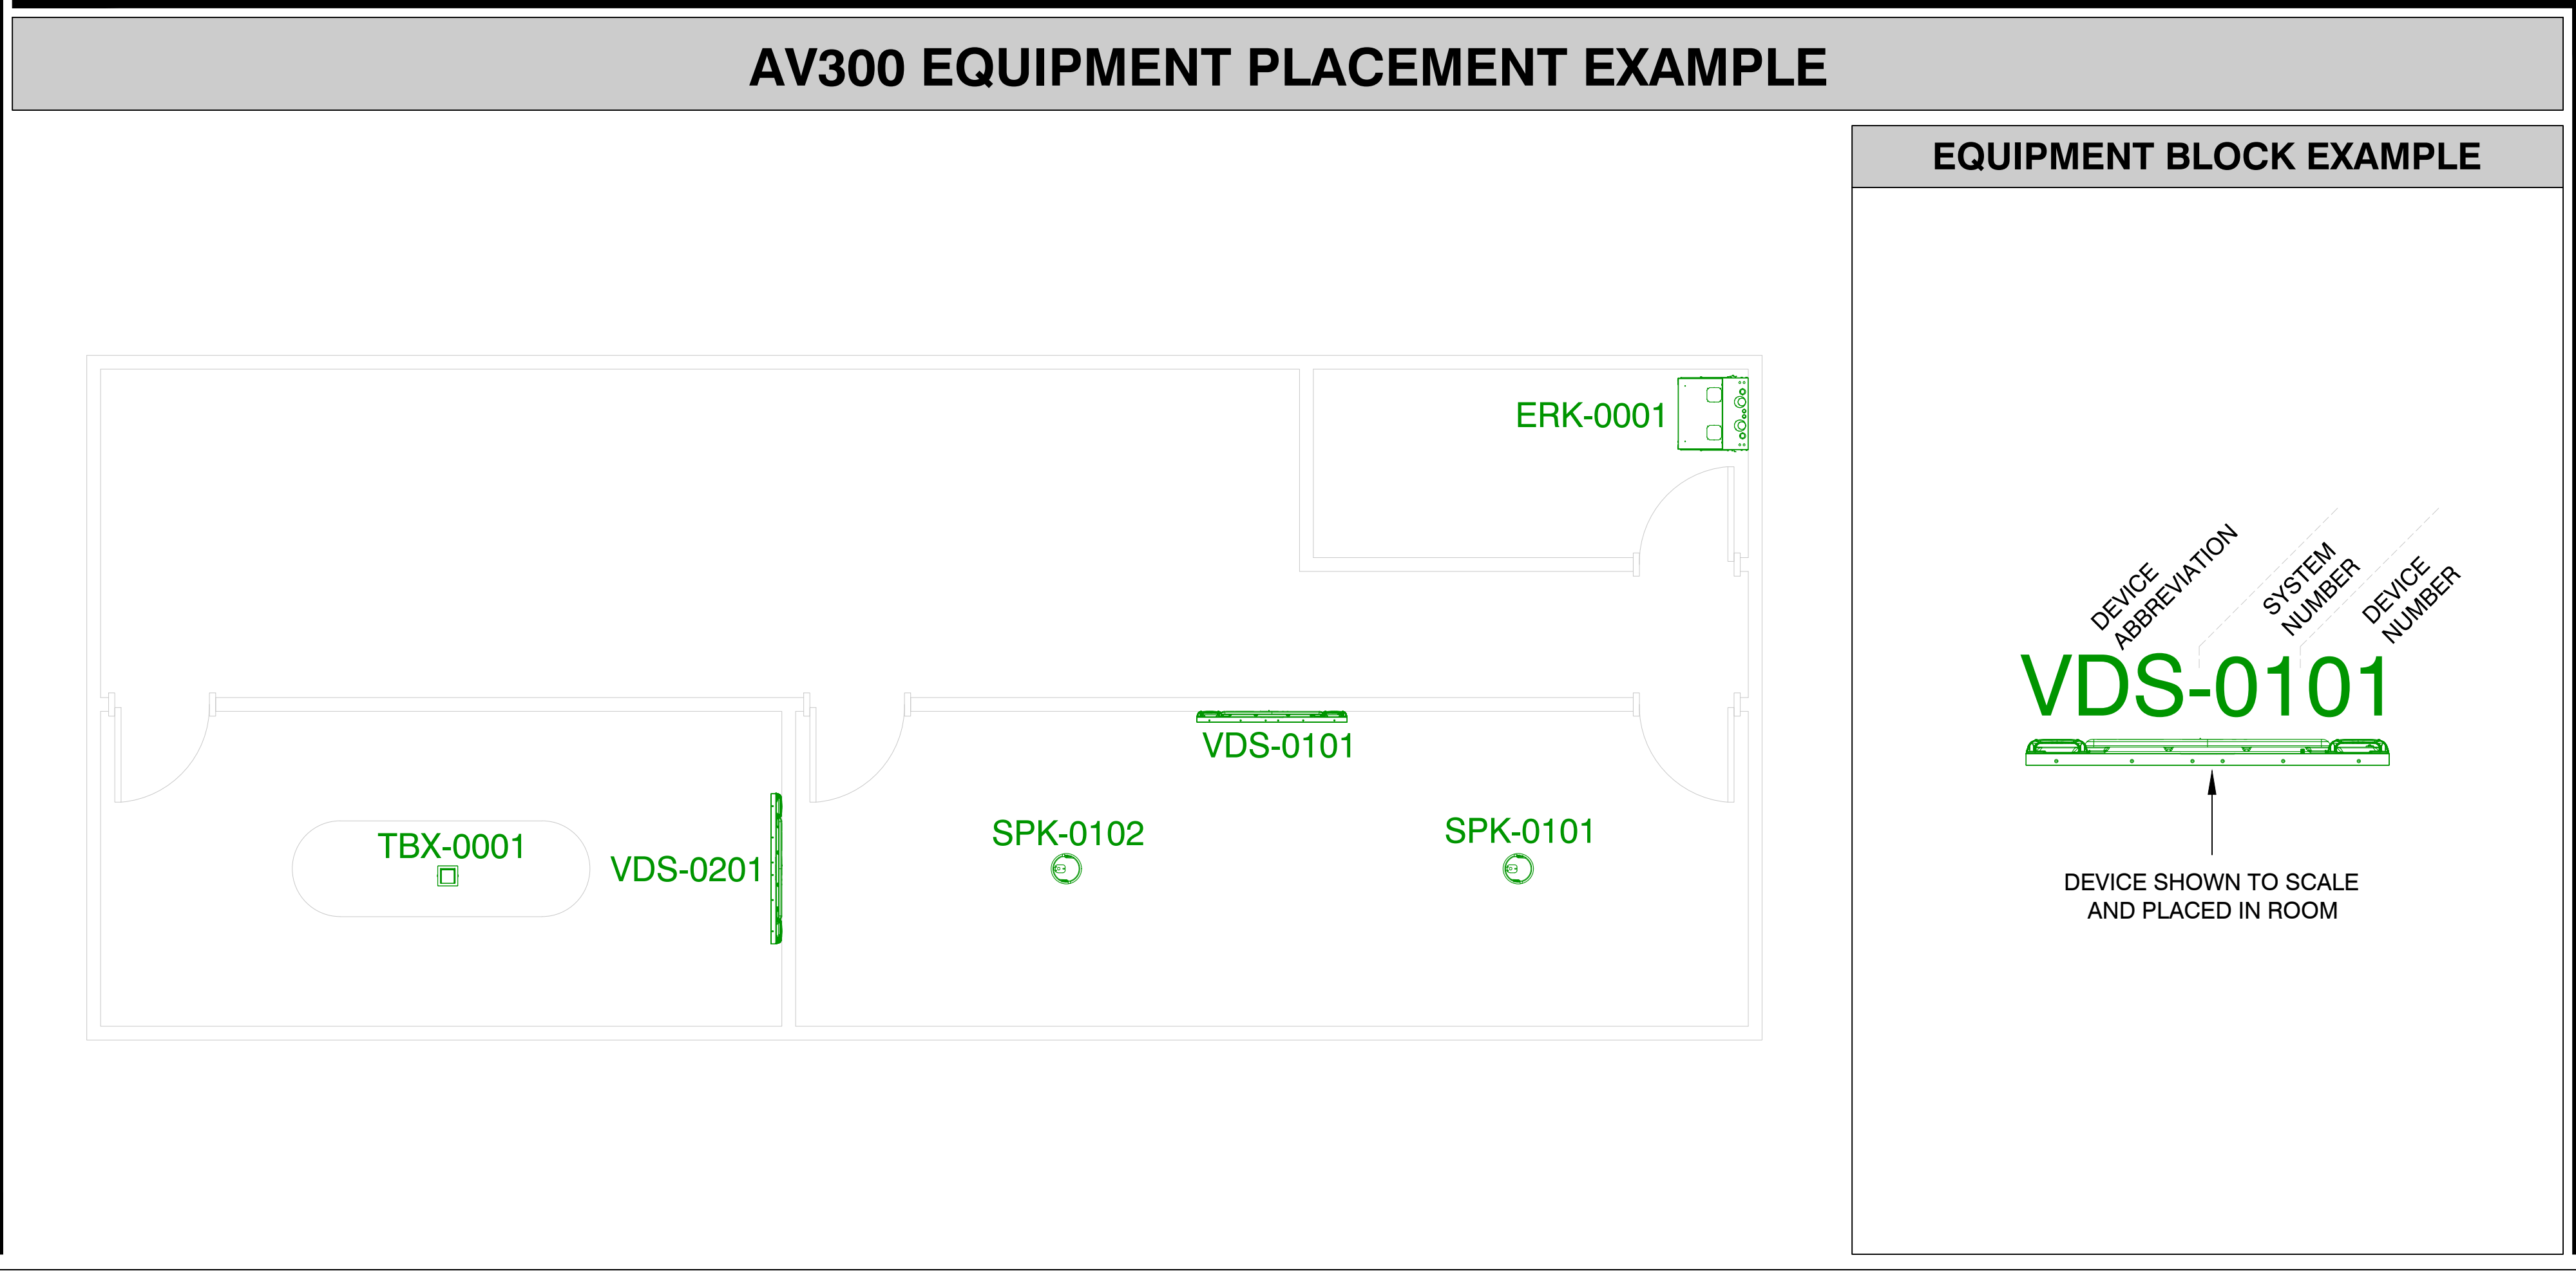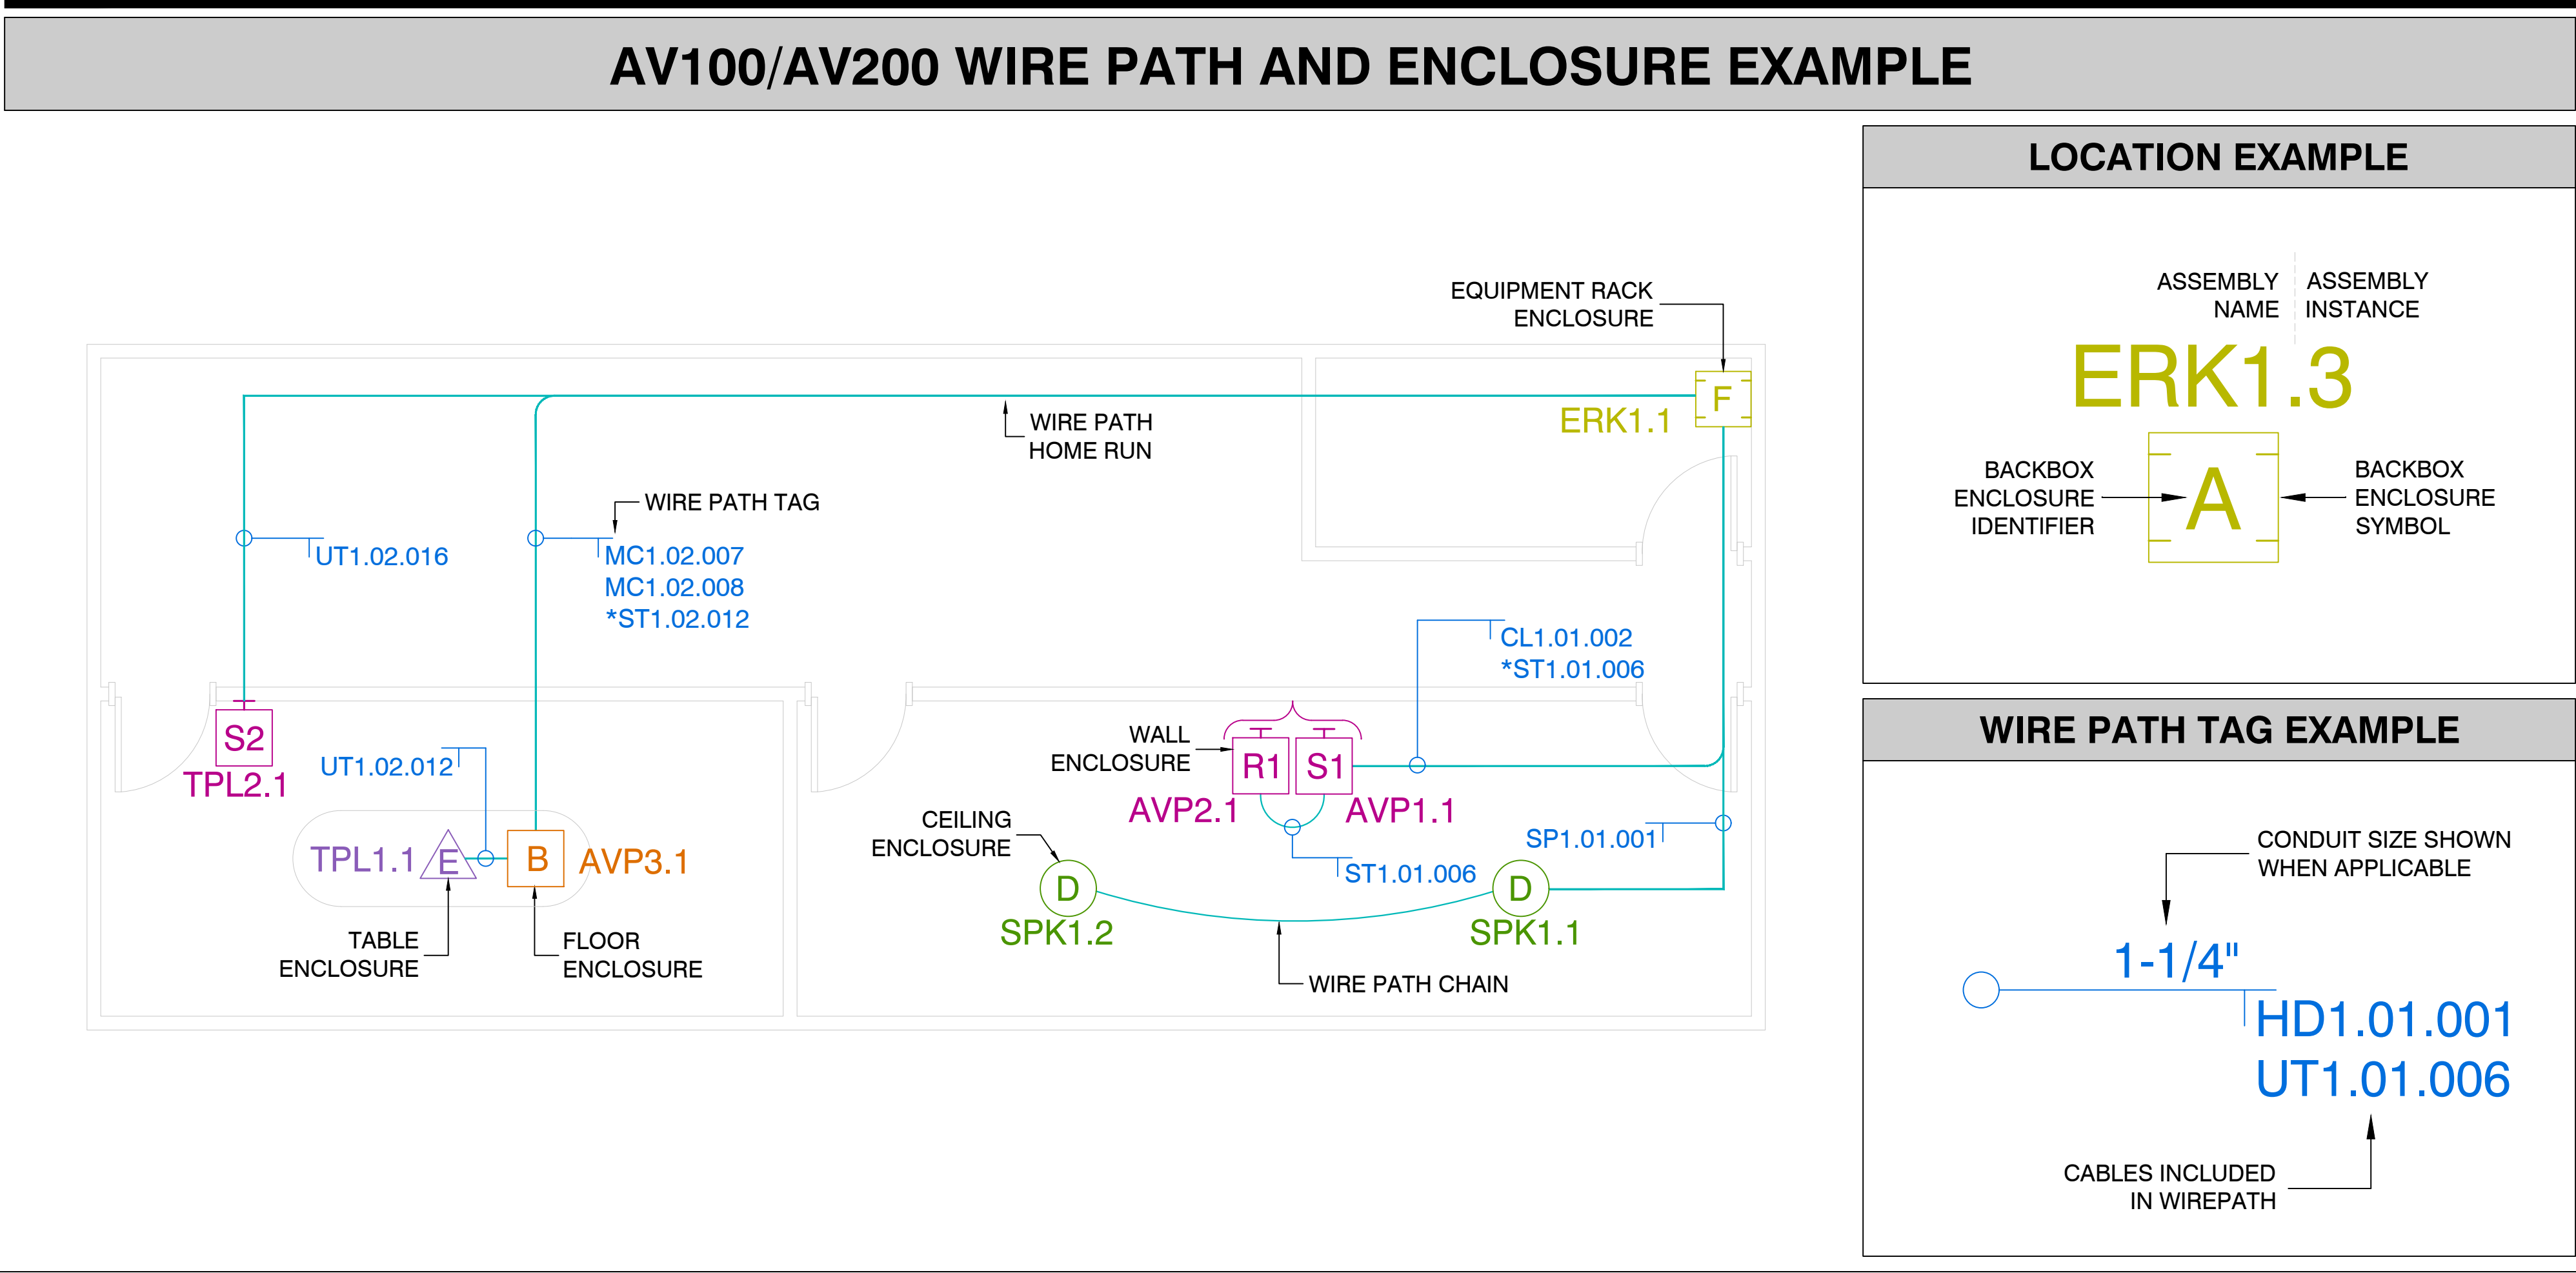



| ABRV. | DESCRIPTION                |
|-------|----------------------------|
| AAP   | AMPLIFIED AUDIO PANEL      |
| ACP   | AUDIO CONTROL PLATE        |
| ACU   | ACOUSTIC MATERIAL          |
| ADC   | AUDIO CONFERENCING         |
| ALS   | ASSISTED LISTENING SYSTEM  |
| AMP   | AMPLIFIER                  |
| AMS   | ASSET MANAGEMENT           |
| ANN   | ANNOTATOR                  |
| ANT   | ANTENNA                    |
| ARS   | AUDIO RESPONSE SYSTEM      |
| ASP   | AUDIO SIGNAL PROCESSOR     |
| AVF   | AUDIO/VIDEO FURNITURE      |
| AVL   | AUDIO/VIDEO LIFT           |
| AVP   | AUDIO/VIDEO PANEL          |
| AVT   | AUDIO/VIDEO PANEL          |
| BAG   | EQUIPMENT BAG              |
| BGM   | BACKGROUND MUSIC SYSTEM    |
| BOB   | BREAK OUT BOX              |
| CAM   | CAMERA                     |
| CBX   | CEILING BOX                |
| CCU   | CAMERA CONTROL UNIT        |
| CLK   | CLOCK                      |
| CNT   | CONTROLLER                 |
| CNV   | CONVERTER                  |
| COD   | ENCODER/DECODER            |
| CPU   | COMPUTER                   |
| CRD   | CARD/MODULE/INSERT         |
| DAR   | DIGITAL AUDIO RECORDER     |
| DMP   | DIGITAL MEDIA PLAYER       |
| DMR   | DIGITAL MEDIA RECORDER     |
| DMT   | DIGITAL MEDIA TRANSMISSION |
| DOC   | DOCUMENT CAMERA            |
| DSP   | DIGITAL SIGNAGE SYSTEM     |
| DTP   | DISTANCE TRANSPORT         |
| DVR   | DIGITAL VIDEO RECORDER     |
| DWR   | DRAWER                     |
| EFX   | EFFECTS PROCESSOR          |
| EMI   | IR/RF EMITTER              |
| ENC   | CHASSIS/CARD ENCLOSURE     |
| ERK   | EQUIPMENT RACK             |
| FAN   | FAN                        |
| FBX   | FLOOR BOX                  |
| GUI   | GRAPHICAL USER INTERFACE   |
| ICS   | INTERCOM SYSTEM            |
| IFB   | INTERUPTED FOLDBACK        |
| INT   | INTERFACE                  |
| IWB   | WHITE BOARD                |
| KPD   | KEYPAD CONTROL             |
| LEN   | LENS                       |
| LGT   | LIGHTING SYSTEM            |
| MDI   | MIDI CONTROLLER            |
| MIC   | MICROPHONE                 |
| MIX   | MIXER                      |
| MOD   | MODULATOR/DEMODULATOR      |
| MON   | MONITOR                    |
| MSG   | MESSAGING SYSTEMS          |
| MSK   | SOUND MASKING SYSTEM       |
| MTR   | MAGNETIC TAPE RECORDER     |
| NCS   | NURSE CALL SYSTEM          |
| NMD   | NETWORK MEDIA DEVICE       |
| NVR   | NETWORK VIDEO RECORDER     |
| NWD   | NETWORK DEVICE             |
| ODR   | OPTICAL DISK RECORDER      |
| PAS   | PUBLIC ADDRESS SYSTEM      |

[illegible]

| CABLE LEGEND                   |           |                    |                     |        |
|--------------------------------|-----------|--------------------|---------------------|--------|
| ID                             | MAKE      | MODEL              | DESCRIPTION         | PLENUM |
| CONTROL                        |           |                    |                     |        |
| CL1                            | WEST PENN | 25510BGY           | CONTROL CABLE       |        |
| CL2                            |           |                    |                     |        |
| CL3                            |           |                    |                     |        |
| CL4                            |           |                    |                     |        |
| CL5                            |           |                    |                     |        |
| COAX                           |           |                    |                     |        |
| CX1                            | WEST PENN | 2584BK             | ANTENNA CABLE       |        |
| CX2                            |           |                    |                     |        |
| CX3                            |           |                    |                     |        |
| CX4                            |           |                    |                     |        |
| CX5                            |           |                    |                     |        |
| FIBER OPTIC                    |           |                    |                     |        |
| FB1                            |           |                    |                     |        |
| FB2                            |           |                    |                     |        |
| FB3                            |           |                    |                     |        |
| FB4                            |           |                    |                     |        |
| HDMI                           |           |                    |                     |        |
| HD1                            |           |                    | 3' HDMI CABLE       |        |
| HD2                            |           |                    | 6' HDMI CABLE       |        |
| HD3                            |           |                    | 10' HDMI CABLE      |        |
| HD4                            |           |                    | 15' HDMI CABLE      |        |
| HD5                            |           |                    | 30' HDMI CABLE      |        |
| HD6                            |           |                    |                     |        |
| HD7                            |           |                    |                     |        |
| HD8                            |           |                    |                     |        |
| MICROPHONE OR LINE LEVEL AUDIO |           |                    |                     |        |
| MC1                            | WEST PENN | 25291BBK           | MIC/LINE CABLE      |        |
| MC2                            |           |                    |                     |        |
| MC3                            |           |                    |                     |        |
| MC4                            |           |                    |                     |        |
| MC5                            |           |                    |                     |        |
| MULTI-FUNCTION                 |           |                    |                     |        |
| MF1                            |           |                    |                     |        |
| MF2                            |           |                    |                     |        |
| MF3                            |           |                    |                     |        |
| MF4                            |           |                    |                     |        |
| POWER                          |           |                    |                     |        |
| PW1                            |           |                    |                     |        |
| PW2                            |           |                    |                     |        |
| PW3                            |           |                    |                     |        |
| PW4                            |           |                    |                     |        |
| PW5                            |           |                    |                     |        |
| SPECIAL                        |           |                    |                     |        |
| SL1                            |           |                    |                     |        |
| SL2                            |           |                    |                     |        |
| SL3                            |           |                    |                     |        |
| SL4                            |           |                    |                     |        |
| SPEAKER                        |           |                    |                     |        |
| SP1                            | WEST PENN | 25225BGY           | 16AWG SPEAKER CABLE |        |
| SP2                            |           |                    |                     |        |
| SP3                            |           |                    |                     |        |
| SP4                            |           |                    |                     |        |
| SP5                            |           |                    |                     |        |
| SHIELDED TWISTED PAIR          |           |                    |                     |        |
| ST1                            | CRESTRON  | DM-CBL-8G-P-SP1000 | HDBASET CABLE       |        |
| ST2                            |           |                    |                     |        |
| ST3                            |           |                    |                     |        |
| ST4                            |           |                    |                     |        |
| ST5                            |           |                    |                     |        |
| USB                            |           |                    |                     |        |
| US1                            |           |                    |                     |        |
| US2                            |           |                    |                     |        |
| US3                            |           |                    |                     |        |
| US4                            |           |                    |                     |        |
| US5                            |           |                    |                     |        |
| UNSHIELDED TWISTED PAIR        |           |                    |                     |        |
| UT1                            | WEST PENN | 254246ABK          | DATA CABLE          |        |
| UT2                            |           |                    |                     |        |
| UT3                            |           |                    |                     |        |
| UT4                            |           |                    |                     |        |
| UT5                            |           |                    |                     |        |

[illegible]


APPELLATION SUN VALLEY

GENERAL DRAWINGS


AV LEGENDS AND KEYS

STRUCTURED CABLING

## AV800 SINGLE LINE DIAGRAM EXAMPLE

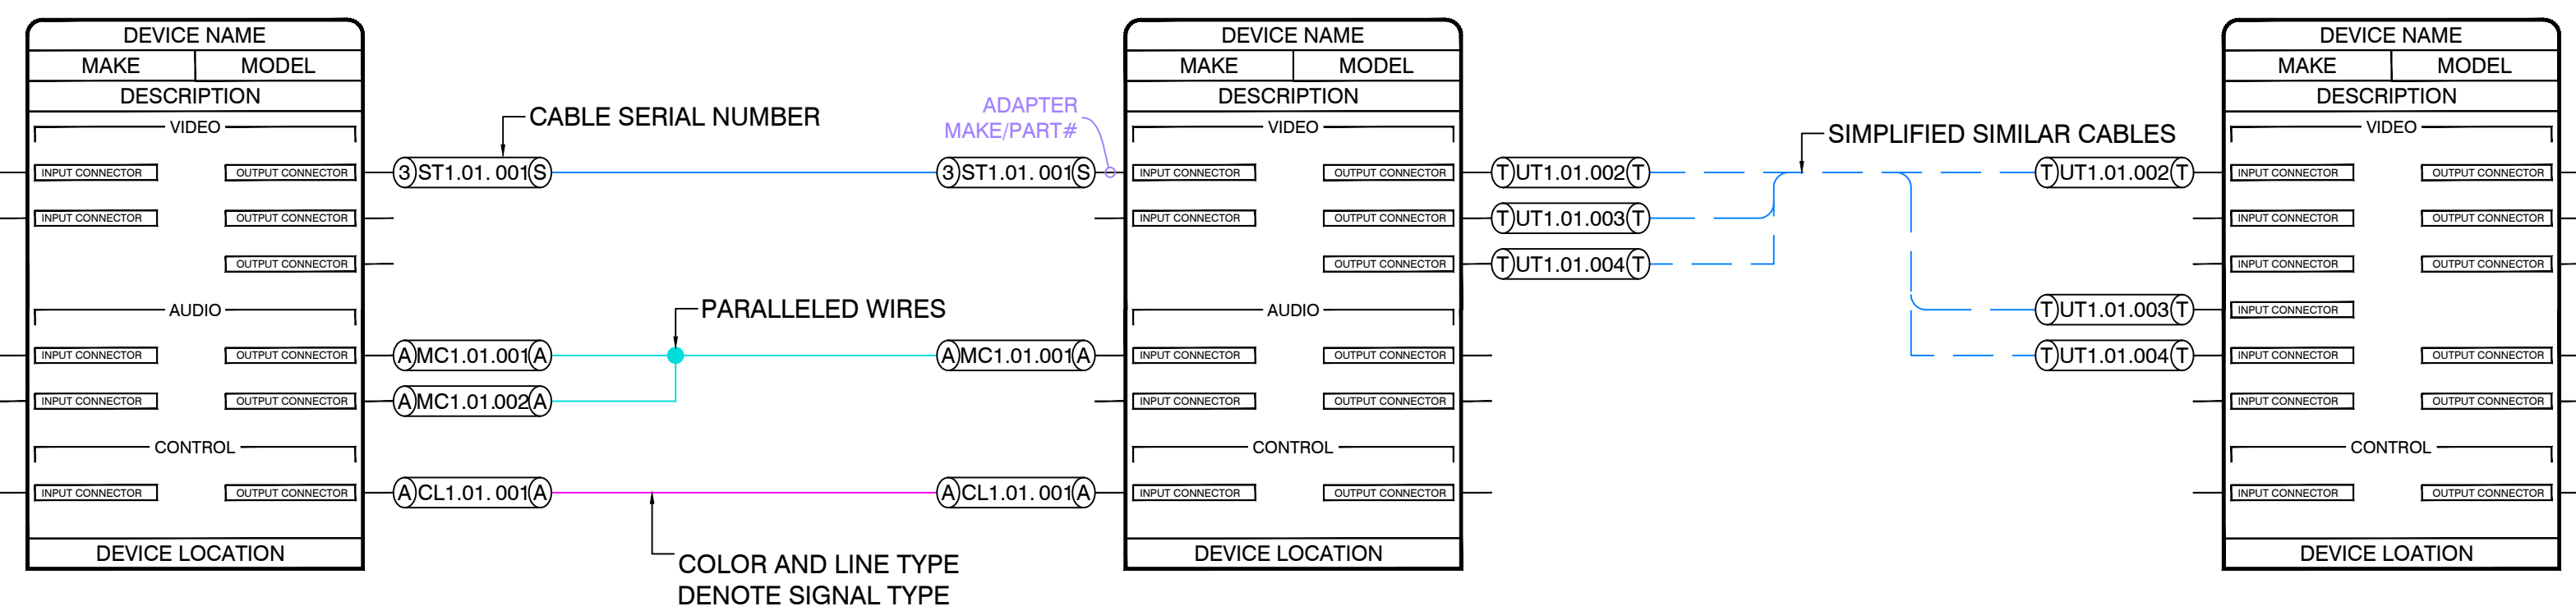

### AV800 CABLE SERIAL NUMBER EXAMPLE

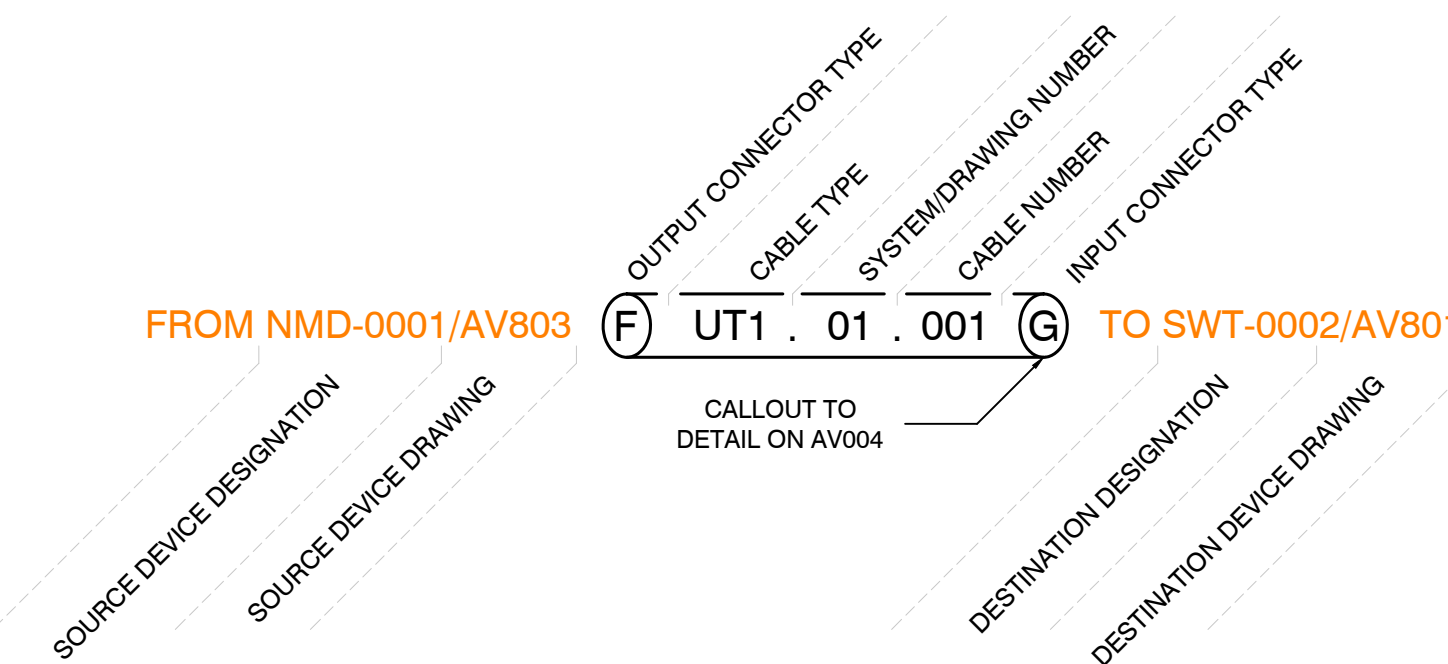

### LINE DESIGNATIONS KEY

- 
- | Category        | Count |
|-----------------|-------|
| BULK - AUDIO    | 10    |
| PATCH - AUDIO   | 9     |
| BULK - VIDEO    | 8     |
| PATCH - VIDEO   | 7     |
| BULK - CONTROL  | 6     |
| PATCH - CONTROL | 5     |
| BULK - GENERIC  | 4     |
| PATCH - GENERIC | 3     |

# AV002

FILE NAME: A:\000 DW



| SHEET CABLE LEGEND |           |                    |                     |     |
|--------------------|-----------|--------------------|---------------------|-----|
| ABBREV             | MAKE      | MODEL              | DESCRIPTION         | QTY |
| SP1                | WEST PENN | 25225BGY           | 16AWG SPEAKER CABLE | 1   |
| ST1                | CRESTRON  | DM-CBL-8G-P-SP1000 | HDBASET CABLE       | 1   |
| UT1                | WEST PENN | 254246ABK          | DATA CABLE          | 11  |

| SHEET ENCLOSURE LEGEND |          |      |                     |                   |       |        |
|------------------------|----------|------|---------------------|-------------------|-------|--------|
| LOCATION               | SYM      | GANG | DESCRIPTION         | ELEVATION         | SHEET | DETAIL |
| AVP4                   | [Symbol] | 1    | 3" DEEP BACKBOX     | RECEPTACLE HEIGHT | AV701 | 4      |
| AVP6                   | [Symbol] | 3    | 3" DEEP BACKBOX     | SWITCH HEIGHT     | AV701 | 6      |
| ERK1                   | [Symbol] | 0    | 26RU EQUIPMNET RACK |                   | AV901 | 1      |
| SPK6                   | [Symbol] | 1    | SPEAKER LOCATION    | FIELD DETERMINED  |       |        |
| TPL2                   | [Symbol] | 2    | 3" DEEP BACKBOX     | SWITCH HEIGHT     | AV701 | 2      |
| VDS2                   | [Symbol] | 1    | 3" DEEP BACKBOX     | FIELD DETERMINED  |       |        |



PROJECT INFORMATION

5853  
APPELLATION SUN VALLEY  
AUDIO VIDEO INTEGRATION

|                |                                     |                  |                |
|----------------|-------------------------------------|------------------|----------------|
| CUSTOMER NAME: | HARRIMAN SUN VALLEY HOTEL           | CUSTOMER NUMBER: | APH001         |
| SITE NAME:     | HARRIMAN SUN VALLEY HOTEL           | SITE NUMBER:     | 72338311       |
| SITE ADDRESS:  | 300 E RIVER ST<br>KETCHUM, ID 83353 |                  |                |
| SALES PERSON:  | JEREMY WADDELL                      | ENGINEERED BY:   | ADAM HANDY     |
| DRAWN:         | EU ANDERSON                         | PROJECT MANAGER: | JEREMY WADDELL |

DRAWING SET INFORMATION

|               |                                          |
|---------------|------------------------------------------|
| PHASE:        | CONSTRUCTION                             |
| PUBLISH DATE: | 5/18/2028                                |
| PLOT SIZE:    | ARCH FULL BLEED E (36.00 X 48.00 INCHES) |
| PLOT SCALE:   | 1" = 1'-0"                               |
| APPROVED BY:  | ----                                     |

SHEET REVISION INFORMATION

|                          |                      |       |
|--------------------------|----------------------|-------|
| REVISION                 | REVISION DATE        | ----  |
| -----                    | REVISION DESCRIPTION | ----- |
| REVISION & ISSUE HISTORY |                      |       |
| ISSUED FOR:              | REV.                 | DATE: |
| 1                        |                      |       |
| 2                        |                      |       |
| 3                        |                      |       |
| 4                        |                      |       |
| 5                        |                      |       |
| 6                        |                      |       |
| 7                        |                      |       |
| 8                        |                      |       |
| 9                        |                      |       |
| 10                       |                      |       |



APPELLATION SUN VALLEY

WIREFATH AND BACKBOXES

LEVEL P1

AV101



| SHEET CABLE LEGEND |           |                    |                     |     |
|--------------------|-----------|--------------------|---------------------|-----|
| ABBREV             | MAKE      | MODEL              | DESCRIPTION         | QTY |
| HD4                |           |                    | 15' HDMI CABLE      | 6   |
| HD5                |           |                    | 30' HDMI CABLE      | 2   |
| MC1                | WEST PENN | 25291BBK           | MIC/LINE CABLE      | 4   |
| SP1                | WEST PENN | 25225BGY           | 16AWG SPEAKER CABLE | 2   |
| ST1                | CRESTRON  | DM-CBL-8G-P-SP1000 | HDBASET CABLE       | 2   |
| UT1                | WEST PENN | 254246ABK          | DATA CABLE          | 16  |

| SHEET ENCLOSURE LEGEND |     |      |                     |                   |       |
|------------------------|-----|------|---------------------|-------------------|-------|
| LOCATION               | SYM | GANG | DESCRIPTION         | ELEVATION         | SHEET |
| AVP3                   | [B] | 3    | 3" DEEP BACKBOX     | SWITCH HEIGHT     | AV701 |
| AVP4                   | [B] |      |                     |                   | AV701 |
| AVP5                   | [B] | 2    | 3" DEEP BACKBOX     | RECEPTACLE HEIGHT | AV701 |
| AVP6                   | [B] | 3    | 3" DEEP BACKBOX     | SWITCH HEIGHT     | AV701 |
| DME1                   | [B] | 1    | 3" DEEP BACKBOX     | +11' AFF          |       |
| ERK2                   | [E] | 0    | 26RU EQUIPMNET RACK |                   |       |
| SPK3                   | [E] | 1    | LANDSCAPE SPEAKER   | FIELD DETERMINED  |       |
| SPK4                   | [E] | 1    | LANDSCAPE SUBWOOFER | FIELD DETERMINED  |       |
| TP12                   | [B] | 2    | 3" DEEP BACKBOX     | SWITCH HEIGHT     | AV701 |
| VDS1                   | [A] | 1    | 3" DEEP BACKBOX     | FIELD DETERMINED  |       |
| VDS3                   | [G] |      | DISPLAY LOCATION    | 60" AFF           |       |



PROJECT INFORMATION


|                                                      |                                    |
|------------------------------------------------------|------------------------------------|
| 5853                                                 |                                    |
| APPELLATION SUN VALLEY                               |                                    |
| AUDIO VIDEO INTEGRATION                              |                                    |
| CUSTOMER NAME:<br>HARRIMAN SUN VALLEY HOTEL          | CUSTOMER NUMBER:<br>APH001         |
| SITE NAME:<br>HARRIMAN SUN VALLEY HOTEL              | SITE NUMBER:<br>72338311           |
| SITE ADDRESS:<br>300 E RIVER ST<br>KETCHUM, ID 83353 |                                    |
| SALES PERSON:<br>JEREMY WADDELL                      | ENGINEERED BY:<br>ADAM HANDY       |
| DRAWN BY:<br>ELI ANDERSON                            | PROJECT MANAGER:<br>JEREMY WADDELL |

DRAWING SET INFORMATION

|               |                                          |
|---------------|------------------------------------------|
| PHASE:        | CONSTRUCTION                             |
| PUBLISH DATE: | 5/18/2028                                |
| PLOT SIZE:    | ARCH FULL BLEED E (36.00 X 48.00 INCHES) |
| PLOT SCALE:   | 1" = 1'-0"                               |
| APPROVED BY:  |                                          |

SHEET REVISION INFORMATION

| REVISION                 | REVISION DATE | REVISION DESCRIPTION |
|--------------------------|---------------|----------------------|
| ---                      | ---           | ---                  |
| REVISION & ISSUE HISTORY |               |                      |
| ISSUED FOR:              | REV.          | DATE:                |
| 1                        |               |                      |
| 2                        |               |                      |
| 3                        |               |                      |
| 4                        |               |                      |
| 5                        |               |                      |
| 6                        |               |                      |
| 7                        |               |                      |
| 8                        |               |                      |
| 9                        |               |                      |
| 10                       |               |                      |

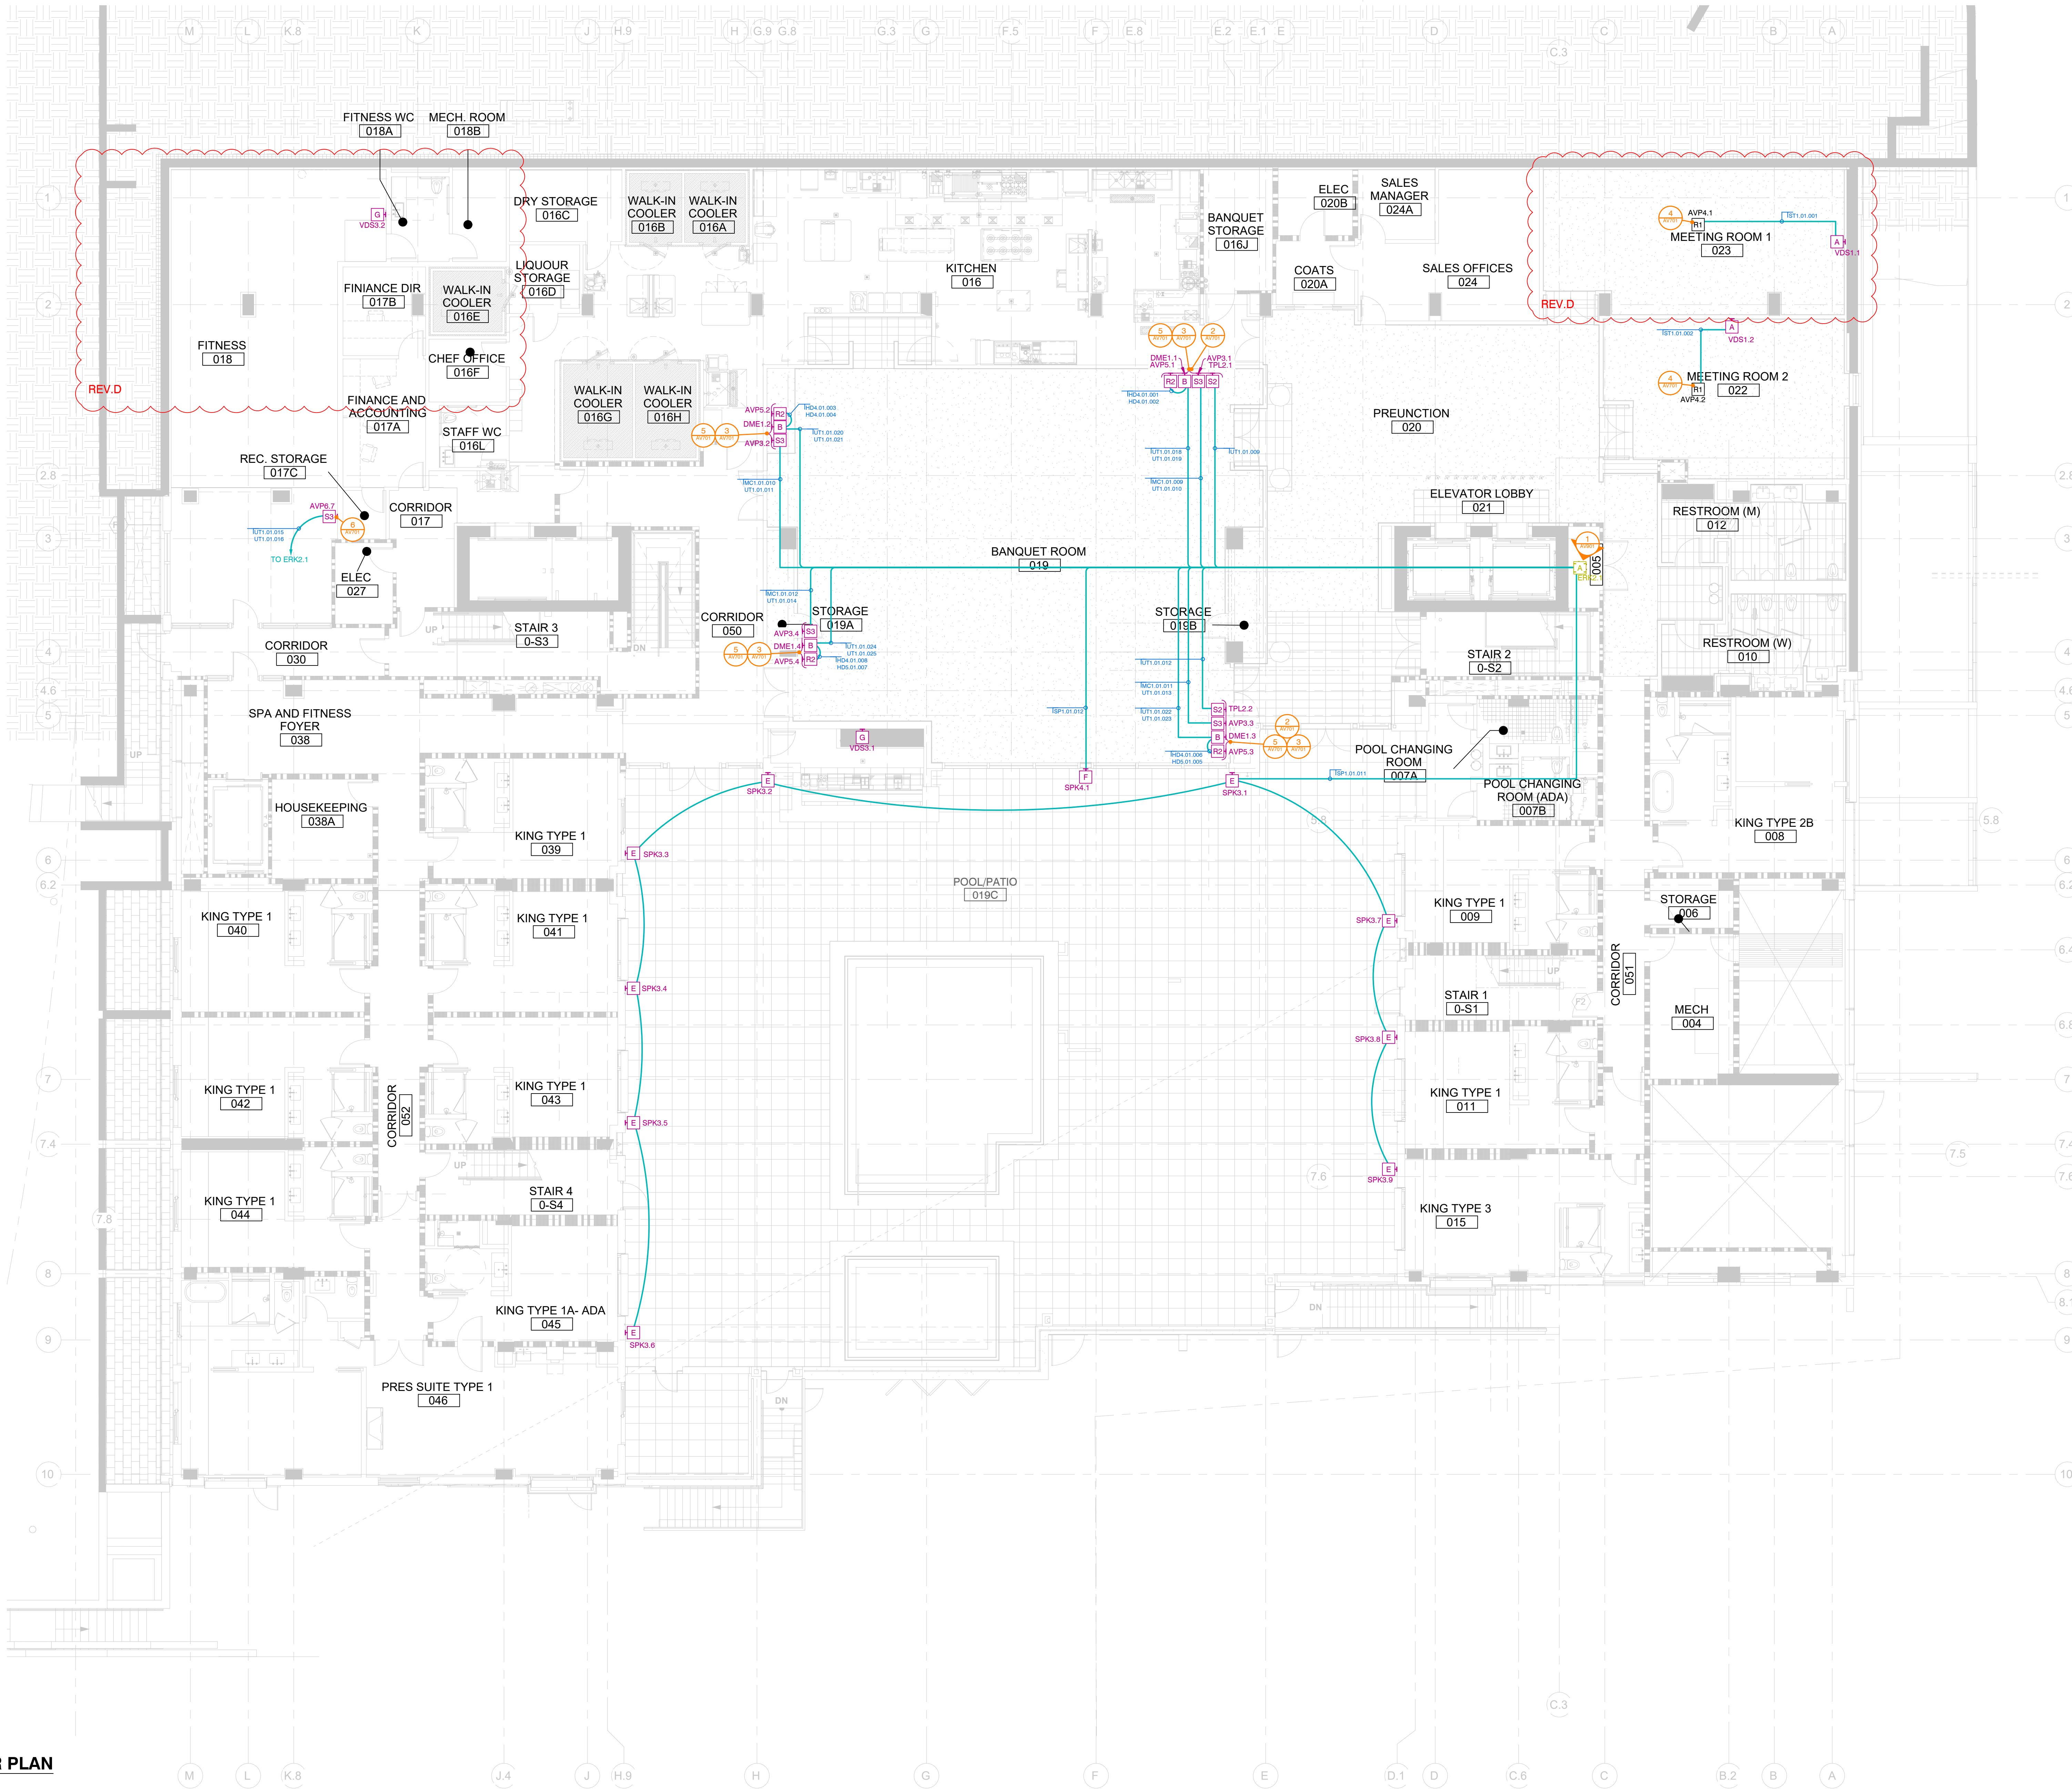

APPELLATION SUN VALLEY  
WIREPATH AND BACKBOXES  
LEVEL 1


AV102








| SHEET ENCLOSURE LEGEND |                                                                                   |      |                          |                  |       |        |
|------------------------|-----------------------------------------------------------------------------------|------|--------------------------|------------------|-------|--------|
| LOCATION               | SYM                                                                               | GANG | DESCRIPTION              | ELEVATION        | SHEET | DETAIL |
| ERK1                   |  | 0    | 26RU EQUIPMENT RACK      |                  | AV901 | 1      |
| SPK1                   |                                                                                   | 0    | 6" SELF ENCLOSED SPEAKER | FLUSH IN CEILING |       |        |

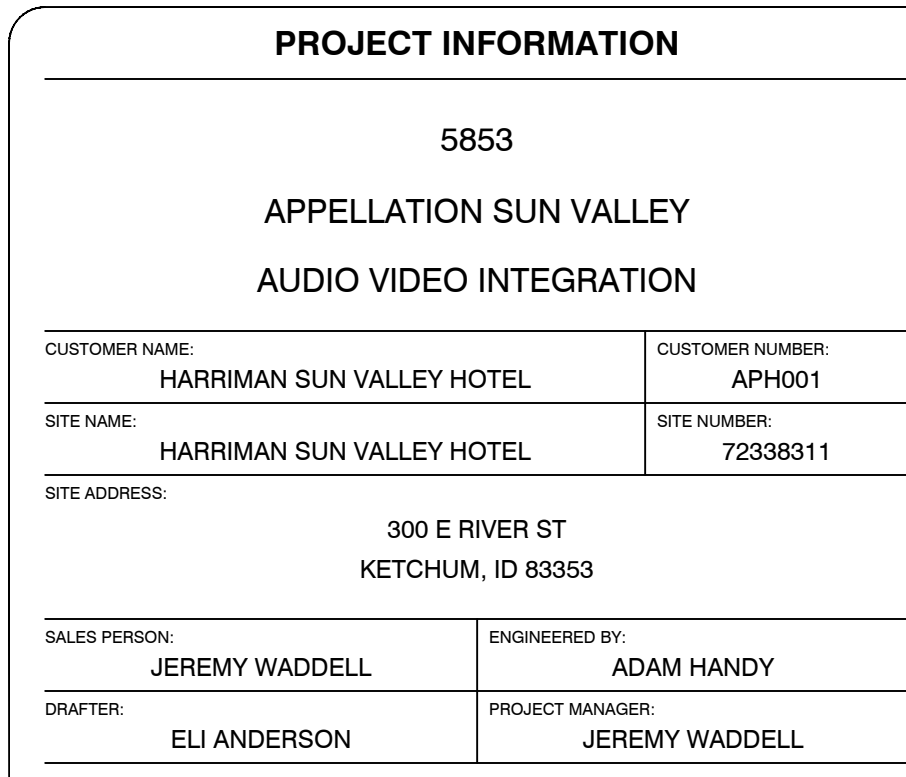

| DRAWING SET INFORMATION |                                          |
|-------------------------|------------------------------------------|
| PHASE:                  | CONSTRUCTION                             |
| PUBLISH DATE:           | 5/18/2028                                |
| PLOT SIZE:              | ARCH FULL BLEED E (36.00 X 48.00 INCHES) |
| PLOT SCALE:             | 1' = 1'-0"                               |
| APPROVED BY:            |                                          |

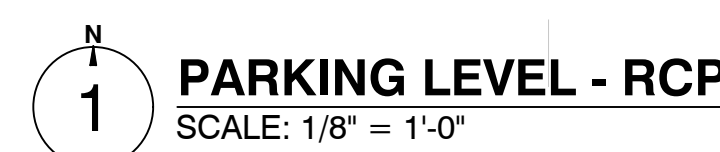[illegible]


APPELLATION SUN VALLEY  
REFLECTED CEILING  
LEVEL P1

AV201


FILE NAME: AV100.DWG



| SHEET ENCLOSURE LEGEND |     |      |                            |                  |       |        |
|------------------------|-----|------|----------------------------|------------------|-------|--------|
| LOCATION               | SYM | GANG | DESCRIPTION                | ELEVATION        | SHEET | DETAIL |
| ERK2                   | Ⓜ   | 0    | 26RU EQUIPMNET RACK        |                  |       |        |
| SPK1                   | Ⓢ   | 0    | 6" SELF ENCLOSED SPEAKER   | FLUSH IN CEILING |       |        |
| SPK2                   | Ⓢ   | 0    | 8" SELF ENCLOSED SUBWOOFER | FLUSH IN CEILING |       |        |

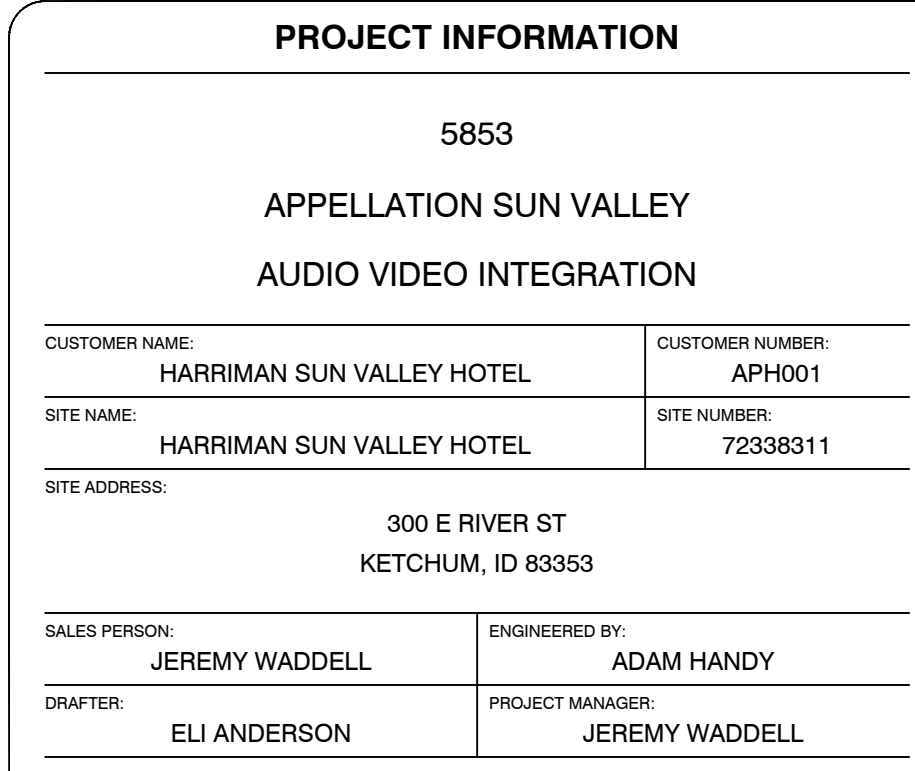

| DRAWING SET INFORMATION |                                          |
|-------------------------|------------------------------------------|
| PHASE:                  | CONSTRUCTION                             |
| PUBLISH DATE:           | 5/18/2026                                |
| PLOT SIZE:              | ARCH FULL BLEED E (36.00 X 48.00 INCHES) |
| PLOT SCALE:             | 1" = 1'-0"                               |
| APPROVED BY:            |                                          |

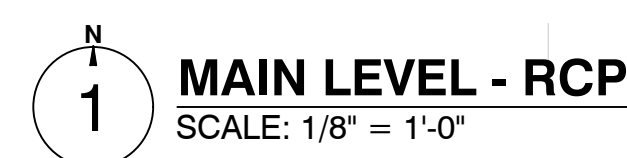[illegible]

APPELLATION SUN VALLEY  
REFLECTED CEILING  
LEVEL 1  
10000000

AV202

FILE NAME: AV100.DWG



| SHEET CABLE LEGEND |           |          |                     |     |
|--------------------|-----------|----------|---------------------|-----|
| ABBREV             | MAKE      | MODEL    | DESCRIPTION         | QTY |
| SP1                | WEST PENN | 25225BGY | 16AWG SPEAKER CABLE | 9   |

| SHEET ENCLOSURE LEGEND |     |      |                     |                  |       |
|------------------------|-----|------|---------------------|------------------|-------|
| LOCATION               | SYM | GANG | DESCRIPTION         | ELEVATION        | SHEET |
| ERK3                   |     | 0    | 26RU EQUIPMNET RACK | FLUSH IN CEILING |       |
| SPK1                   |     | 0    | 6\"/>               | FLUSH IN CEILING |       |
| SPK2                   |     | 0    | 8\"/>               | FLUSH IN CEILING |       |



PROJECT INFORMATION

5853  
APPELLATION SUN VALLEY  
AUDIO VIDEO INTEGRATION

|                |                                     |                  |                |
|----------------|-------------------------------------|------------------|----------------|
| CUSTOMER NAME: | HARRIMAN SUN VALLEY HOTEL           | CUSTOMER NUMBER: | APH001         |
| SITE NAME:     | HARRIMAN SUN VALLEY HOTEL           | SITE NUMBER:     | 72388311       |
| SITE ADDRESS:  | 300 E RIVER ST<br>KETCHUM, ID 83353 |                  |                |
| SALES PERSON:  | JEREMY WADDELL                      | ENGINEERED BY:   | ADAM HANDY     |
| DRAWN BY:      | ELI ANDERSON                        | PROJECT MANAGER: | JEREMY WADDELL |

DRAWING SET INFORMATION

|               |                                          |
|---------------|------------------------------------------|
| PHASE:        | CONSTRUCTION                             |
| PUBLISH DATE: | 5/18/2028                                |
| PLOT SIZE:    | ARCH FULL BLEED E (36.00 X 48.00 INCHES) |
| PLOT SCALE:   | 1" = 1'-0"                               |
| APPROVED BY:  | ----                                     |

SHEET REVISION INFORMATION

|                          |               |                      |
|--------------------------|---------------|----------------------|
| REVISION                 | REVISION DATE | REVISION DESCRIPTION |
| ----                     | ----          | ----                 |
| REVISION & ISSUE HISTORY |               |                      |
| ISSUED FOR:              | REV.          | DATE:                |
| 1                        |               |                      |
| 2                        |               |                      |
| 3                        |               |                      |
| 4                        |               |                      |
| 5                        |               |                      |
| 6                        |               |                      |
| 7                        |               |                      |
| 8                        |               |                      |
| 9                        |               |                      |
| 10                       |               |                      |




1 SECOND LEVEL - RCP  
SCALE: 1/8" = 1'-0"

APPELLATION SUN VALLEY  
REFLECTED CEILING  
LEVEL 2

AV203




| DESIGNATION | DESCRIPTION | LOCATION |
|-------------|-------------|----------|
| TPL-0101    | TOUCH PANEL | TPL1.1   |

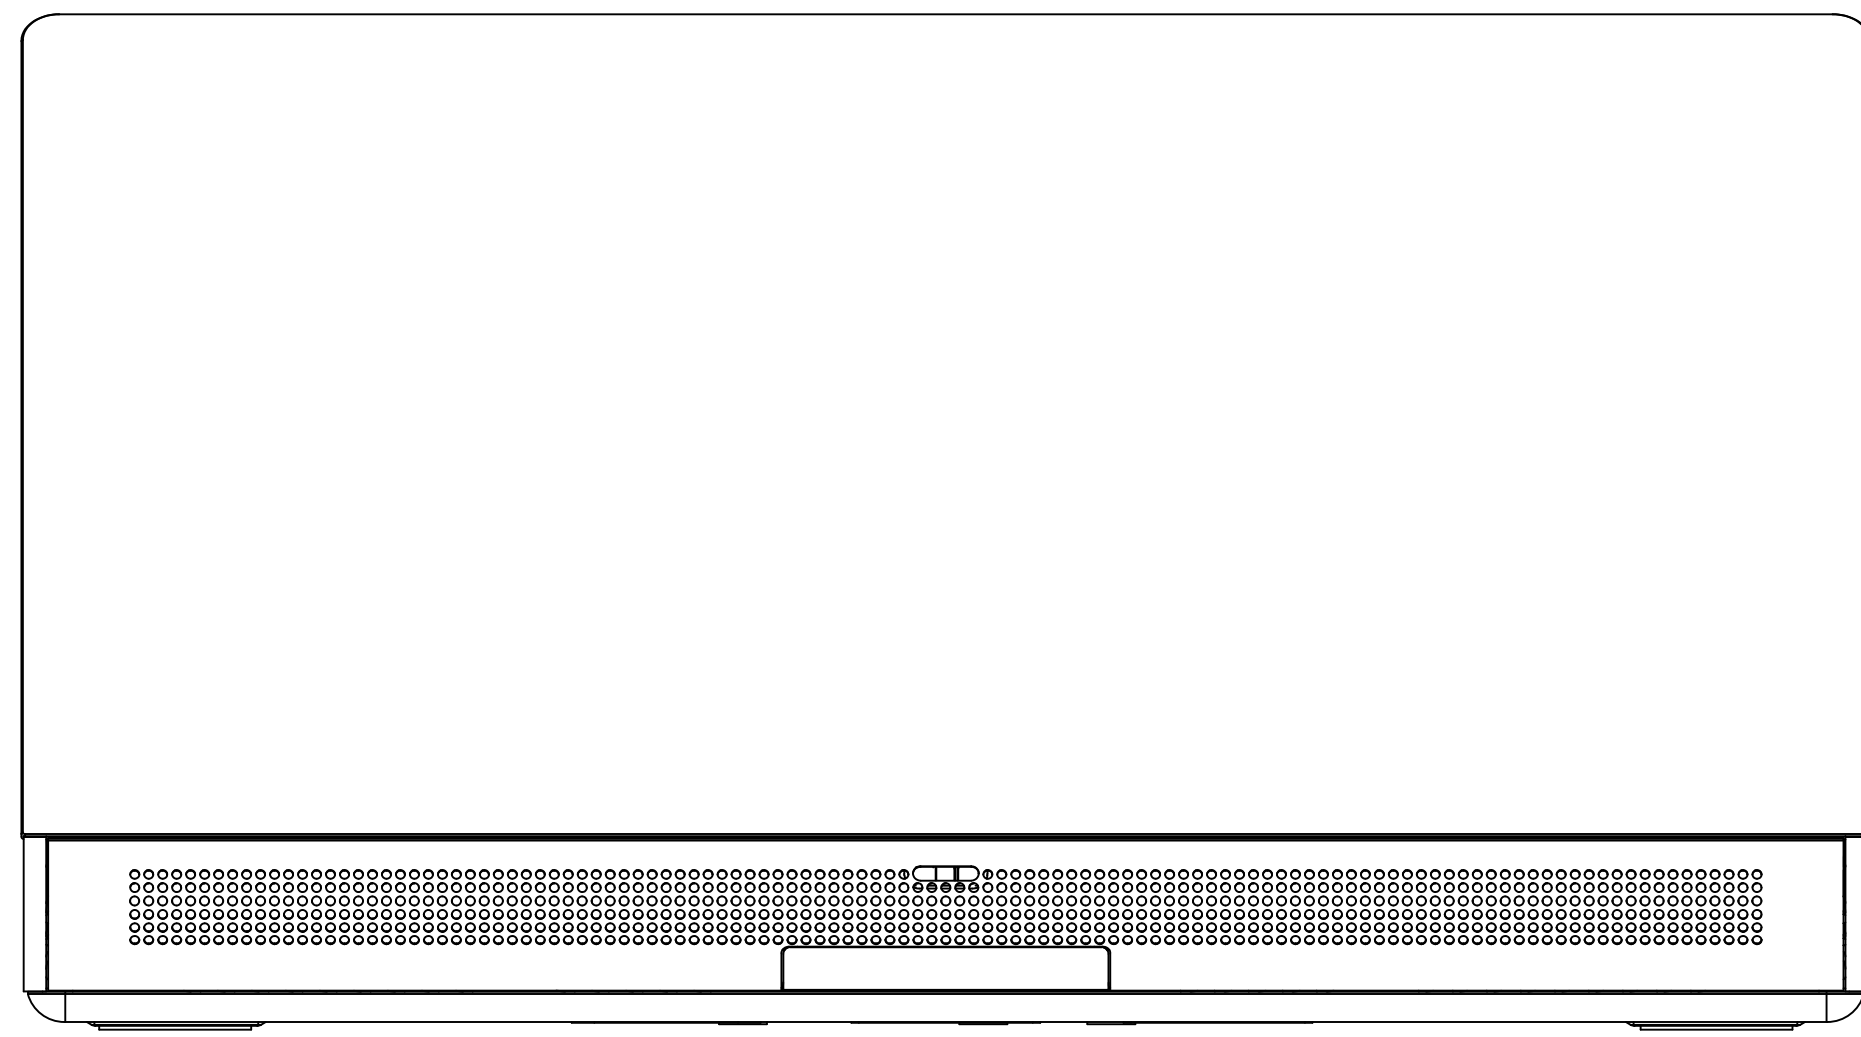


**1 TPL1**  
CRESTRON TS-1070  
SCALE: 1" = 1'-0"

| DESIGNATION | DESCRIPTION          | LOCATION |
|-------------|----------------------|----------|
| TPT-0101    | MEETING ROOM 1 DM TX | AVP4.1   |
| TPT-0102    | MEETING ROOM 2 DM TX | AVP4.2   |
| TPT-0103    | PRIVATE DINING DM TX | AVP4.3   |
| TPT-0104    | PRIVATE DINING DM TX | AVP4.5   |
| TPT-0105    | EMPLOYEE CAFE DM TX  | AVP4.4   |

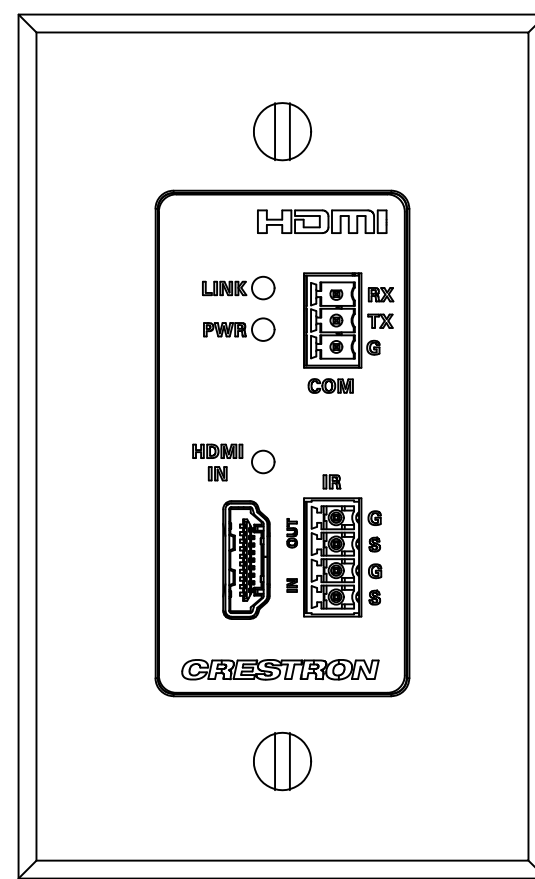


4 **AVP4**  
CRESTRON HD-TXC-4KZ-101-1G-W  
SCALE: 1' = 1'-0"

| DESIGNATION | DESCRIPTION      | LOCATION |
|-------------|------------------|----------|
| CNT-0102    | SALON CONTROLLER | KPD1.1   |

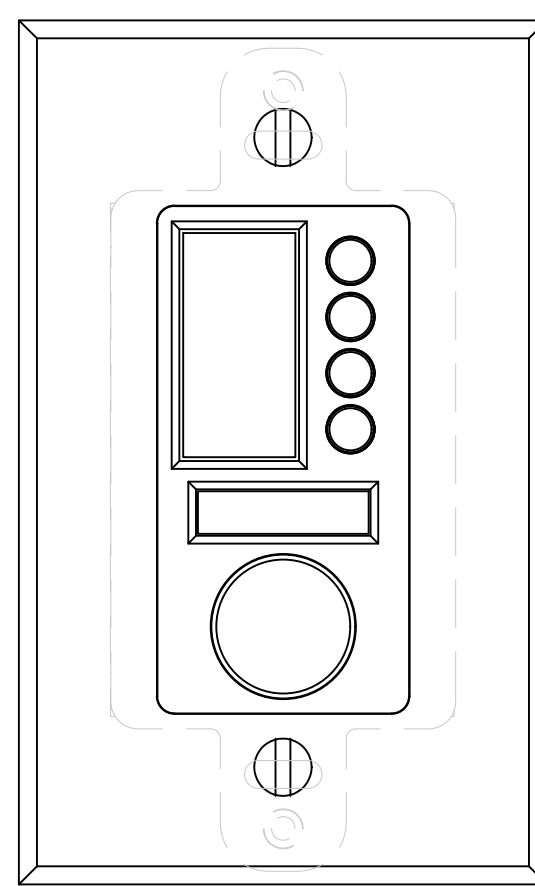


**7 KPD1**  
SYMETRIX 80-0171  
SCALE: 1" = 1'-0"

| DESIGNATION | DESCRIPTION | LOCATION |
|-------------|-------------|----------|
| TPL-0102    | TOUCH PANEL | TPL2.1   |
| TPL-0103    | TOUCH PANEL | TPL2.2   |

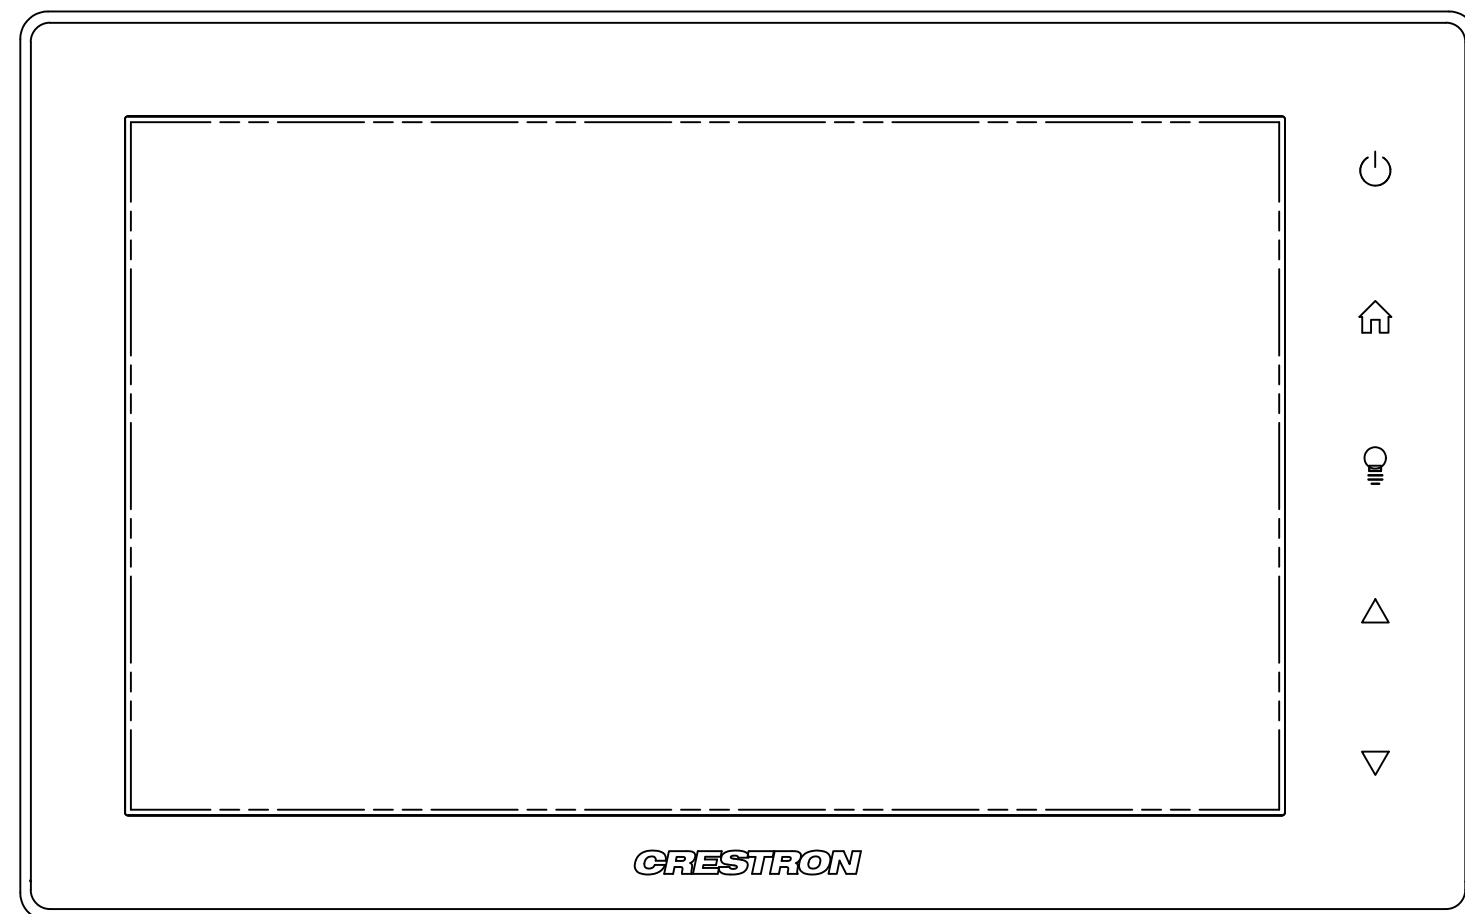


**2 TPL2**  
CRESTRON TSW-750-W-S  
SCALE: 1' = 1'-0"

| DESIGNATION | DESCRIPTION               | LOCATION |
|-------------|---------------------------|----------|
| AVP-0111    | BANQUET NORTH HDMI INPUT  | AVP5.1   |
| AVP-0112    | BANQUET NORTH HDMI OUTPUT |          |
| AVP-0113    | BANQUET NORTH HDMI INPUT  | AVP5.2   |
| AVP-0114    | BANQUET NORTH HDMI OUTPUT |          |
| AVP-0115    | HDMI INPUT                | AVP5.3   |
| AVP-0116    | HDMI OUTPUT               |          |
| AVP-0117    | BANQUET SOUTH HDMI INPUT  | AVP5.4   |
| AVP-0118    | BANQUET SOUTH HDMI OUTPUT |          |

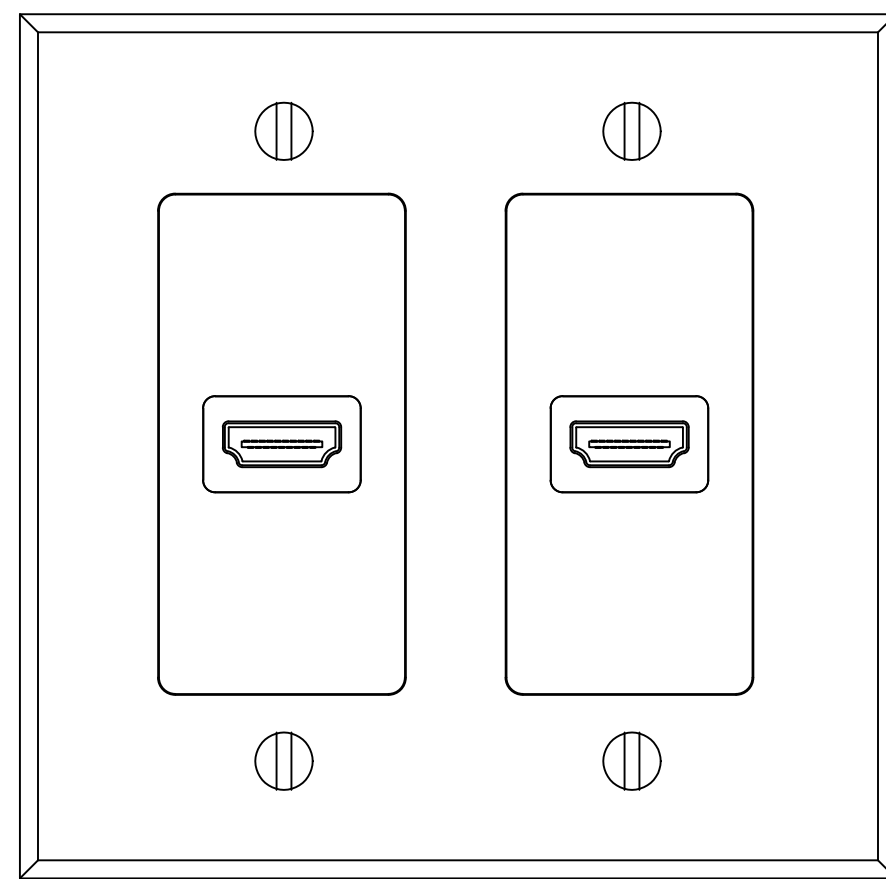


**5 AVP5**  
DUAL C2G 41043 FOR HDMI INPUT/OUTPUT  
SCALE: 1' = 1'-0"

| DESIGNATION | DESCRIPTION                | LOCATION |
|-------------|----------------------------|----------|
| TPL-0105    | PRIVATE DINING TOUCH PANEL | TPL3.1   |

 


**8 TPL3**  
CRESTRON TSW-770-B-S  
SCALE: 1" = 1'-0"

| DESIGNATION | DESCRIPTION                 | LOCATION |
|-------------|-----------------------------|----------|
| AVP-0101    | PRIVATE DINING BLUETOOTH RX | BTP1.1   |

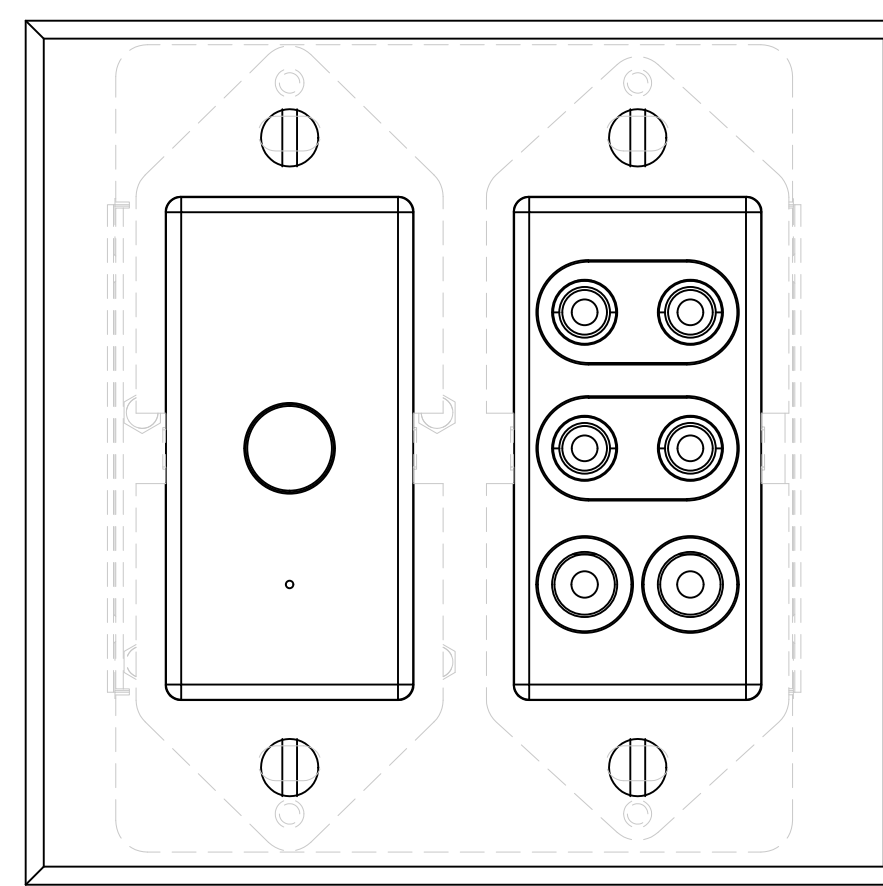


**9 BTP1**  
SYMETRIX XIO BLUETOOTH RCA-3.5  
SCALE: 1' = 1'-0"

| DESIGNATION | DESCRIPTION                | LOCATION |
|-------------|----------------------------|----------|
| AVP-0106    | BANQUET NORTH BLUETOOTH RX | AVP3.1   |
| MIP-0101    | BANQUET NORTH AUX AUDIO    |          |
| AVP-0107    | BANQUET NORTH BLUETOOTH RX | AVP3.2   |
| MIP-0102    | BANQUET NORTH AUX AUDIO    |          |
| AVP-0108    | BANQUET SOUTH BLUETOOTH RX | AVP3.3   |
| MIP-0103    | BANQUET SOUTH AUX AUDIO    |          |
| AVP-0109    | BANQUET SOUTH BLUETOOTH RX | AVP3.4   |
| MIP-0104    | BANQUET SOUTH AUX AUDIO    |          |

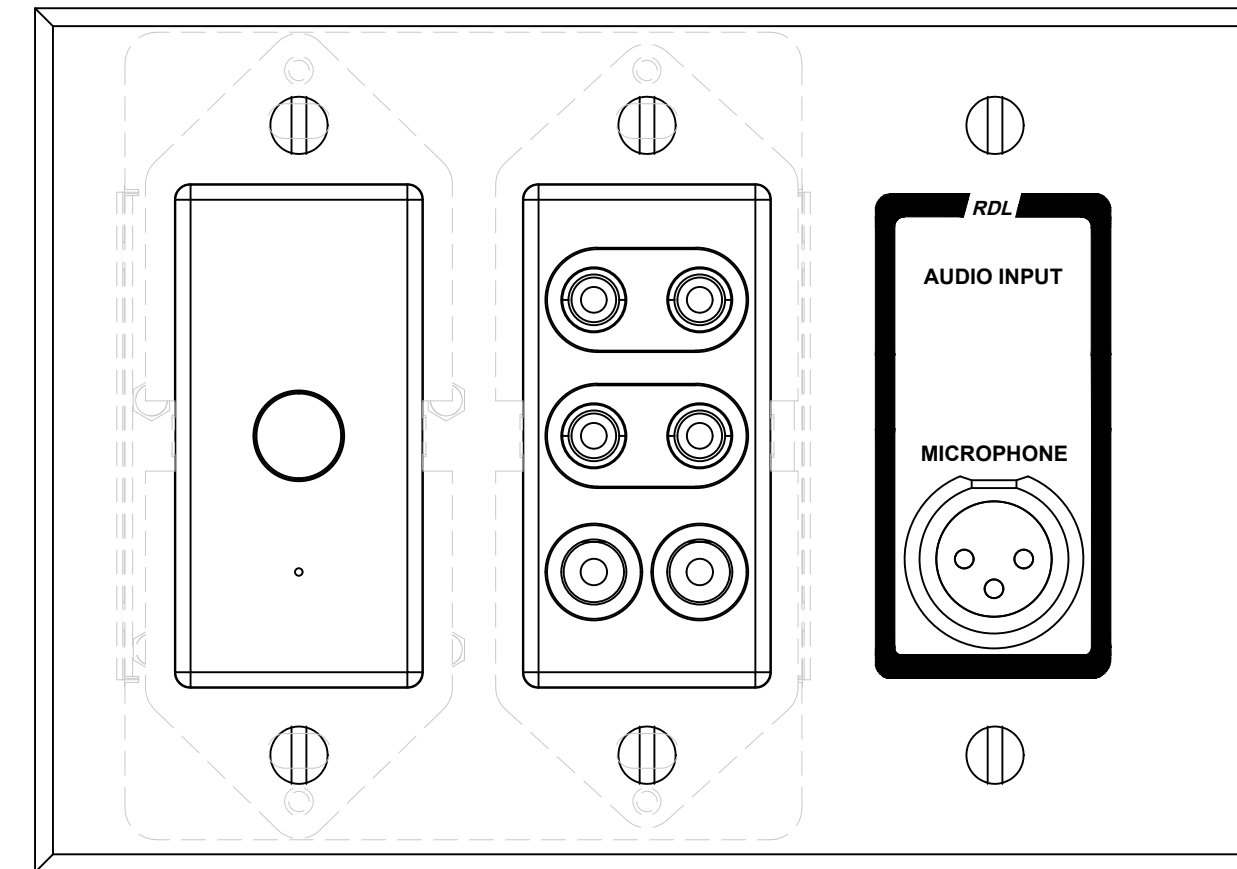

**3 AVP3**  
DUAL C2G 41043 FOR HDMI INPUT/OUTPUT  
SCALE: 1' = 1'-0"

| DESIGNATION | DESCRIPTION                     | LOCATION |
|-------------|---------------------------------|----------|
| AVP-0121    | SAUNA 1 BLUETOOTH RX            | AVP6.2   |
| CNT-0103    | SAUNA 1 CONTROLLER              |          |
| AVP-0122    | SAUNA 1 BLUETOOTH RX            |          |
| CNT-0104    | SAUNA 2 CONTROLLER              | AVP6.3   |
| AVP-0123    | SAUNA 3 BLUETOOTH RX            | AVP6.4   |
| CNT-0105    | SAUNA 3 CONTROLLER              |          |
| AVP-0124    | SAUNA 4 BLUETOOTH RX            |          |
| CNT-0106    | SAUNA 4 CONTROLLER              | AVP6.5   |
| AVP-0125    | SAUNA 5 BLUETOOTH RX            | AVP6.6   |
| CNT-0107    | SAUNA 5 CONTROLLER              |          |
| AVP-0105    | FITNESS BLUETOOTH RX            |          |
| CNT-0108    | FITNESS CONTROLLER              | AVP6.7   |
| AVP-0102    | RESTAURANT AND BAR BLUETOOTH RX | AVP6.9   |
| CNT-0110    | RESTAURANT AND BAR CONTROLLER   |          |
| AVP-0103    | ADVENTURE CLUB BLUETOOTH RX     |          |
| CNT-0111    | ADVENTURE CLUB CONTROLLER       | AVP6.10  |
| AVP-0104    | BAKERY BLUETOOTH RX             | AVP6.11  |
| CNT-0112    | BAKERY CONTROLLER               |          |
| AVP-0126    | SERVICE CORRIDOR BLUETOOTH RX   |          |
| CNT-0114    | SERVICE CORRIDOR CONTROLLER     | AVP6.12  |

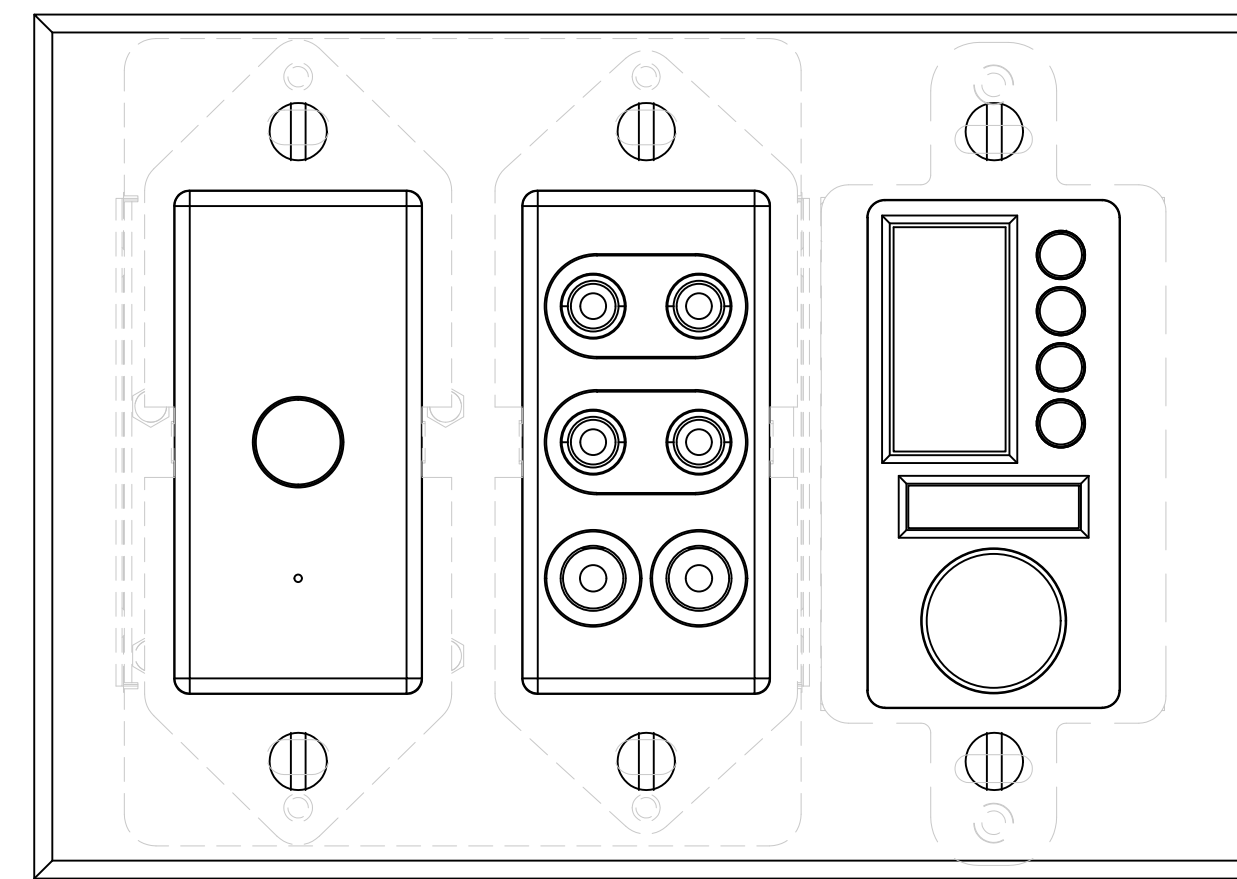

**6 AVP6**  
SYMETRIX XIO BLUETOOTH RCA-3.5 WITH SYMETRIX 80-0171  
SCALE: 1' = 1'-0"



## PROJECT INFORMATION

5853

APPELLATION SUN VALLEY  
AUDIO VIDEO INTEGRATION

|                                                      |                                    |                              |
|------------------------------------------------------|------------------------------------|------------------------------|
| CUSTOMER NAME:<br>HARRIMAN SUN VALLEY HOTEL          |                                    | CUSTOMER NUMBER:<br>APH001   |
| SITE NAME:<br>HARRIMAN SUN VALLEY HOTEL              |                                    | SITE NUMBER:<br>72338311     |
| SITE ADDRESS:<br>300 E RIVER ST<br>KETCHUM, ID 83353 |                                    |                              |
| SALES PERSON:<br>JEREMY WADDELL                      |                                    | ENGINEERED BY:<br>ADAM HANDY |
| OWNER:<br>ELI ANDERSON                               | PROJECT MANAGER:<br>JEREMY WADDELL |                              |

### DRAWING SET INFORMATION

|               |                                          |
|---------------|------------------------------------------|
| PHASE:        | CONSTRUCTION                             |
| PUBLISH DATE: | 5/18/2028                                |
| PLOT SIZE:    | ARCH FULL BLEED E (36.00 X 48.00 INCHES) |
| PLOT SCALE:   | 1" = 1'-0"                               |
| APPROVED BY:  |                                          |

### SHEET REVISION INFORMATION

[illegible]

APPELLATION SUN VALLEY

## PLATE DETAILS


## UTILIZED PLATES

11

# AV701

FILE NAME: AV700.DWG



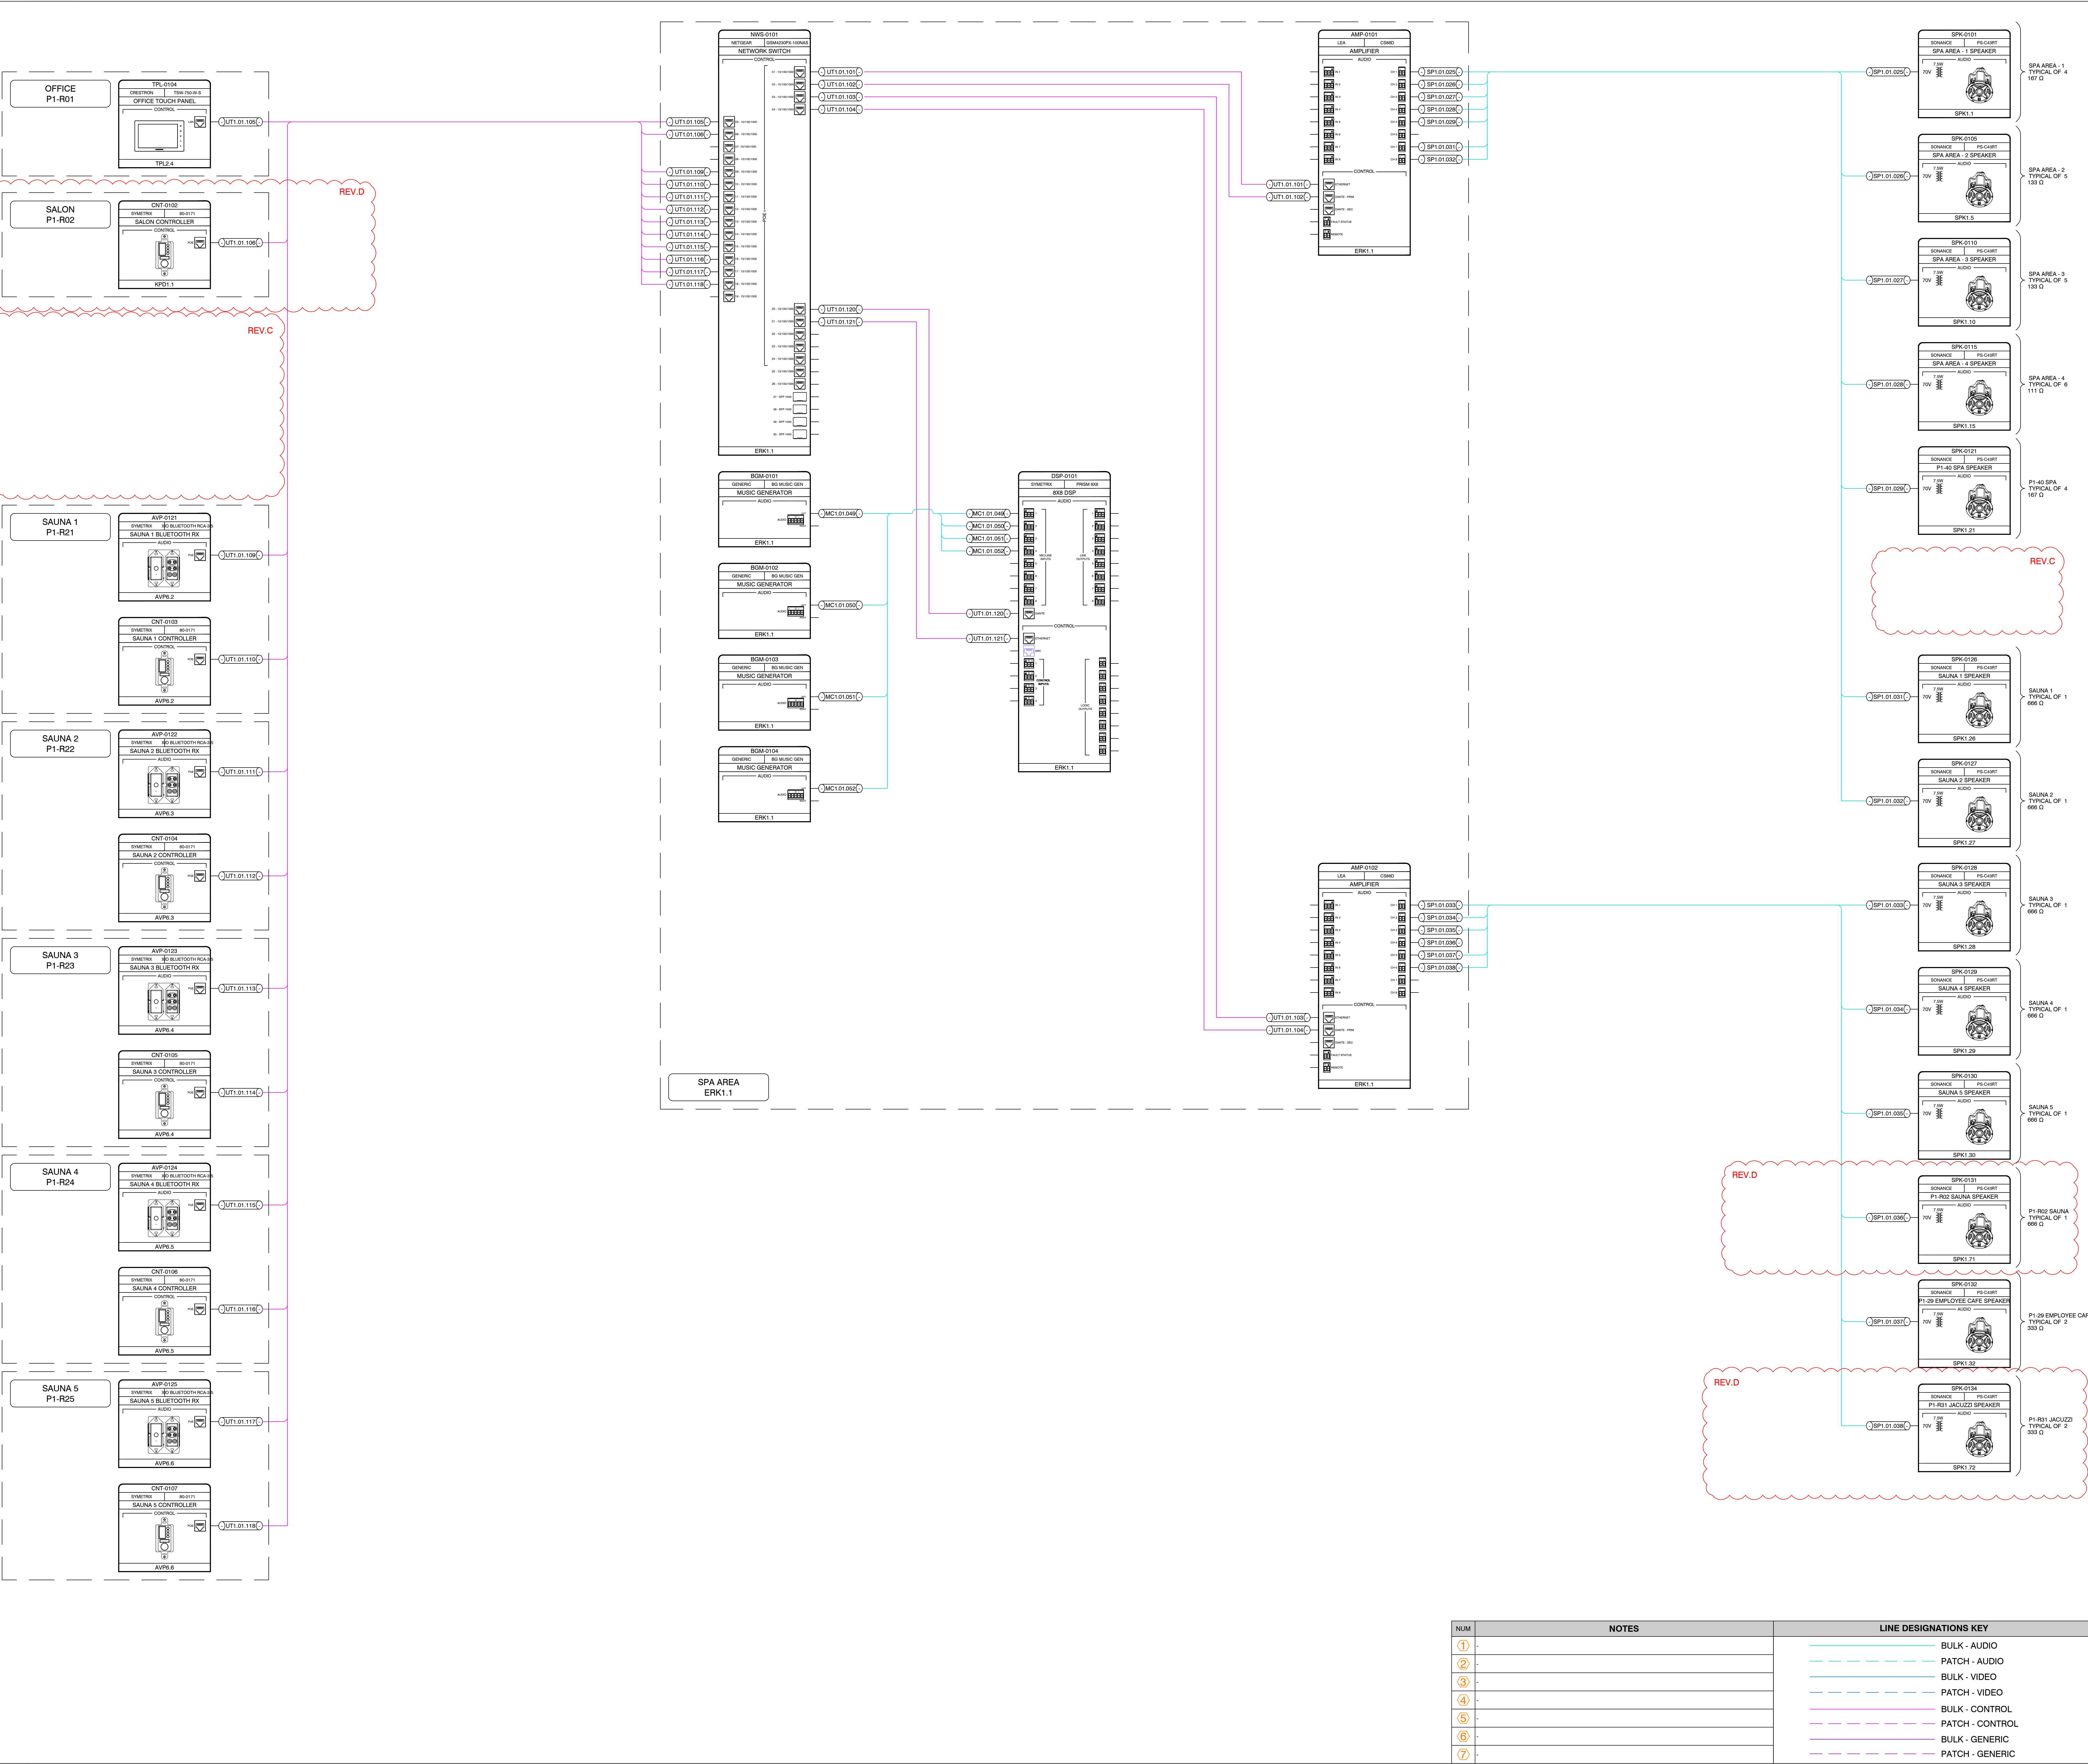

| NUM | NOTES | LINE DESIGNATIONS KEY |
|-----|-------|-----------------------|
| ①   |       | BULK - AUDIO          |
| ②   |       | PATCH - AUDIO         |
| ③   |       | BULK - VIDEO          |
| ④   |       | PATCH - VIDEO         |
| ⑤   |       | BULK - CONTROL        |
| ⑥   |       | PATCH - CONTROL       |
| ⑦   |       | BULK - GENERIC        |
|     |       | PATCH - GENERIC       |

www.marshallind.com

PROJECT INFORMATION

5853

APPELLATION SUN VALLEY

AUDIO VIDEO INTEGRATION

|                |                                     |                  |                |
|----------------|-------------------------------------|------------------|----------------|
| CUSTOMER NAME: | HARRIMAN SUN VALLEY HOTEL           | CUSTOMER NUMBER: | APH001         |
| SITE NAME:     | HARRIMAN SUN VALLEY HOTEL           | SITE NUMBER:     | 72388311       |
| SITE ADDRESS:  | 300 E RIVER ST<br>KETCHUM, ID 83353 |                  |                |
| SALES PERSON:  | JEREMY WADDELL                      | ENGINEERED BY:   | ADAM HANDY     |
| DRAWN:         | EU ANDERSON                         | PROJECT MANAGER: | JEREMY WADDELL |

DRAWING SET INFORMATION

PHASE: CONSTRUCTION

PUBLISH DATE: 5/18/2028

PLOT SIZE: ARCH FULL BLEED E (36.00 X 48.00 INCHES)

PLOT SCALE: 1" = 1'-0"

APPROVED BY: \_\_\_\_\_

SHEET REVISION INFORMATION

| REVISION | REVISION DATE | REVISION DESCRIPTION |
|----------|---------------|----------------------|
| ---      | ---           | ---                  |

REVISION & ISSUE HISTORY

| ISSUED FOR: | REV. | DATE: |
|-------------|------|-------|
| ---         | ---  | ---   |

APPELLATION SUN VALLEY

SINGLE LINE DIAGRAMS


RESORT AV

LEVEL P1 RACK - SPA


AV801.1

FILE NAME: AV800.DWG





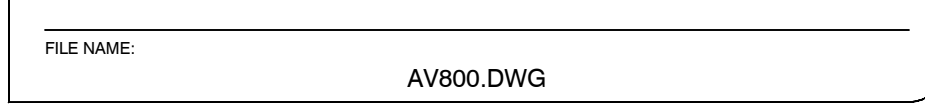



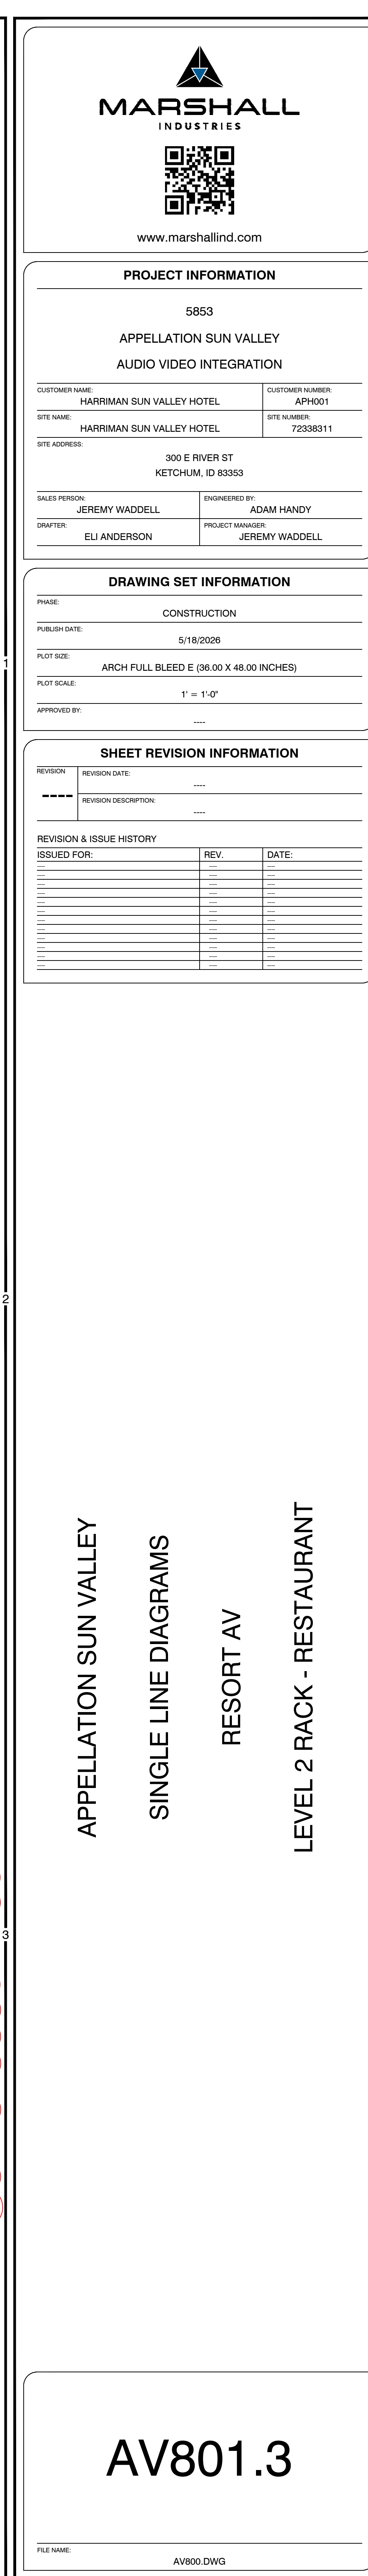

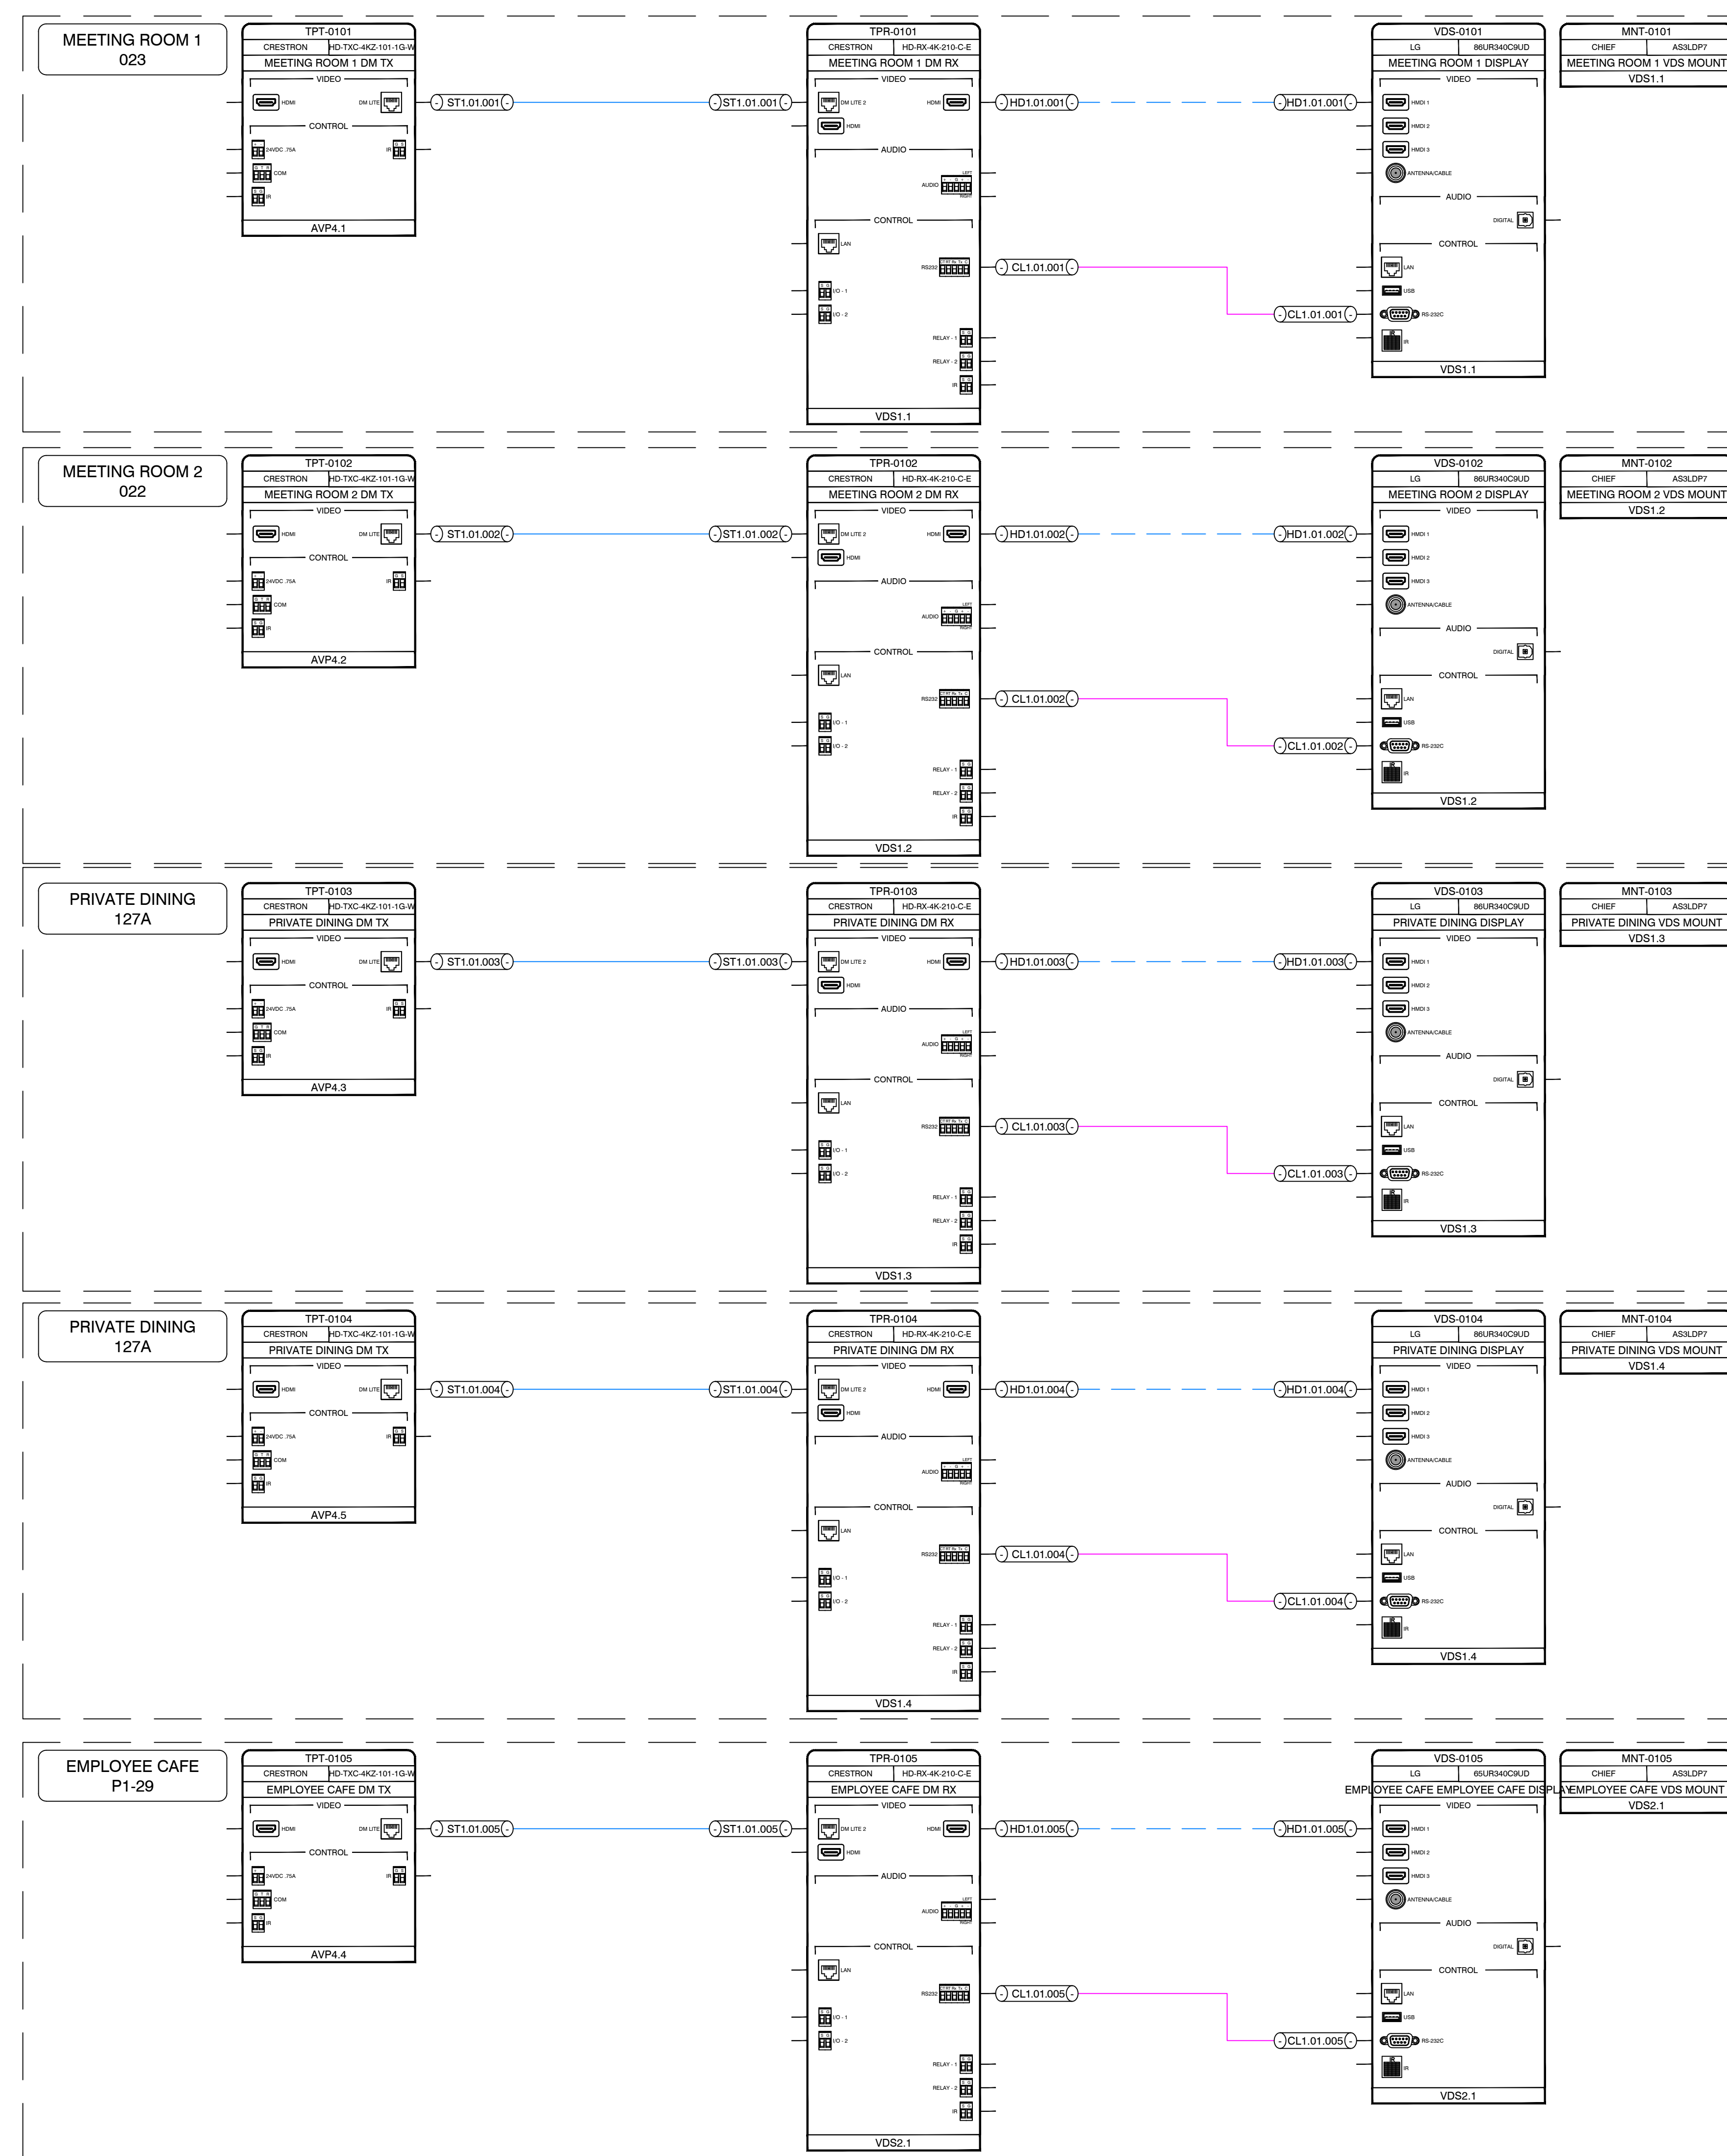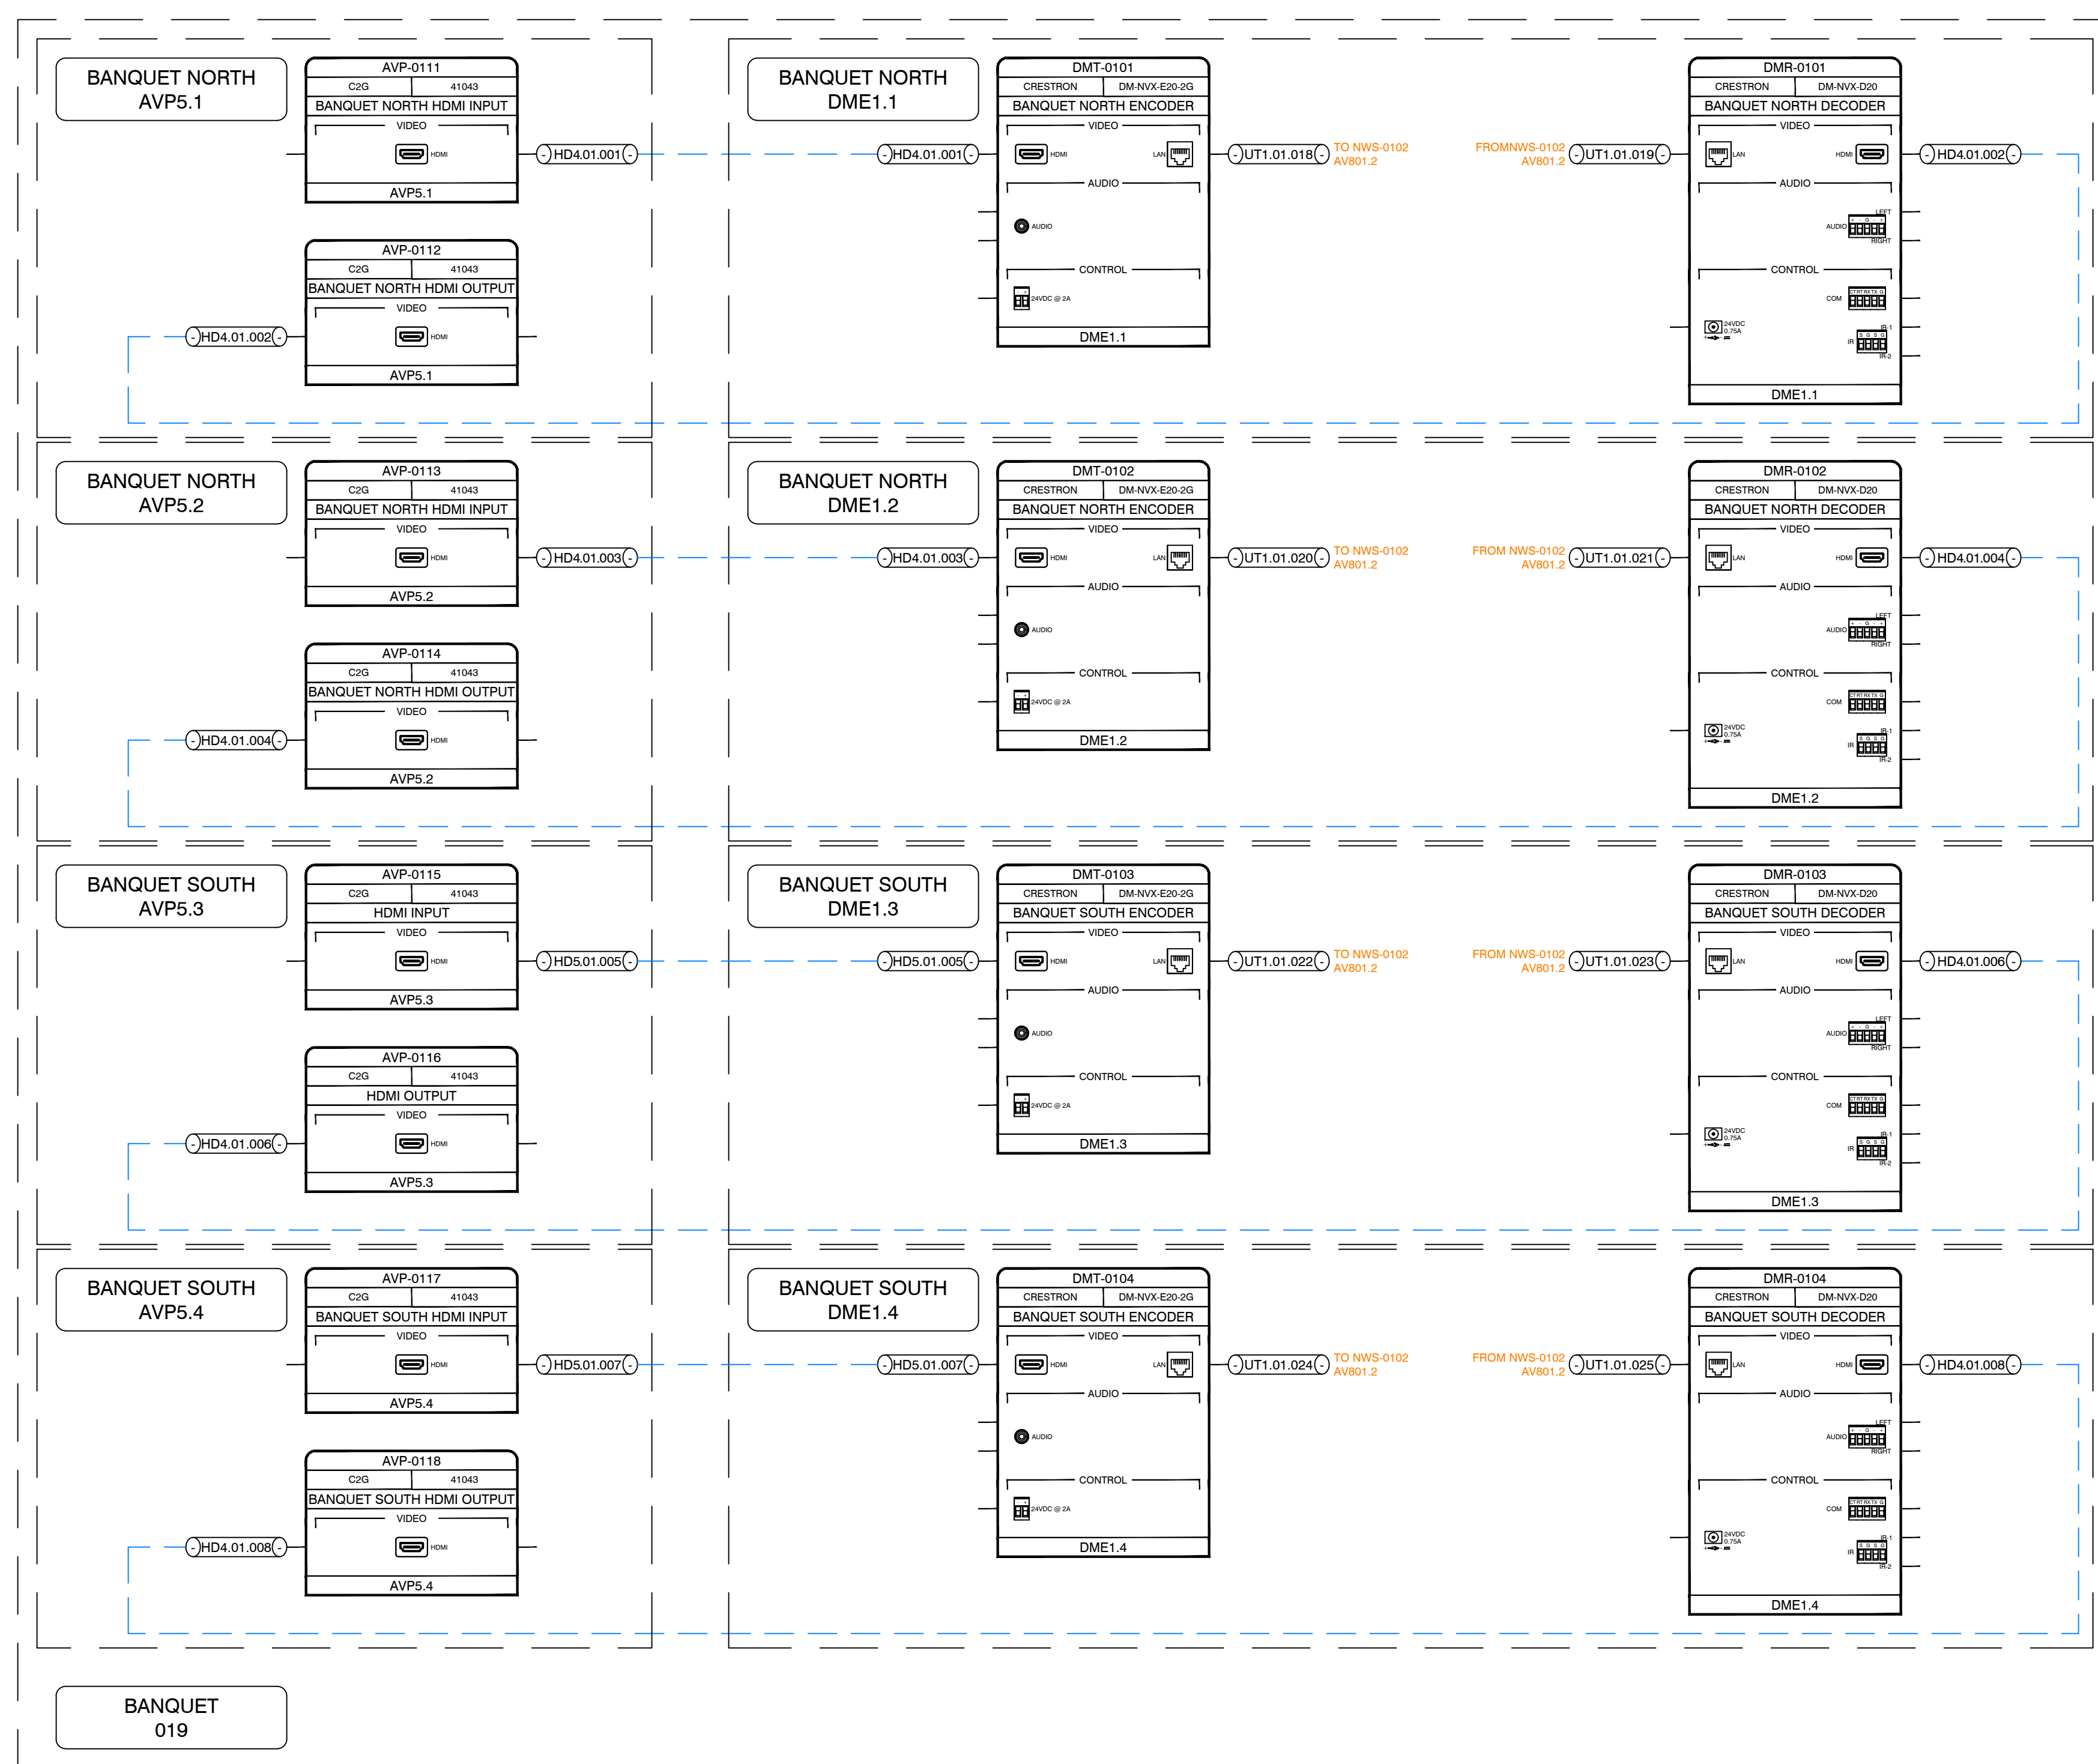

[illegible]

| NOTES |  | LINE DESIGNATIONS KEY                                                                 |                 |
|-------|--|---------------------------------------------------------------------------------------|-----------------|
| ① -   |  |  | BULK - AUDIO    |
| ② -   |  |  | PATCH - AUDIO   |
| ③ -   |  |  | BULK - VIDEO    |
| ④ -   |  |  | PATCH - VIDEO   |
| ⑤ -   |  |  | BULK - CONTROL  |
| ⑥ -   |  |  | PATCH - CONTROL |
| ⑦ -   |  |  | BULK - GENERIC  |
|       |  |  | PATCH - GENERIC |





## 5853

## AUDIO VIDEO INTEGRATION

|                                 |                                    |
|---------------------------------|------------------------------------|
| SALES PERSON:<br>JEREMY WADDELL | ENGINEERED BY:<br>ADAM HANDY       |
| DRAFTER:<br>ELI ANDERSON        | PROJECT MANAGER:<br>JEREMY WADDELL |

## PHASE:

APPROVED BY:

|          |                |
|----------|----------------|
| REVISION | REVISION DATE: |
|----------|----------------|

| REVISION | REVISION DESCRIPTION |
|----------|----------------------|
| 0001     | Initial release      |

|             |      |       |
|-------------|------|-------|
| ISSUED FOR: | REV. | DATE: |
|-------------|------|-------|

|      |      |      |
|------|------|------|
| 2019 | 2019 | 2019 |
| 2018 | 2018 | 2018 |
| 2017 | 2017 | 2017 |
| 1892 | 1892 | 1892 |

FILE NAME: AV900.DWG



1 **ERK1**  
SCALE: 3" = 1'-0"



2 **ERK2**  
SCALE: 3" = 1'-0"



3 ERK3  
SCALE: 3" = 1'-0"