

APPELLATION SUN VALLEY AUDIO VIDEO INTEGRATION

AUDIOVISUAL SHOP DRAWINGS

MARSHALL INDUSTRIES • 1303 NORTH 39TH STREET, NAMPA, ID • 208.442.7222

TABLE OF CONTENTS

REV	DRAWING NUMBER	TITLE	DESCRIPTION	APP BY
AV000 - GENERAL DRAWINGS				
A	AV000	TABLE OF CONTENTS		
	AV001	AV LEGENDS AND KEYS	ROUGH-IN	
	AV002	AV LEGENDS AND KEYS	STRUCTURED CABLING	
AV100 - WIREPATH AND BACKBOXES				
	AV101	LEVEL P1		
	AV102	LEVEL 1		
	AV103	LEVEL 2		
AV200 - REFLECTED CEILING				
	AV201	LEVEL P1		
	AV202	LEVEL 1		
	AV203	LEVEL 2		
AV700 - PLATE DETAILS				
	AV701	UTILIZED PLATES		
AV800 - SINGLE LINE DIAGRAMS				
	AV801.1	RESORT AV	LEVEL P1 RACK - SPA	
A	AV801.2	RESORT AV	LEVEL 1 RACK - BANQUET	
	AV801.3	RESORT AV	LEVEL 2 RACK - RESTAURANT	
	AV801.4	RESORT AV	VIDEO SYSTEM FUNCTIONAL	
AV900 - ENCLOSURE ELEVATIONS				
A	AV901	UTILIZED RACKS		



www.marshallind.com

PROJECT INFORMATION

853

APPELLATION SUN VALLEY
AUDIO VIDEO INTEGRATION

CUSTOMER NAME: HARRIMAN SUN VALLEY HOTEL	CUSTOMER NUMBER: APH001
SITE NAME: HARRIMAN SUN VALLEY HOTEL	SITE NUMBER: 72338311
SITE ADDRESS: 300 E RIVER ST KETCHUM, ID 83353	

SALES PERSON: JEREMY WADDELL	ENGINEERED BY: ADAM HANDY
DRAFTER: ELI ANDERSON	PROJECT MANAGER: JEREMY WADDELL

DRAWING SET INFORMATION

PHASE:	CONSTRUCTION
PUBLISH DATE:	6/1/2026
PLOT SIZE:	ARCH FULL BLEED E (36.00 X 48.00 INCHES)
PLOT SCALE:	1" = 1'-0"
APPROVED BY:	

SHEET REVISION INFORMATION

REVISION	REVISION DATE:
A	6/1/2026
	REVISION DESCRIPTION:
	INTERNAL CHANGES

REVISION & ISSUE HISTORY

[illegible]

APPELLATION SUN VALLEY



GENERAL DRAWINGS

TABLE OF CONTENTS

AV000

FILE NAME: AV000.DWG

ENCLOSURE LEGEND																							
SYM		DESCRIPTION		ELEVATION		QTY					SYM		TYPE		GANG		DESCRIPTION		ELEVATION		QTY		
COMMONLY USED WALL BOXES						1G	2G	3G	4G	5G	6G	CEILING BOXES											
C#		GENERIC 3" DEEP BACKBOX. REFER TO # FOR GANG SIZE.		COUNTER HEIGHT		0	0	0	0	0	0	A		SONANCE PS-C63RTL		0		6" SELF ENCLOSED SPEAKER		FLUSH IN CEILING		100	
R#				RECEPTACLE HEIGHT		3	4	0	0	0	0	B		SONANCE PS-C83RWT		0		8" SELF ENCLOSED SUBWOOFER		FLUSH IN CEILING		6	
S#				SWITCH HEIGHT		0	4	16	0	0	0	C											
D												D											
E												E											
F												F											
G												G											
H												H											
I												I											
J												J											
K												K											
L												L											
M												M											
N																							
O																							
P																							
Q																							
T																							
U																							
V																							
W																							
X																							
SYM		TYPE		GANG		DESCRIPTION		ELEVATION		QTY		SYM		TYPE		GANG		DESCRIPTION		ELEVATION		QTY	
PROJECT SPECIFIC WALL BOXES												FLOOR BOXES											
A				1		3" DEEP BACKBOX		FIELD DETERMINED		5		A				1				FINISH FLOOR		0	
B				1		3" DEEP BACKBOX		+11' AFF		4		B											
D				1		SPEAKER LOCATION		FIELD DETERMINED		6		C											
E				1		LANDSCAPE SPEAKER		FIELD DETERMINED		9		D											
F				1		LANDSCAPE SUBWOOFER		FIELD DETERMINED		1		E											
G		CHIEF PAC526FWP2				DISPLAY LOCATION		60" AFF		3		F											
H												G											
I												H											
J												I											
K												J											
L												K											
M												L											
N												M											
O																							
P																							
Q																							
T																							
U																							
V																							
W																							
X																							
TABLE BOXES												EQUIPMENT RACKS											
A												A		MIDDLE ATLANTIC CWR-26-26VD		0		26RU EQUIPMNET RACK				3	
B												B											
C												C											
D												D											
E												E											
F												F											
G												G											
H												H											
I												I											
J												J											
K												K											
L												L											

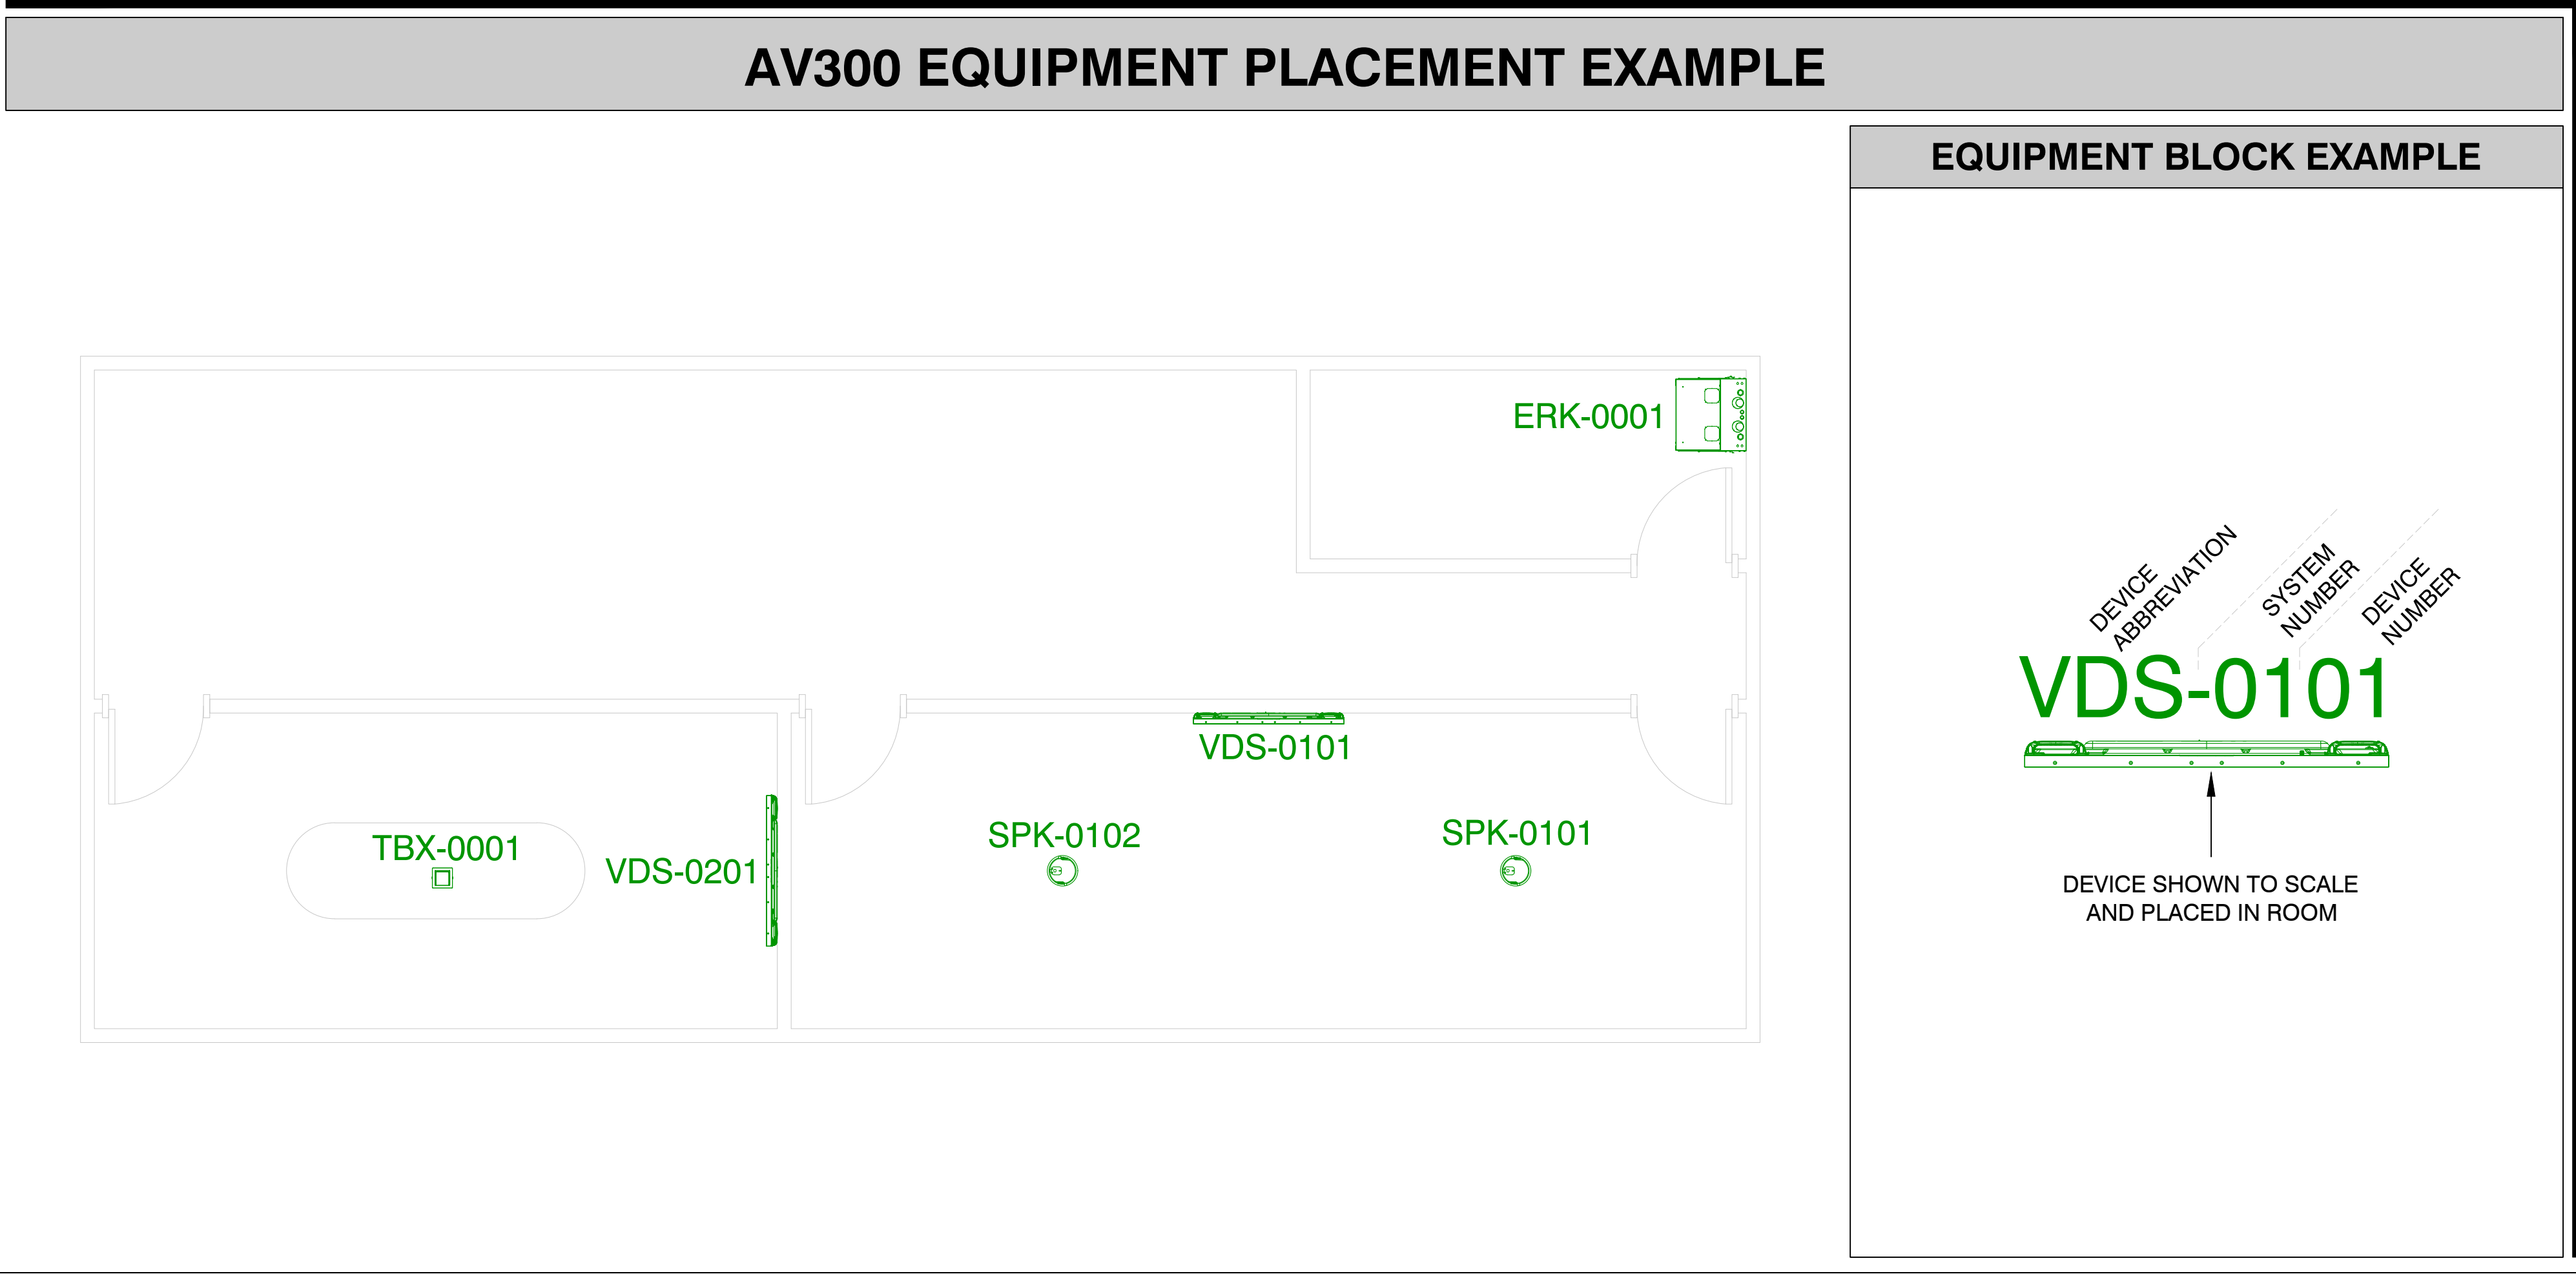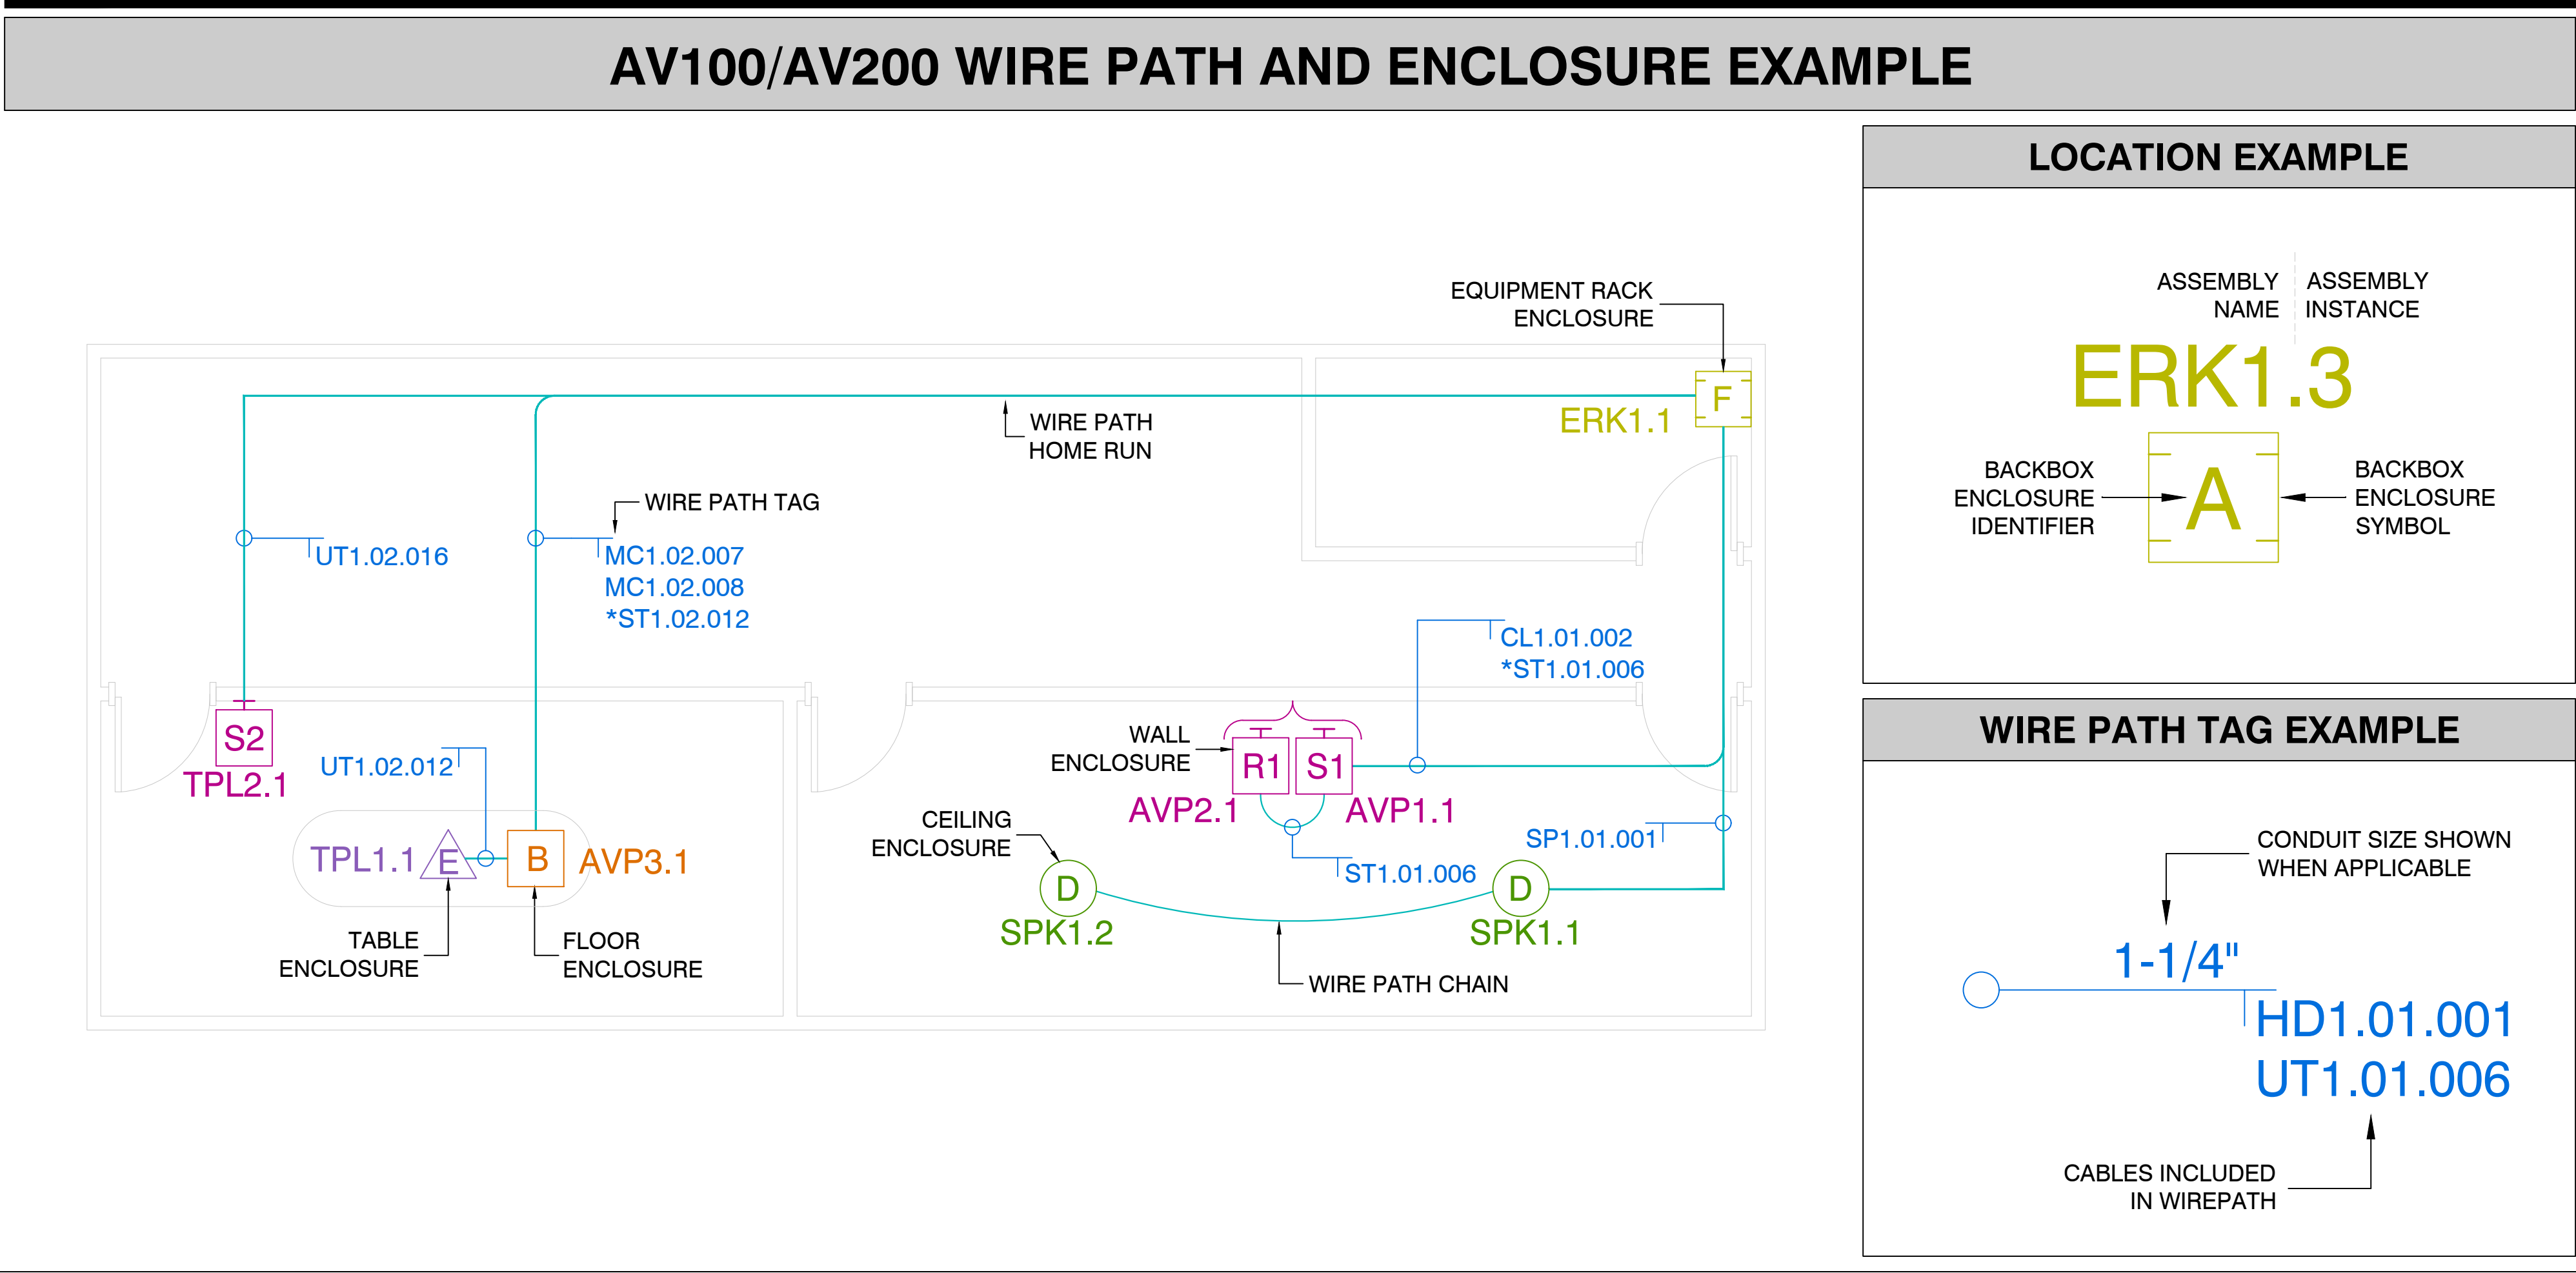

www.marshallind.com

PROJECT INFORMATION
5853
APPELLATION SUN VALLEY
AUDIO VIDEO INTEGRATION
CUSTOMER NAME: HARRIMAN SUN VALLEY HOTEL CUSTOMER NUMBER: APH001
SITE NAME: HARRIMAN SUN VALLEY HOTEL SITE NUMBER: 72388311
SITE ADDRESS: 300 E RIVER ST KETCHUM, ID 83353
SALES PERSON: JEREMY WADDELL ENGINEERED BY: ADAM HANDY
DRAFT: ELI ANDERSON PROJECT MANAGER: JEREMY WADDELL

DRAWING SET INFORMATION
PHASE: CONSTRUCTION
PUBLISH DATE: 6/1/2028
PLOT SIZE: ARCH FULL BLEED E (36.00 X 48.00 INCHES)
PLOT SCALE: 1" = 1'-0"
APPROVED BY: ----


SHEET REVISION INFORMATION
REVISION: REVISION DATE: ----
REVISION DESCRIPTION: ----
REVISION & ISSUE HISTORY
ISSUED FOR: REV. DATE:
1 1 1
2 1 1
ABRV.	DESCRIPTION
AAP	AMPLIFIED AUDIO PANEL
ACP	AUDIO CONTROL PLATE
ACU	ACOUSTIC MATERIAL
ADC	AUDIO CONFERENCING
ALS	ASSISTED LISTENING SYSTEM
AMP	AMPLIFIER
AMS	ASSET MANAGEMENT
ANN	ANNOTATOR
ANT	ANTENNA
ARS	AUDIO RESPONSE SYSTEM
ASP	AUDIO SIGNAL PROCESSOR
AVF	AUDIO/VIDEO FURNITURE
AVL	AUDIO/VIDEO LIFT
AVP	AUDIO/VIDEO PANEL
AVT	AUDIO/VIDEO PANEL
BAG	EQUIPMENT BAG
BGM	BACKGROUND MUSIC SYSTEM
BOB	BREAK OUT BOX
CAM	CAMERA
CBX	CEILING BOX
CCU	CAMERA CONTROL UNIT
CLK	CLOCK
CNT	CONTROLLER
CNV	CONVERTER
COD	ENCODER/DECODER
CPU	COMPUTER
CRD	CARD/MODULE/INSERT
DAR	DIGITAL AUDIO RECORDER
DMP	DIGITAL MEDIA PLAYER
DMR	DIGITAL MEDIA RECORDER
DMT	DIGITAL MEDIA TRANSMISSION
DOC	DOCUMENT CAMERA
DSP	DIGITAL SIGNAGE SYSTEM
DTP	DISTANCE TRANSPORT
DVR	DIGITAL VIDEO RECORDER
DWR	DRAWER
EFX	EFFECTS PROCESSOR
EMI	IR/RF EMITTER
ENC	CHASSIS/CARD ENCLOSURE
ERK	EQUIPMENT RACK
FAN	FAN
FBX	FLOOR BOX
GUI	GRAPHICAL USER INTERFACE
ICS	INTERCOM SYSTEM
IFB	INTERUPTED FOLDBACK
INT	INTERFACE
IWB	WHITE BOARD
KPD	KEYPAD CONTROL
LEN	LENS
LGT	LIGHTING SYSTEM
MDI	MIDI CONTROLLER
MIC	MICROPHONE
MIX	MIXER
MOD	MODULATOR/DEMODULATOR
MON	MONITOR
MSG	MESSAGING SYSTEMS
MSK	SOUND MASKING SYSTEM
MTR	MAGNETIC TAPE RECORDER
NCS	NURSE CALL SYSTEM
NMD	NETWORK MEDIA DEVICE
NVR	NETWORK VIDEO RECORDER
NWD	NETWORK DEVICE
ODR	OPTICAL DISK RECORDER
PAS	PUBLIC ADDRESS SYSTEM

ABRV.	DESCRIPTION
PGS	PAGING SYSTEM
PPL	PATCH PANEL
PRJ	PROJECTOR
PWR	POWER DEVICE
REM	REMOTE CONTROL
RMK	RACK MOUNT KIT
ROB	ROBOTIC SYSTEM
RTS	DISCUSSION SYSTEM
SBX	STAGE BOX/SNAKE
SCN	PROJECTION SCREEN
SCP	PROJECTION SCREEN CONTROL PLATE
SCR	SCALER/SCAN CONVERTER
SNS	SENSOR DEVICE
SOF	SOFTWARE
SPK	SPEAKER
SPT	RF SPLITTER
SWT	SWITCHER
TBX	TABLE BOX
TEL	TELEPHONES
TMP	TAPE MEDIA PLAYER
TPL	TOUCH PANEL
TRX	TRANSMITTER/RECIEVER
UPS	UNINTERRUPTABLE POWER SUPPLY
VDC	VIDEO CONFERENCING
VDS	VIDEO DISPLAY
VSP	VIDEO SIGNAL PROCESSOR
VWS	VIDEO WALL SYSTEM
WAP	WIRELESS ACCESS POINT
WBX	WALL BOX
WMR	WIRELESS TX/RX
XDA	DISTRIBUTION AMPLIFIER
XMR	TRANSFORMER
XXX	UNKNOWN

CABLE LEGEND				
ID	MAKE	MODEL	DESCRIPTION	PLENUM
CL1	WEST PENN	25510BGY	CONTROL	CONTROL CABLE
CL2				
CL3				
CL4				
CL5				
CX1	WEST PENN	2584BK	COAX	ANTENNA CABLE
CX2				
CX3				
CX4				
CX5				
FB1			FIBER OPTIC	
FB2				
FB3				
FB4				
HD1			HDMI	3' HDMI CABLE
HD2				6' HDMI CABLE
HD3				10' HDMI CABLE
HD4				15' HDMI CABLE
HD5				30' HDMI CABLE
HD6				
HD7				
HD8				
MC1	WEST PENN	25291BBK	MICROPHONE OR LINE LEVEL AUDIO	MIC/LINE CABLE
MC2				
MC3				
MC4				
MC5				
MF1			MULTI-FUNCTION	
MF2				
MF3				
MF4				
PW1			POWER	
PW2				
PW3				
PW4				
PW5				
SL1			SPECIAL	
SL2				
SL3				
SL4				
SP1	WEST PENN	25225BGY	SPEAKER	16AWG SPEAKER CABLE
SP2				
SP3				
SP4				
SP5				
ST1	CRESTRON	DM-CBL-8G-P-SP1000	SHIELDED TWISTED PAIR	HDBASET CABLE
ST2				
ST3				
ST4				
ST5				
US1			USB	
US2				
US3				
US4				
US5				
UT1	WEST PENN	254246ABK	UNSHIELDED TWISTED PAIR	DATA CABLE
UT2				
UT3				
UT4				
UT5				

AV800 SINGLE LINE DIAGRAM EXAMPLE

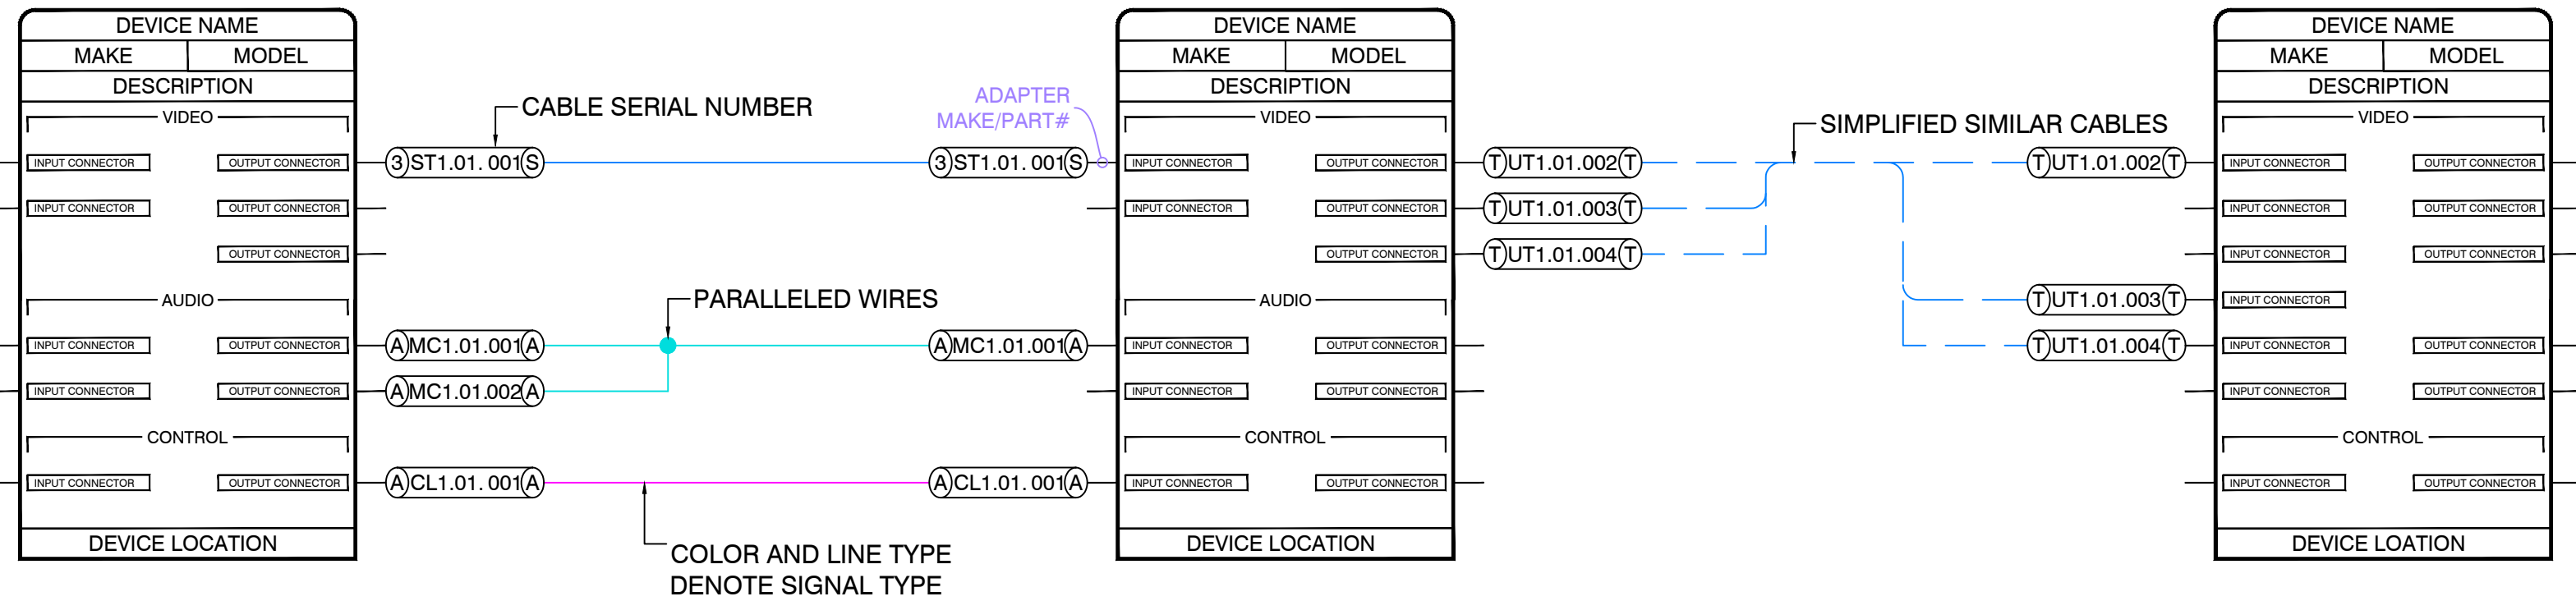

AV800 CABLE SERIAL NUMBER EXAMPLE

FROM NMD-0001/AV803

TO SWT-0002/AV801

CALLOUT TO DETAIL ON AV004

OUTPUT CONNECTOR TYPE

CABLE TYPE

SYSTEM/DRAWING NUMBER

CABLE NUMBER

INPUT CONNECTOR TYPE

SOURCE DEVICE DESIGNATION

SOURCE DEVICE DRAWING

DESTINATION DESIGNATION

DESTINATION DEVICE DRAWING

LINE DESIGNATIONS KEY

BULK - AUDIO

BULK - VIDEO

BULK - CONTROL

BULK - GENERIC

PATCH - AUDIO

PATCH - VIDEO

PATCH - CONTROL

PATCH - GENERIC

AV002

AV000.DWG

SHEET CABLE LEGEND				
ABBREV	MAKE	MODEL	DESCRIPTION	QTY
HD4			15' HDMI CABLE	6
HD5			30' HDMI CABLE	2
MC1	WEST PENN	25291BBK	MIC/LINE CABLE	4
SP1	WEST PENN	25225BGY	16AWG SPEAKER CABLE	2
ST1	CRESTRON	DM-CBL-8G-P-SP1000	HDBASET CABLE	2
UT1	WEST PENN	254246ABK	DATA CABLE	16

SHEET ENCLOSURE LEGEND					
LOCATION	SYM	GANG	DESCRIPTION	ELEVATION	SHEET
AVP3	[B]	3	3" DEEP BACKBOX	SWITCH HEIGHT	AV701
AVP4	[B]				AV701
AVP5	[B]	2	3" DEEP BACKBOX	RECEPTACLE HEIGHT	AV701
AVP6	[B]	3	3" DEEP BACKBOX	SWITCH HEIGHT	AV701
DME1	[B]	1	3" DEEP BACKBOX	+11' AFF	
ERK2	[E]	0	26RU EQUIPMNET RACK		
SPK3	[E]	1	LANDSCAPE SPEAKER	FIELD DETERMINED	
SPK4	[E]	1	LANDSCAPE SUBWOOFER	FIELD DETERMINED	
TP12	[B]	2	3" DEEP BACKBOX	SWITCH HEIGHT	AV701
VDS1	[A]	1	3" DEEP BACKBOX	FIELD DETERMINED	
VDS3	[G]		DISPLAY LOCATION	60" AFF	



PROJECT INFORMATION


5853	
APPELLATION SUN VALLEY	
AUDIO VIDEO INTEGRATION	
CUSTOMER NAME: HARRIMAN SUN VALLEY HOTEL	CUSTOMER NUMBER: APH001
SITE NAME: HARRIMAN SUN VALLEY HOTEL	SITE NUMBER: 72338311
SITE ADDRESS: 300 E RIVER ST KETCHUM, ID 83353	
SALES PERSON: JEREMY WADDELL	ENGINEERED BY: ADAM HANDY
DRAWN BY: ELU ANDERSON	PROJECT MANAGER: JEREMY WADDELL

DRAWING SET INFORMATION

PHASE:	CONSTRUCTION
PUBLISH DATE:	5/18/2028
PLOT SIZE:	ARCH FULL BLEED E (36.00 X 48.00 INCHES)
PLOT SCALE:	1" = 1'-0"
APPROVED BY:	----

SHEET REVISION INFORMATION

REVISION	REVISION DATE	REVISION DESCRIPTION
----	----	----
REVISION & ISSUE HISTORY		
ISSUED FOR:	REV.	DATE:
1		
2		
3		
4		
5		
6		
7		
8		
9		
10		

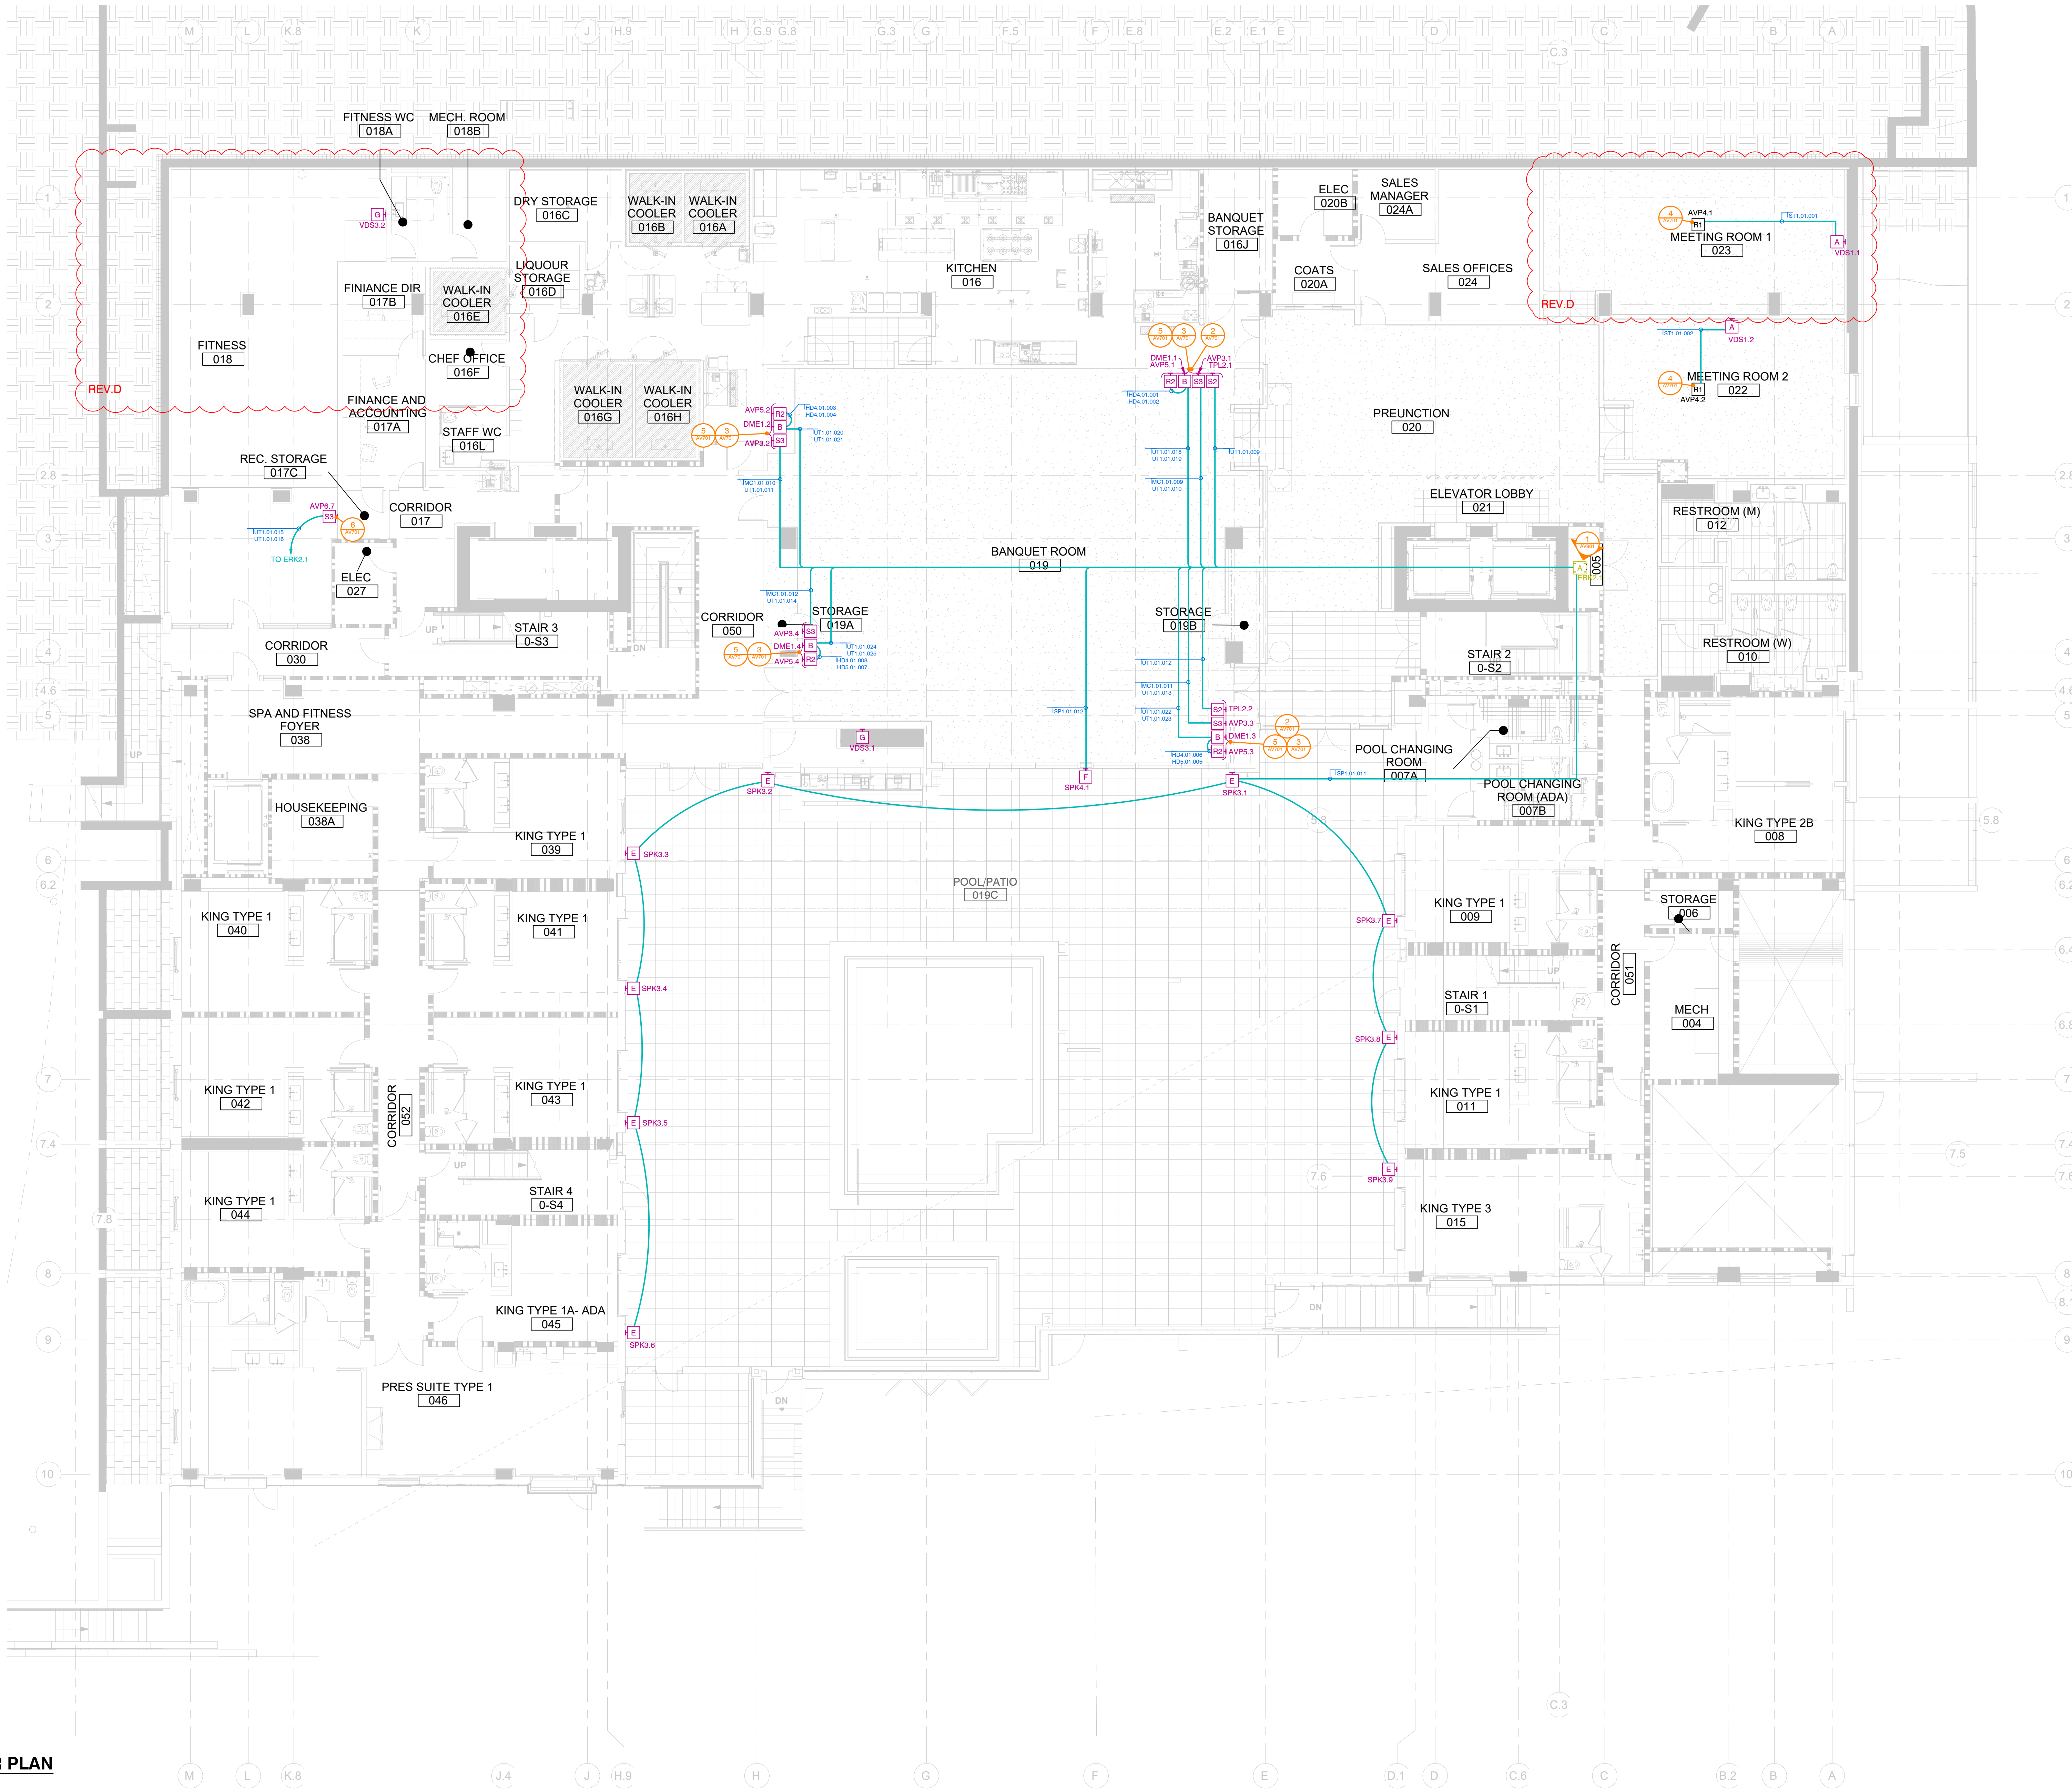

APPELLATION SUN VALLEY
WIREPATH AND BACKBOXES
LEVEL 1

AV102

SHEET CABLE LEGEND				
ABBREV	MAKE	MODEL	DESCRIPTION	QTY
SP1	WEST PENN	25225BGY	16AWG SPEAKER CABLE	2
ST1	CRESTRON	DM-CBL-8G-P-SP1000	HDBASET CABLE	2
UT1	WEST PENN	254246ABK	DATA CABLE	11

SHEET ENCLOSURE LEGEND					
LOCATION	SYM	GANG	DESCRIPTION	ELEVATION	SHEET
AVP4	[Symbol]	1	3" DEEP BACKBOX	RECEPTACLE HEIGHT	AV701
AVP6	[Symbol]	3	3" DEEP BACKBOX	SWITCH HEIGHT	AV701
ERK3	[Symbol]	0	26RU EQUIPMNET RACK		
SPK6	[Symbol]	1	SPEAKER LOCATION	FIELD DETERMINED	
TPL1	[Symbol]	2	3" DEEP BACKBOX	SWITCH HEIGHT	AV701
VDS1	[Symbol]	1	3" DEEP BACKBOX	FIELD DETERMINED	



PROJECT INFORMATION


5853	
APPELLATION SUN VALLEY	
AUDIO VIDEO INTEGRATION	
CUSTOMER NAME:	HARRIMAN SUN VALLEY HOTEL
CUSTOMER NUMBER:	APH001
SITE NAME:	HARRIMAN SUN VALLEY HOTEL
SITE NUMBER:	72388311
SITE ADDRESS:	300 E RIVER ST KETCHUM, ID 83353
SALES PERSON:	JEREMY WADDELL
ENGINEERED BY:	ADAM HANDY
DRAWN:	ELI ANDERSON
PROJECT MANAGER:	JEREMY WADDELL

DRAWING SET INFORMATION

PHASE:	CONSTRUCTION
PUBLISH DATE:	5/18/2028
PLOT SIZE:	ARCH FULL BLEED E (36.00 X 48.00 INCHES)
PLOT SCALE:	1" = 1'-0"
APPROVED BY:	----

SHEET REVISION INFORMATION

REVISION	REVISION DATE	----
----	REVISION DESCRIPTION	----
REVISION & ISSUE HISTORY		
ISSUED FOR:	REV.	DATE:
1		
2		
3		
4		
5		
6		
7		
8		
9		
10		

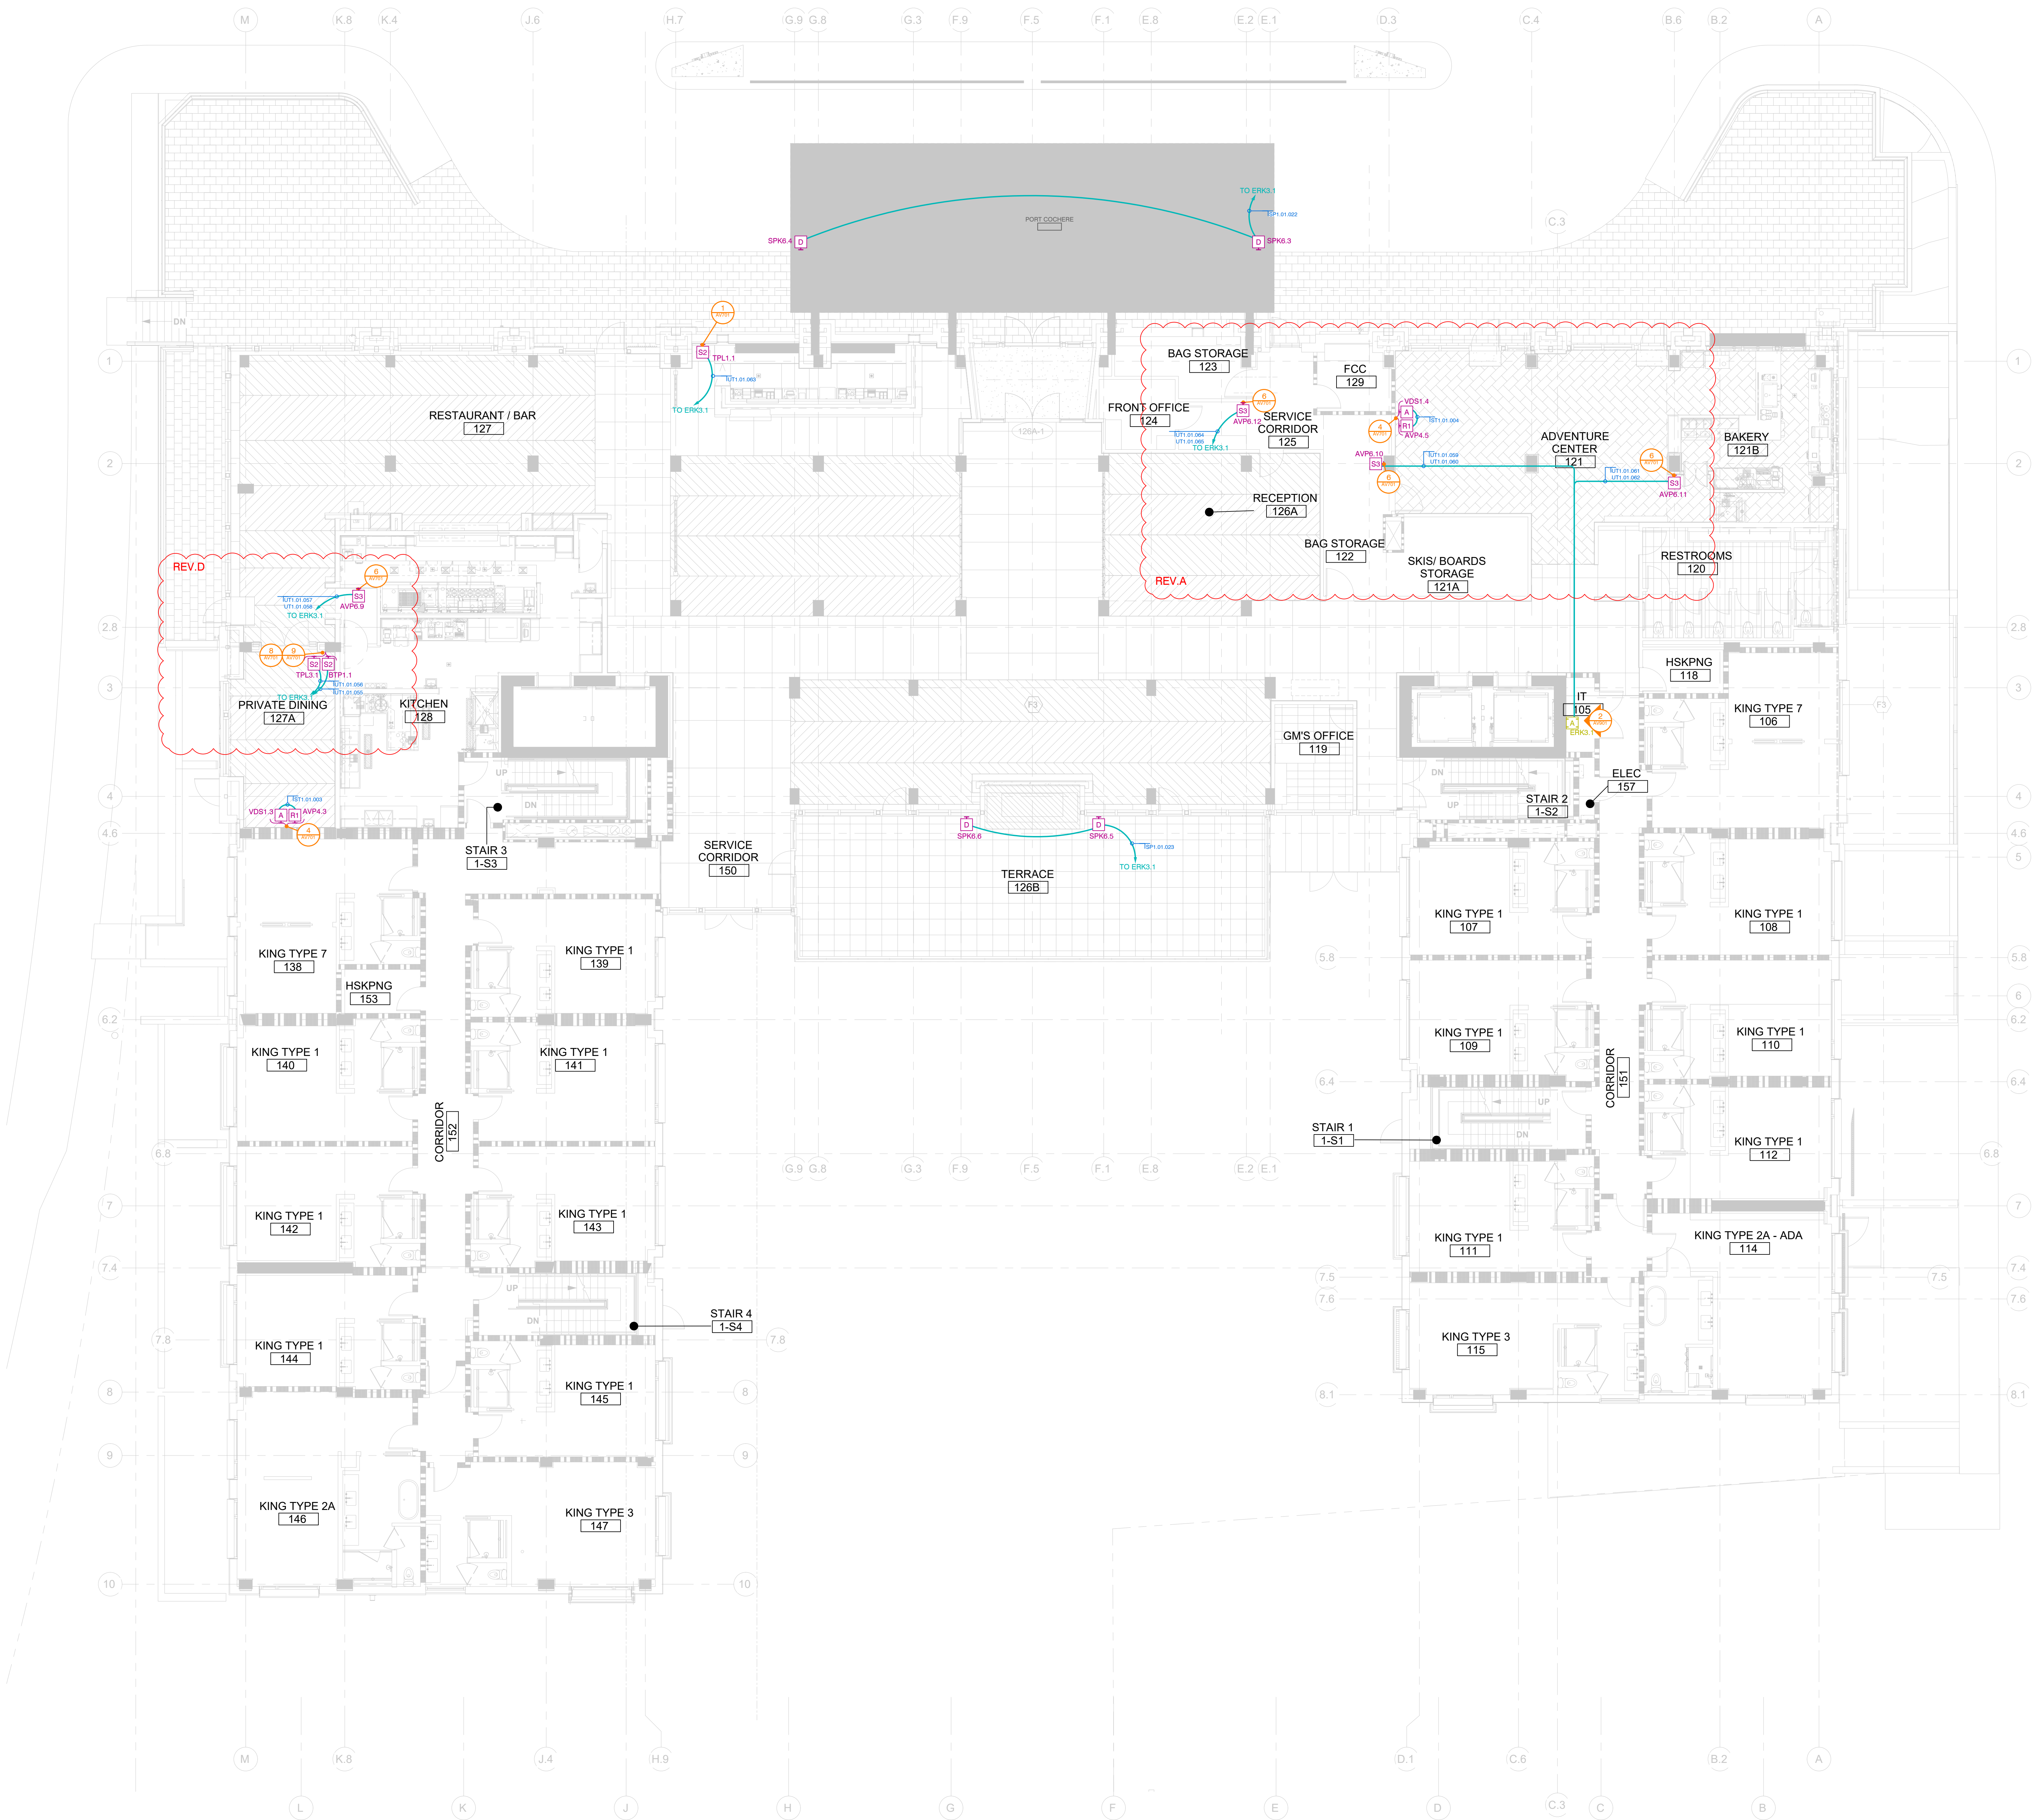

1 SECOND LEVEL - FLOOR PLAN
SCALE: 1/8" = 1'-0"

APPELLATION SUN VALLEY
WIREPATH AND BACKBOXES
LEVEL 2

AV103

SHEET CABLE LEGEND				
ABBREV	MAKE	MODEL	DESCRIPTION	QTY
SP1	WEST PENN	25225BGY	16AWG SPEAKER CABLE	11

SHEET ENCLOSURE LEGEND					
LOCATION	SYM	GANG	DESCRIPTION	ELEVATION	SHEET
ERK1		0	26RU EQUIPMNET RACK		AV901
SPK1		0	6" SELF ENCLOSED SPEAKER	FLUSH IN CEILING	1



PROJECT INFORMATION


5853	
APPELLATION SUN VALLEY	
AUDIO VIDEO INTEGRATION	
CUSTOMER NAME:	APPH001
CUSTOMER NUMBER:	72338311
SITE NAME:	300 E RIVER ST
SITE ADDRESS:	KETCHUM, ID 83353
SALES PERSON:	ENGINEERED BY:
DESIGNED BY:	ADAM HANDY
DRAWN BY:	PROJECT MANAGER:
ELI ANDERSON	JEREMY WADDELL

DRAWING SET INFORMATION

PHASE:	CONSTRUCTION
PUBLISH DATE:	5/18/2028
PLOT SIZE:	ARCH FULL BLEED E (36.00 X 48.00 INCHES)
PLOT SCALE:	1" = 1'-0"
APPROVED BY:	

SHEET REVISION INFORMATION

REVISION	REVISION DATE	
----	REVISION DESCRIPTION	
REVISION & ISSUE HISTORY		
ISSUED FOR:	REV.	DATE:
1		
2		
3		
4		
5		
6		
7		
8		
9		
10		

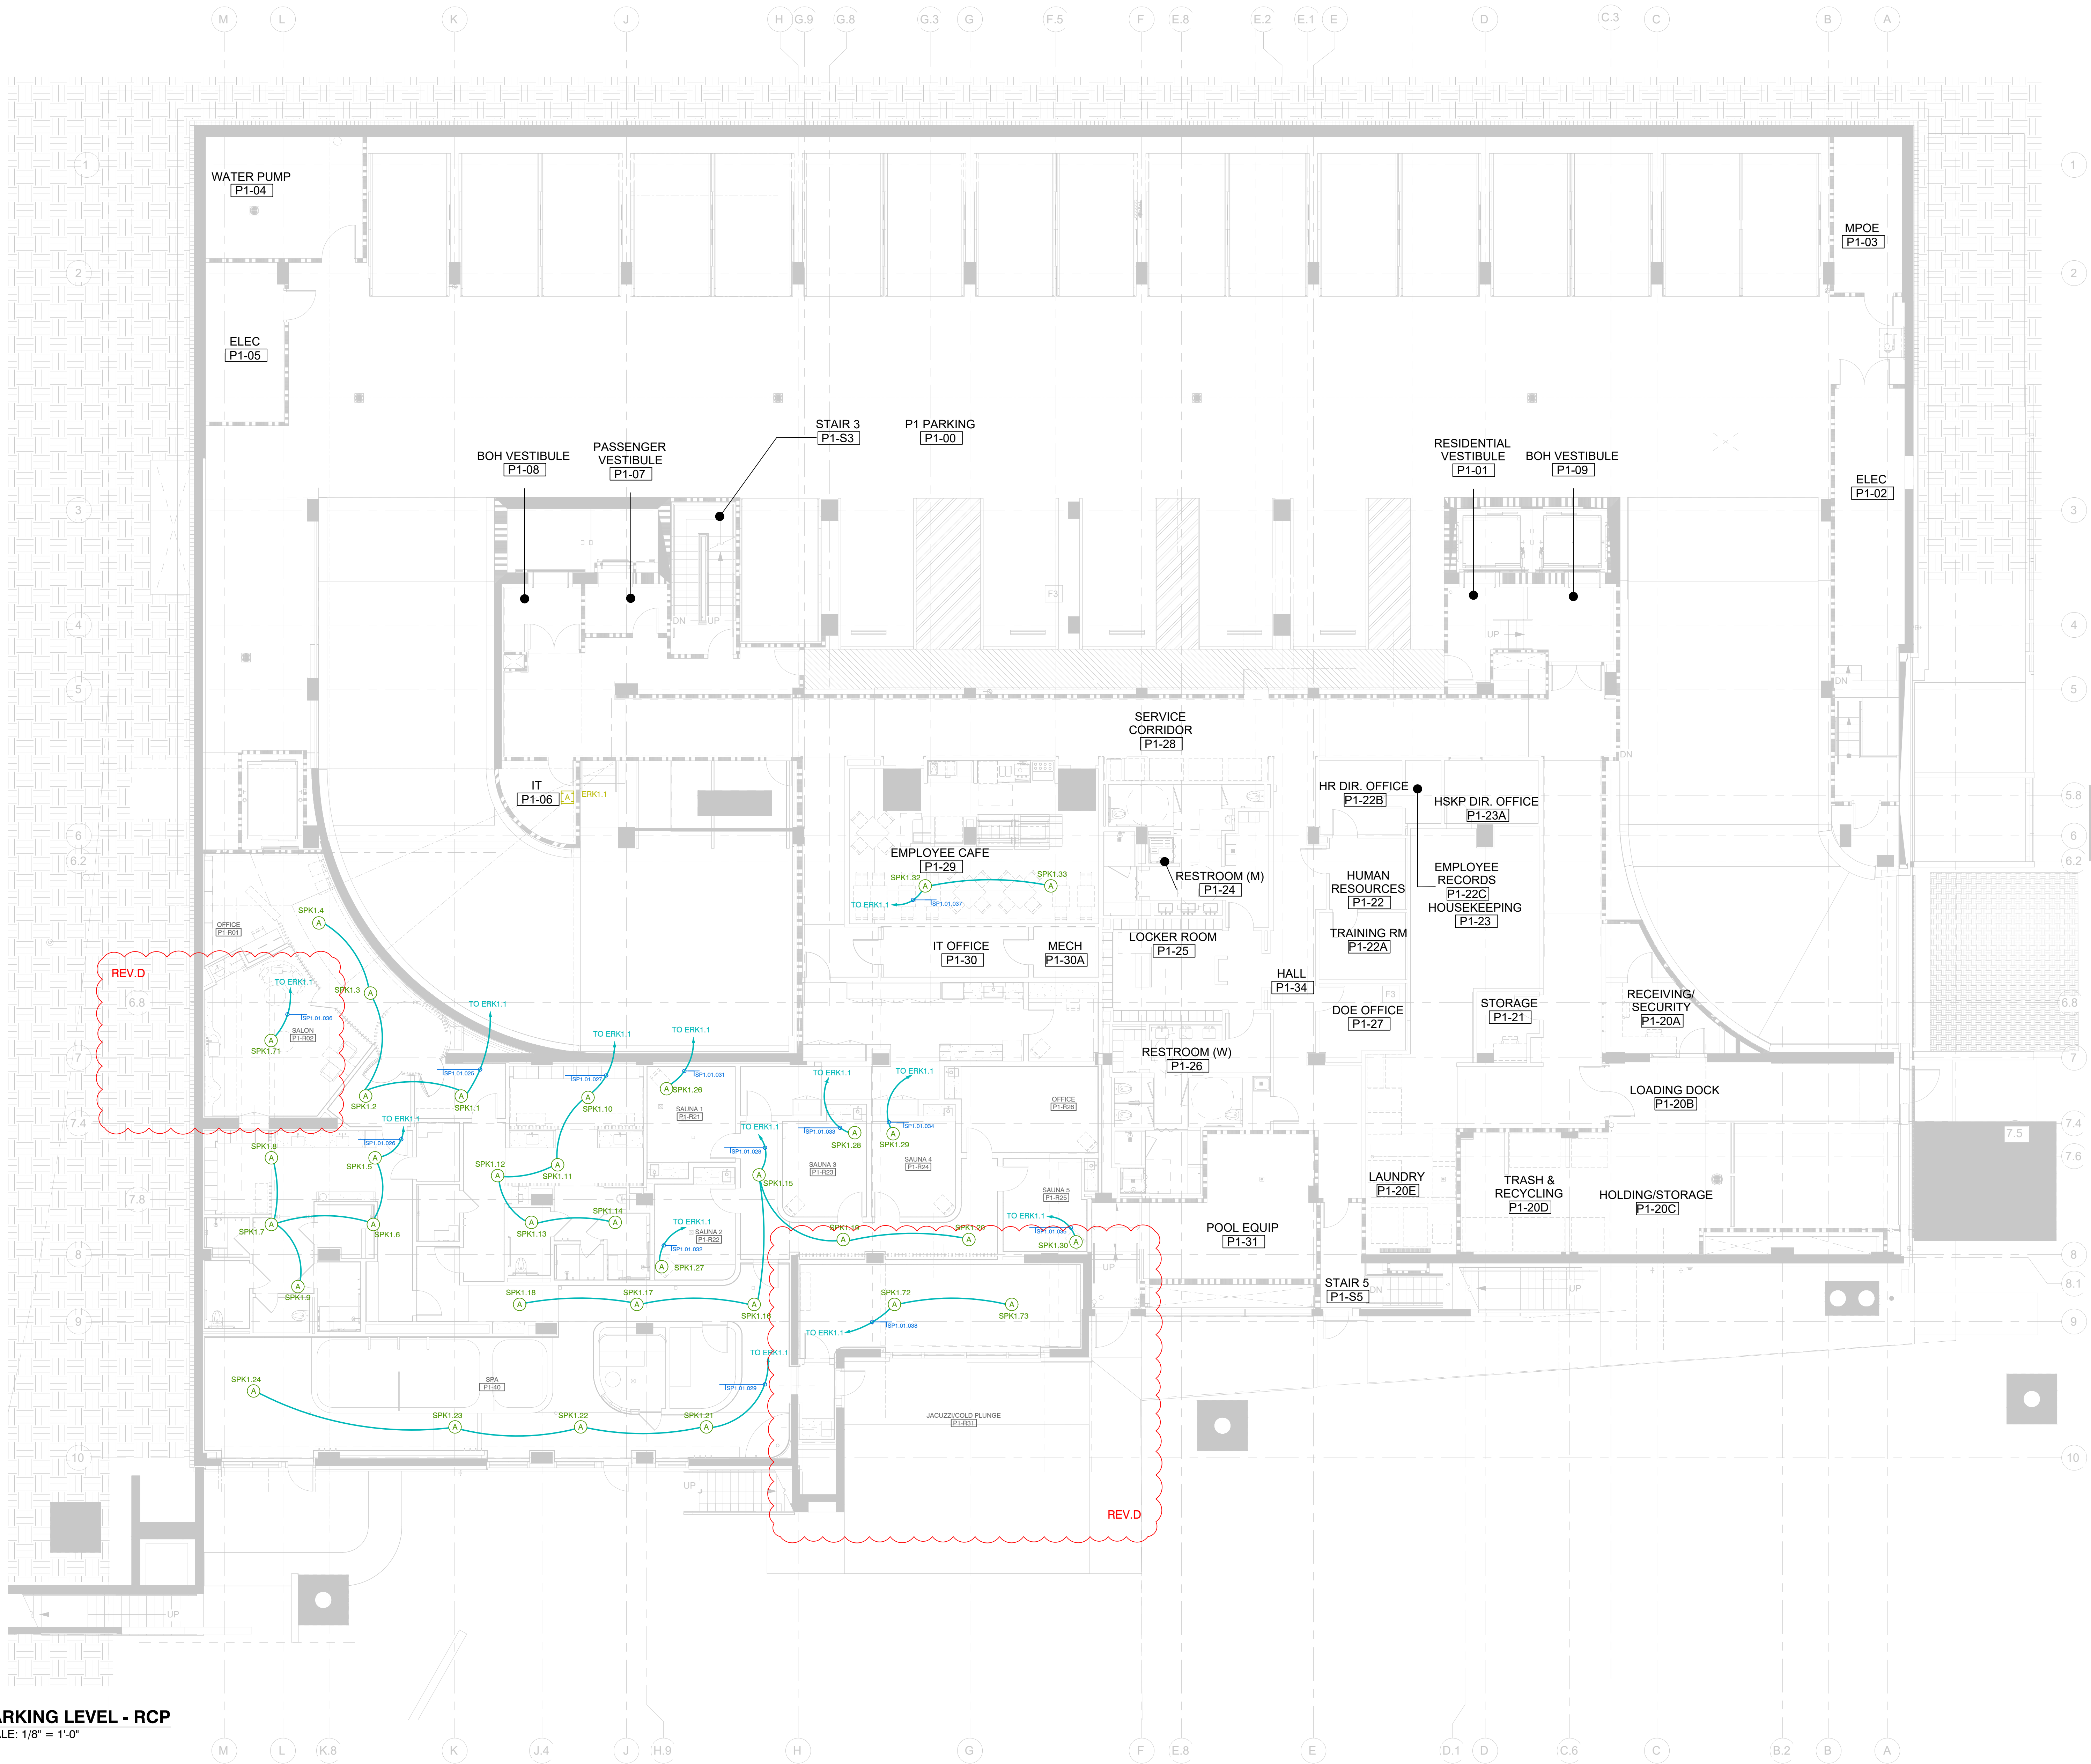


1
N
PARKING LEVEL - RCP
SCALE: 1/8" = 1'-0"

APPELLATION SUN VALLEY
REFLECTED CEILING
LEVEL P1

AV201

FILE NAME: AV100.DWG

SHEET ENCLOSURE LEGEND						
LOCATION	SYM	GANG	DESCRIPTION	ELEVATION	SHEET	DETAIL
ERK2	A	0	26RU EQUIPMNET RACK			
SPK1	A	0	6" SELF ENCLOSED SPEAKER	FLUSH IN CEILING		
SPK2	B	0	8" SELF ENCLOSED SUBWOOFER	FLUSH IN CEILING		

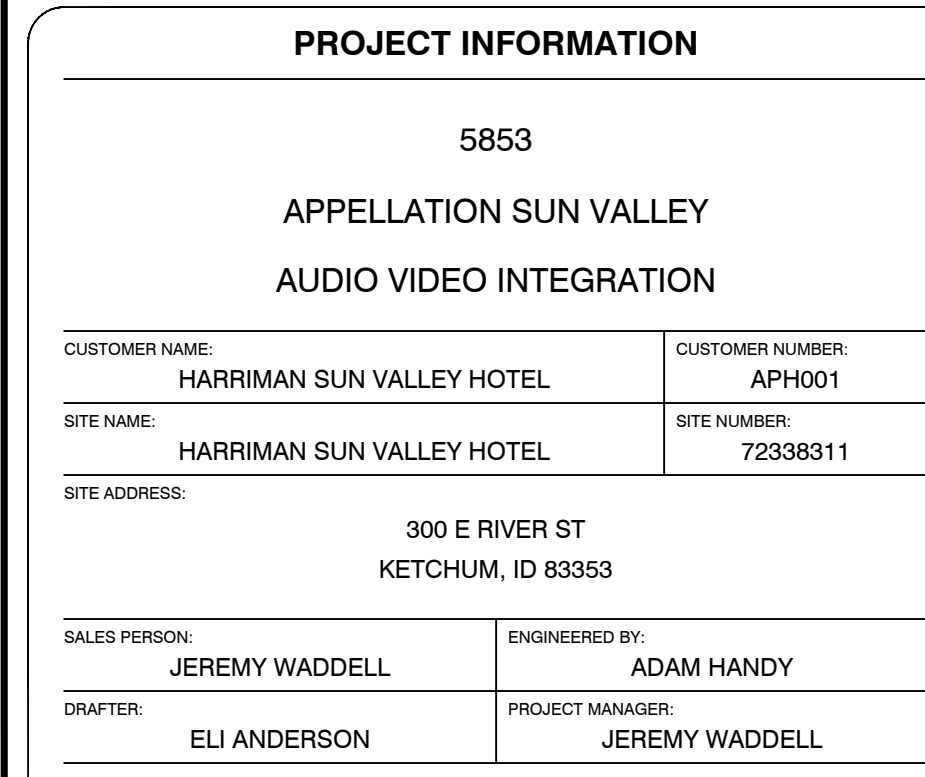

DRAWING SET INFORMATION	
PHASE:	CONSTRUCTION
PUBLISH DATE:	5/18/2026
PLOT SIZE:	ARCH FULL BLEED E (36.00 X 48.00 INCHES)
PLOT SCALE:	1" = 1'-0"
APPROVED BY:	

[illegible]

APPELLATION SUN VALLEY

REFLECTED CEILING

LEVEL 1

AV202

FILE NAME: AV100.DWG

SHEET CABLE LEGEND				
ABBREV	MAKE	MODEL	DESCRIPTION	QTY
SP1	WEST PENN	25225BGY	16AWG SPEAKER CABLE	9

SHEET ENCLOSURE LEGEND					
LOCATION	SYM	GANG	DESCRIPTION	ELEVATION	SHEET
ERK3		0	26RU EQUIPMNET RACK		
SPK1		0	6\"/>	FLUSH IN CEILING	
SPK2		0	8\"/>	FLUSH IN CEILING	



PROJECT INFORMATION

5853	
APPELLATION SUN VALLEY	
AUDIO VIDEO INTEGRATION	
CUSTOMER NAME:	HARRIMAN SUN VALLEY HOTEL
CUSTOMER NUMBER:	APH001
SITE NAME:	HARRIMAN SUN VALLEY HOTEL
SITE NUMBER:	72388311
SITE ADDRESS:	300 E RIVER ST KETCHUM, ID 83353
SALES PERSON:	JEREMY WADDELL
ENGINEERED BY:	ADAM HANDY
DRAWN BY:	ELI ANDERSON
PROJECT MANAGER:	JEREMY WADDELL

DRAWING SET INFORMATION

PHASE:	CONSTRUCTION
PUBLISH DATE:	5/18/2028
PLOT SIZE:	ARCH FULL BLEED E (36.00 X 48.00 INCHES)
PLOT SCALE:	1" = 1'-0"
APPROVED BY:	----

SHEET REVISION INFORMATION

REVISION	REVISION DATE	REVISION DESCRIPTION
----	----	----
REVISION & ISSUE HISTORY		
ISSUED FOR:	REV.	DATE:
1		
2		
3		
4		
5		
6		
7		
8		
9		
10		




1 SECOND LEVEL - RCP
SCALE: 1/8" = 1'-0"

APPELLATION SUN VALLEY
REFLECTED CEILING
LEVEL 2


AV203

DESIGNATION	DESCRIPTION	LOCATION
TPL-0101	TOUCH PANEL	TPL1.1

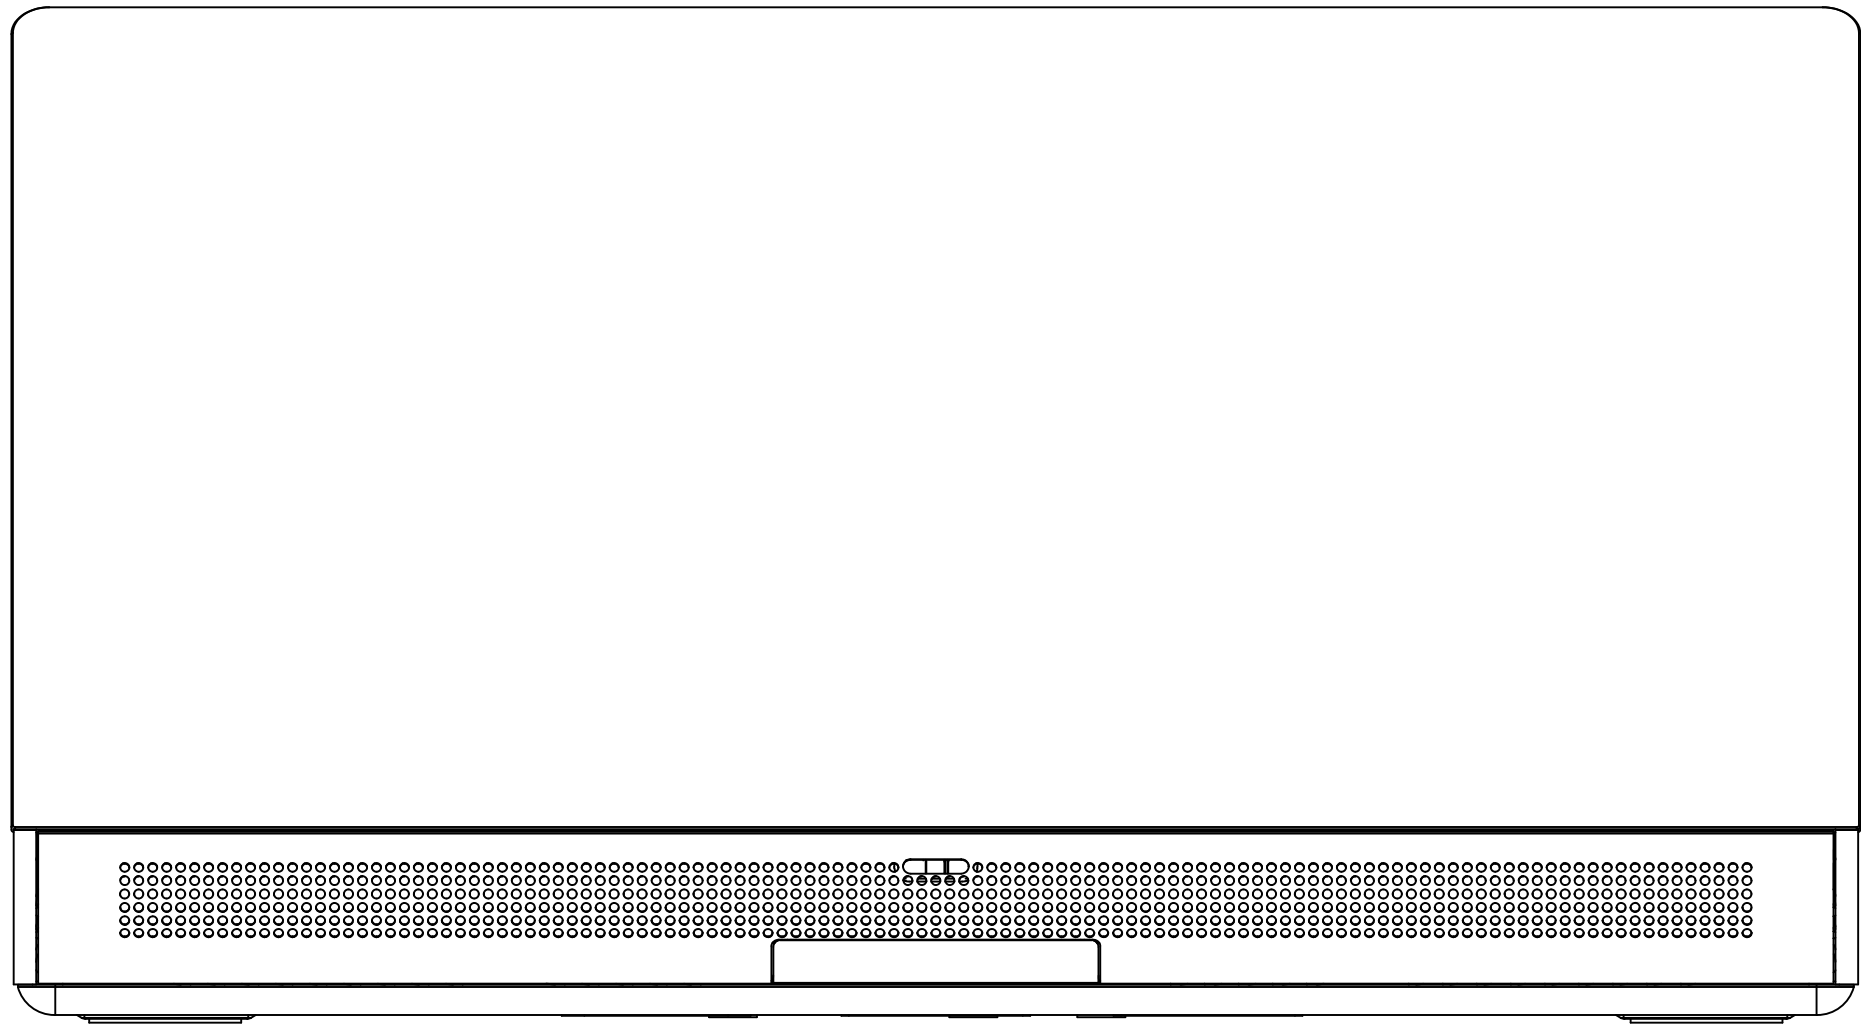


1 **TPL1**
CRESTRON TS-1070
SCALE: 1" = 1'-0"

DESIGNATION	DESCRIPTION	LOCATION
TPT-0101	MEETING ROOM 1 DM TX	AVP4.1
TPT-0102	MEETING ROOM 2 DM TX	AVP4.2
TPT-0103	PRIVATE DINING DM TX	AVP4.3
TPT-0104	PRIVATE DINING DM TX	AVP4.5
TPT-0105	EMPLOYEE CAFE DM TX	AVP4.4

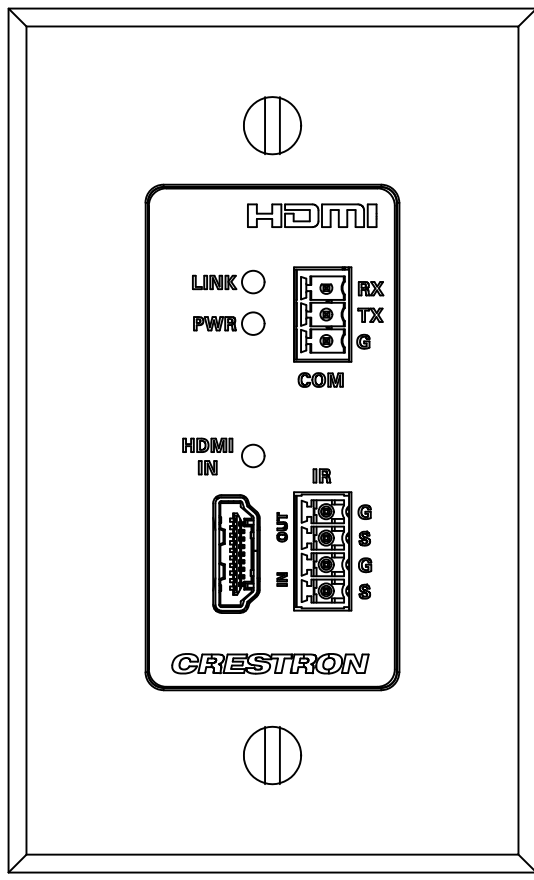


4 **AVP4**
CRESTRON HD-TXC-4KZ-101-1G-W
SCALE: 1" = 1'-0"

DESIGNATION	DESCRIPTION	LOCATION
CNT-0102	SALON CONTROLLER	KPD1.1

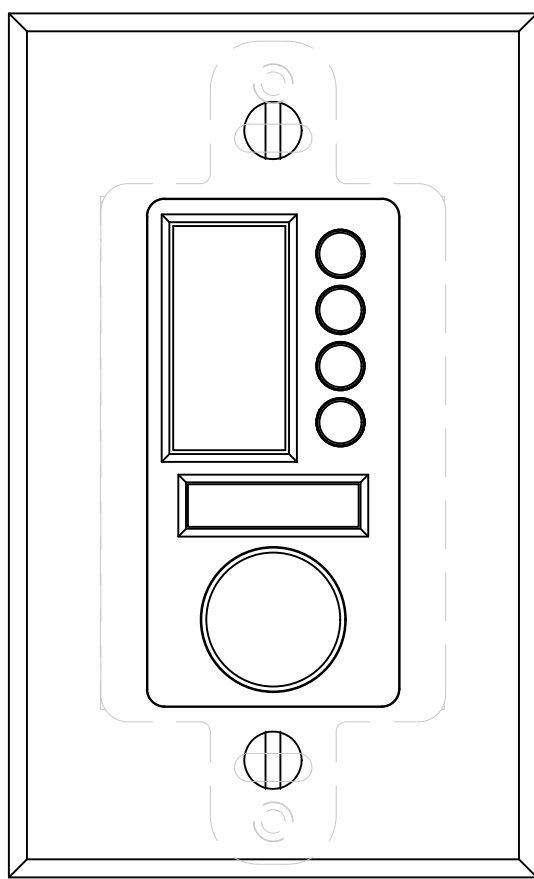


7 **KPD1**
SYMETRIX 80-0171
SCALE: 1" = 1'-0"

DESIGNATION	DESCRIPTION	LOCATION
TPL-0102	TOUCH PANEL	TPL2.1
TPL-0103	TOUCH PANEL	TPL2.2

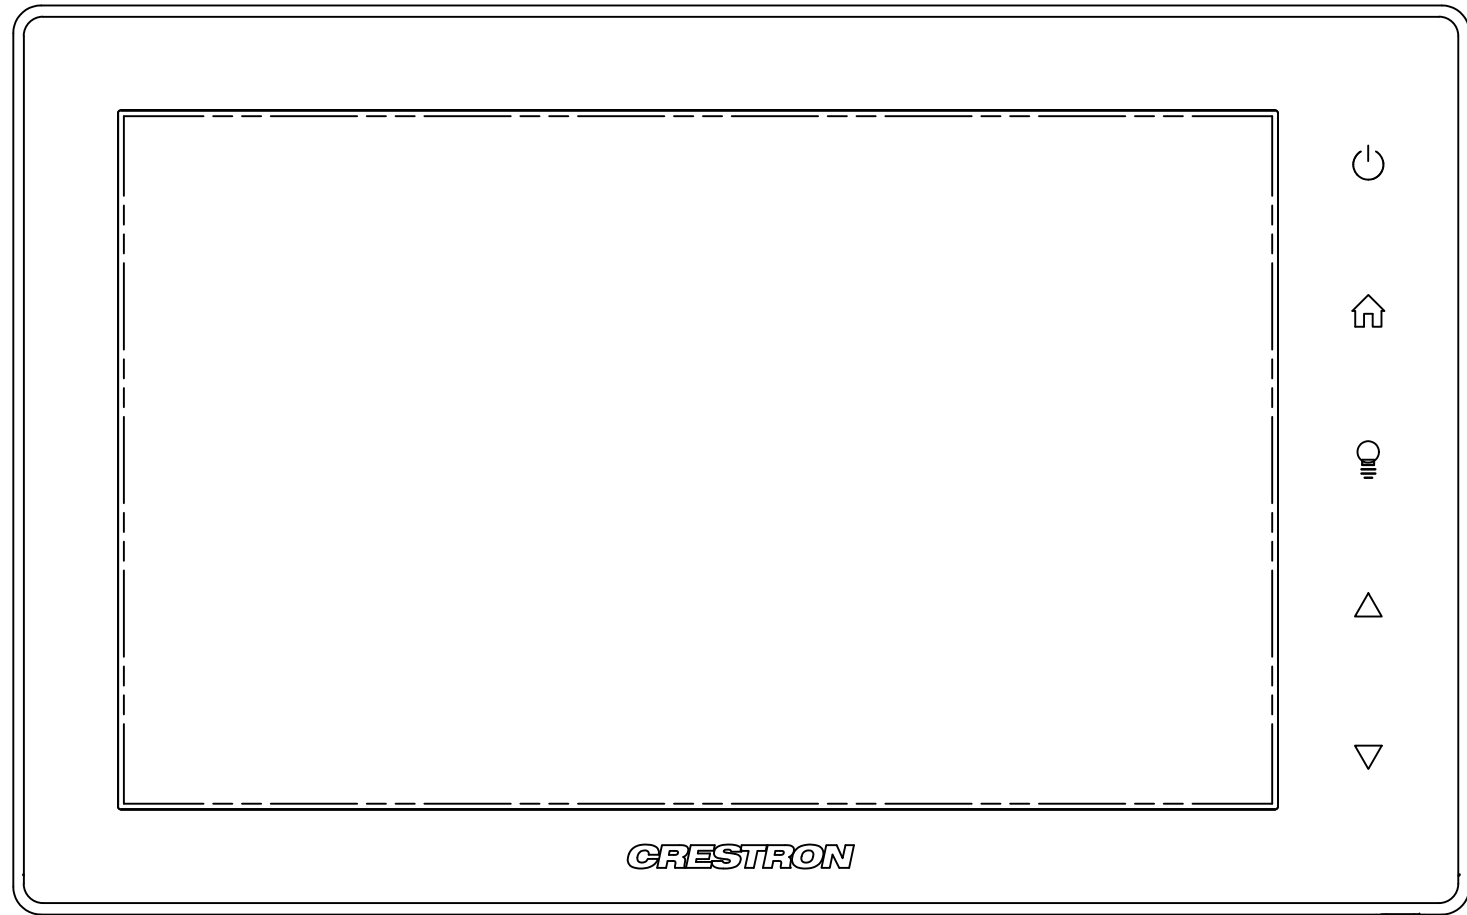


2 **TPL2**
CRESTRON TSW-750-W-S
SCALE: 1" = 1'-0"

DESIGNATION	DESCRIPTION	LOCATION
AVP-0111	BANQUET NORTH HDMI INPUT	AVP5.1
AVP-0112	BANQUET NORTH HDMI OUTPUT	AVP5.1
AVP-0113	BANQUET NORTH HDMI INPUT	AVP5.2
AVP-0114	BANQUET NORTH HDMI OUTPUT	AVP5.2
AVP-0115	HDMI INPUT	AVP5.3
AVP-0116	HDMI OUTPUT	AVP5.3
AVP-0117	BANQUET SOUTH HDMI INPUT	AVP5.4
AVP-0118	BANQUET SOUTH HDMI OUTPUT	AVP5.4

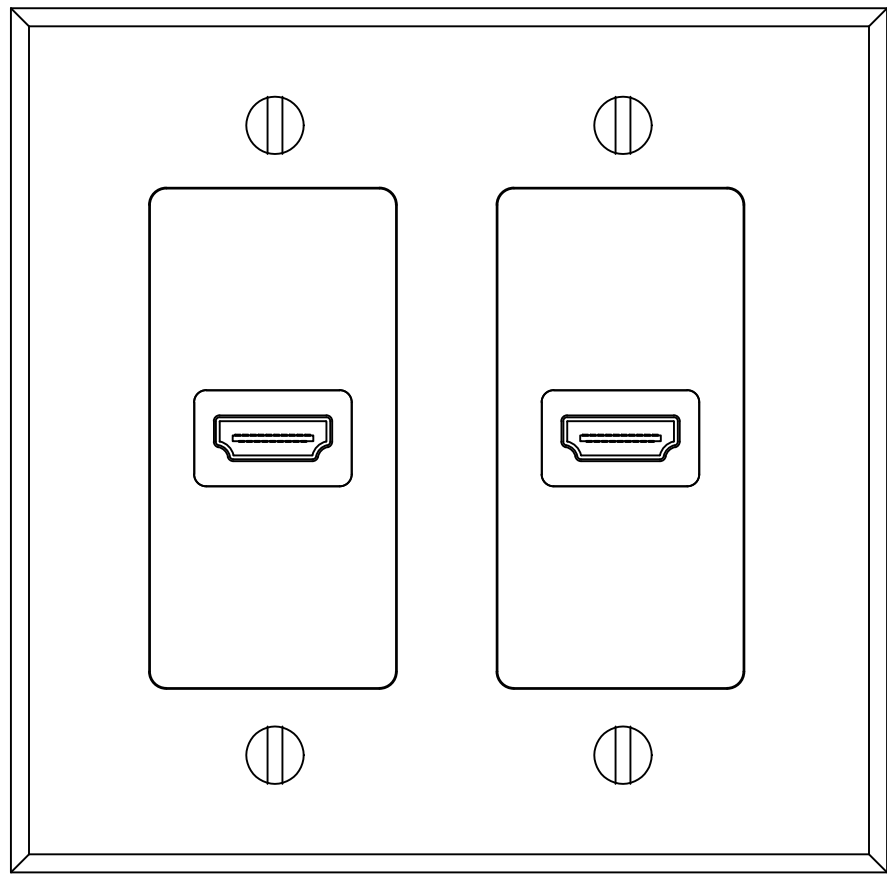


5 **AVP5**
DUAL C2G 41043 FOR HDMI INPUT/OUTPUT
SCALE: 1" = 1'-0"

DESIGNATION	DESCRIPTION	LOCATION
TPL-0105	PRIVATE DINING TOUCH PANEL	TPL3.1

 


8 **TPL3**
CRESTRON TSW-770-B-S
SCALE: 1" = 1'-0"

DESIGNATION	DESCRIPTION	LOCATION
AVP-0101	PRIVATE DINING BLUETOOTH RX	BTP1.1

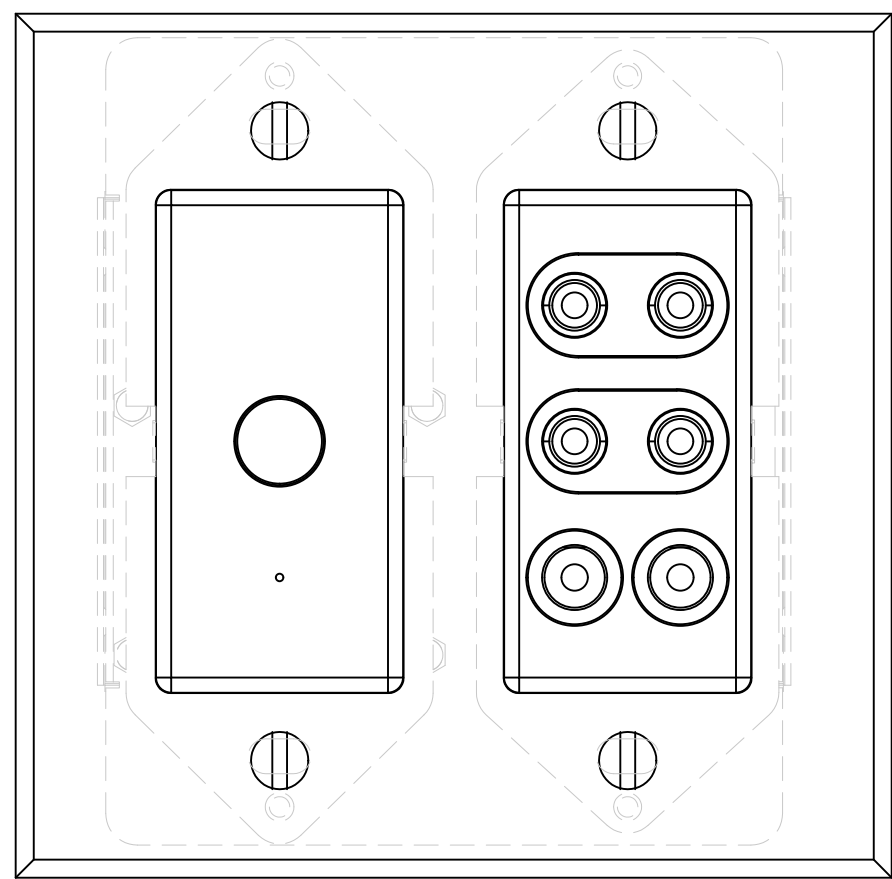


9 **BTP1**
SYMETRIX XIO BLUETOOTH RCA-3.5
SCALE: 1" = 1'-0"

DESIGNATION	DESCRIPTION	LOCATION
AVP-0106	BANQUET NORTH BLUETOOTH RX	AVP3.1
MIP-0101	BANQUET NORTH AUX AUDIO	AVP3.1
AVP-0107	BANQUET NORTH BLUETOOTH RX	AVP3.2
MIP-0102	BANQUET NORTH AUX AUDIO	AVP3.2
AVP-0108	BANQUET SOUTH BLUETOOTH RX	AVP3.3
MIP-0103	BANQUET SOUTH AUX AUDIO	AVP3.3
AVP-0109	BANQUET SOUTH BLUETOOTH RX	AVP3.4
MIP-0104	BANQUET SOUTH AUX AUDIO	AVP3.4

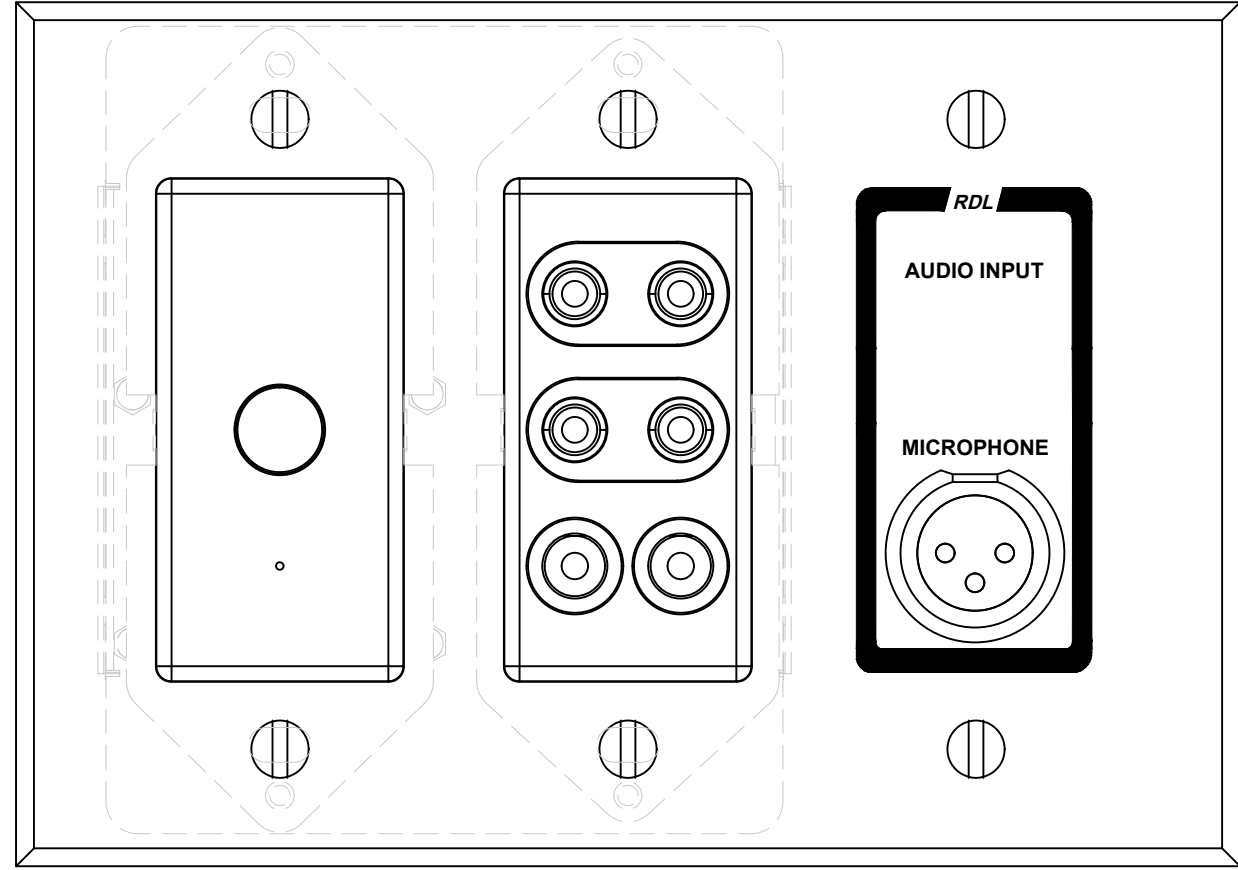

3 **AVP3**
DUAL C2G 41043 FOR HDMI INPUT/OUTPUT
SCALE: 1" = 1'-0"

DESIGNATION	DESCRIPTION	LOCATION
AVP-0121	SAUNA 1 BLUETOOTH RX	AVP6.2
CNT-0103	SAUNA 1 CONTROLLER	AVP6.2
AVP-0122	SAUNA 2 BLUETOOTH RX	AVP6.3
CNT-0104	SAUNA 2 CONTROLLER	AVP6.3
AVP-0123	SAUNA 3 BLUETOOTH RX	AVP6.4
CNT-0105	SAUNA 3 CONTROLLER	AVP6.4
AVP-0124	SAUNA 4 BLUETOOTH RX	AVP6.5
CNT-0106	SAUNA 4 CONTROLLER	AVP6.5
AVP-0125	SAUNA 5 BLUETOOTH RX	AVP6.6
CNT-0107	SAUNA 5 CONTROLLER	AVP6.6
AVP-0105	FITNESS BLUETOOTH RX	AVP6.7
CNT-0108	FITNESS CONTROLLER	AVP6.7
AVP-0102	RESTAURANT AND BAR BLUETOOTH RX	AVP6.9
CNT-0110	RESTAURANT AND BAR CONTROLLER	AVP6.9
AVP-0103	ADVENTURE CLUB BLUETOOTH RX	AVP6.10
CNT-0111	ADVENTURE CLUB CONTROLLER	AVP6.10
AVP-0104	BAKERY BLUETOOTH RX	AVP6.11
CNT-0112	BAKERY CONTROLLER	AVP6.11
AVP-0126	SERVICE CORRIDOR BLUETOOTH RX	AVP6.12
CNT-0114	SERVICE CORRIDOR CONTROLLER	AVP6.12

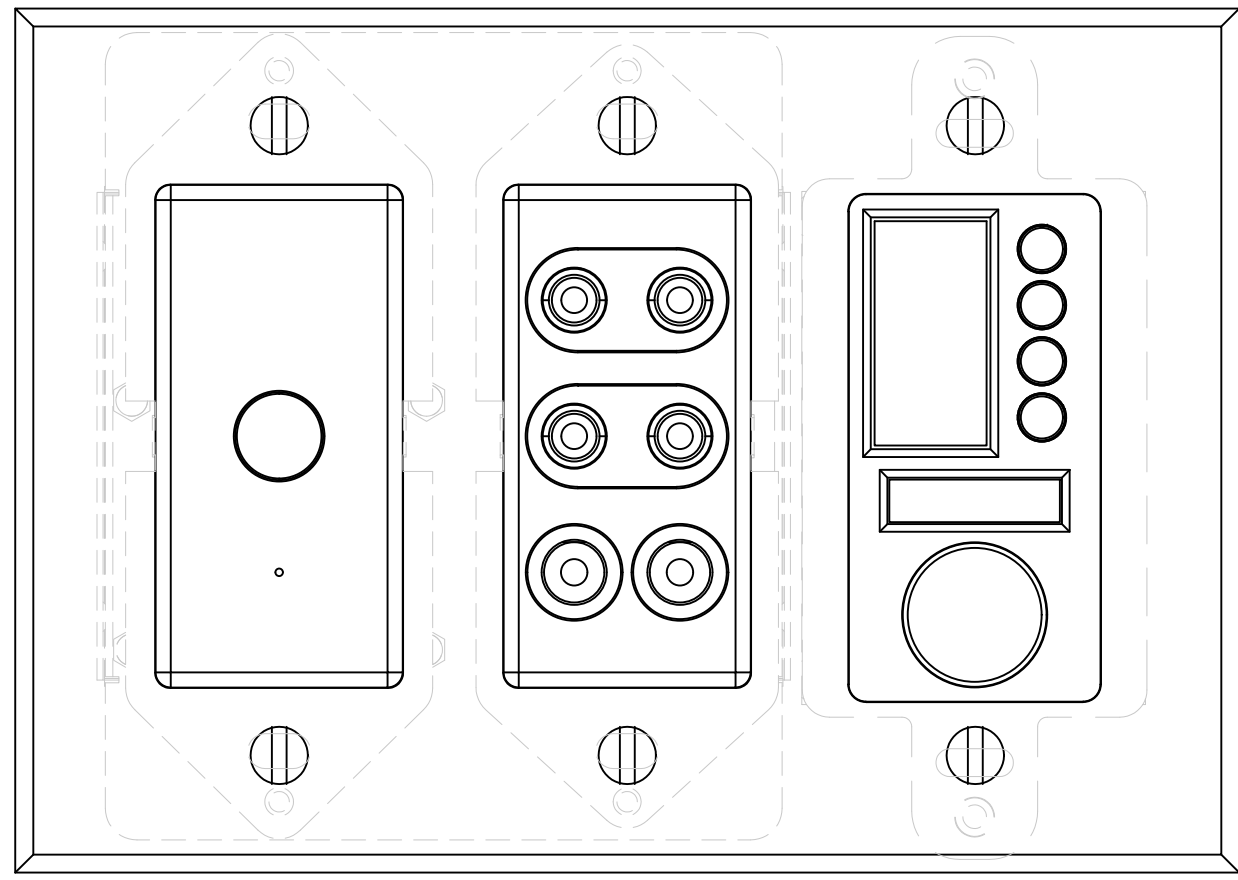

6 **AVP6**
SYMETRIX XIO BLUETOOTH RCA-3.5 WITH SYMETRIX 80-0171
SCALE: 1" = 1'-0"



www.marshallind.com

PROJECT INFORMATION

5853

APPELLATION SUN VALLEY
AUDIO VIDEO INTEGRATION

CUSTOMER NAME:	HARRIMAN SUN VALLEY HOTEL	CUSTOMER NUMBER:	APH001
SITE NAME:	HARRIMAN SUN VALLEY HOTEL	SITE NUMBER:	72358311

SITE ADDRESS:
300 E RIVER ST
KETCHUM, ID 83353

SALES PERSON:	JEREMY WADDELL	ENGINEERED BY:	ADAM HANDY
DRAWN:	ELI ANDERSON	PROJECT MANAGER:	JEREMY WADDELL

DRAWING SET INFORMATION

PHASE:	CONSTRUCTION
PUBLISH DATE:	5/18/2008
PLOT SIZE:	ARCH FULL BLEED E (36.00 X 48.00 INCHES)
PLOT SCALE:	1" = 1'-0"
APPROVED BY:	----

SHEET REVISION INFORMATION

REVISION	REVISION DATE	----
----	REVISION DESCRIPTION	----

REVISION & ISSUE HISTORY	REV.	DATE:
ISSUED FOR:		
1		
2		
3		
4		
5		
6		
7		
8		
9		
10		
11		
12		
13		
14		
15		
16		
17		
18		
19		
20		


APPELLATION SUN VALLEY

PLATE DETAILS

UTILIZED PLATES

AV701

FILE NAME: AV700.DWG

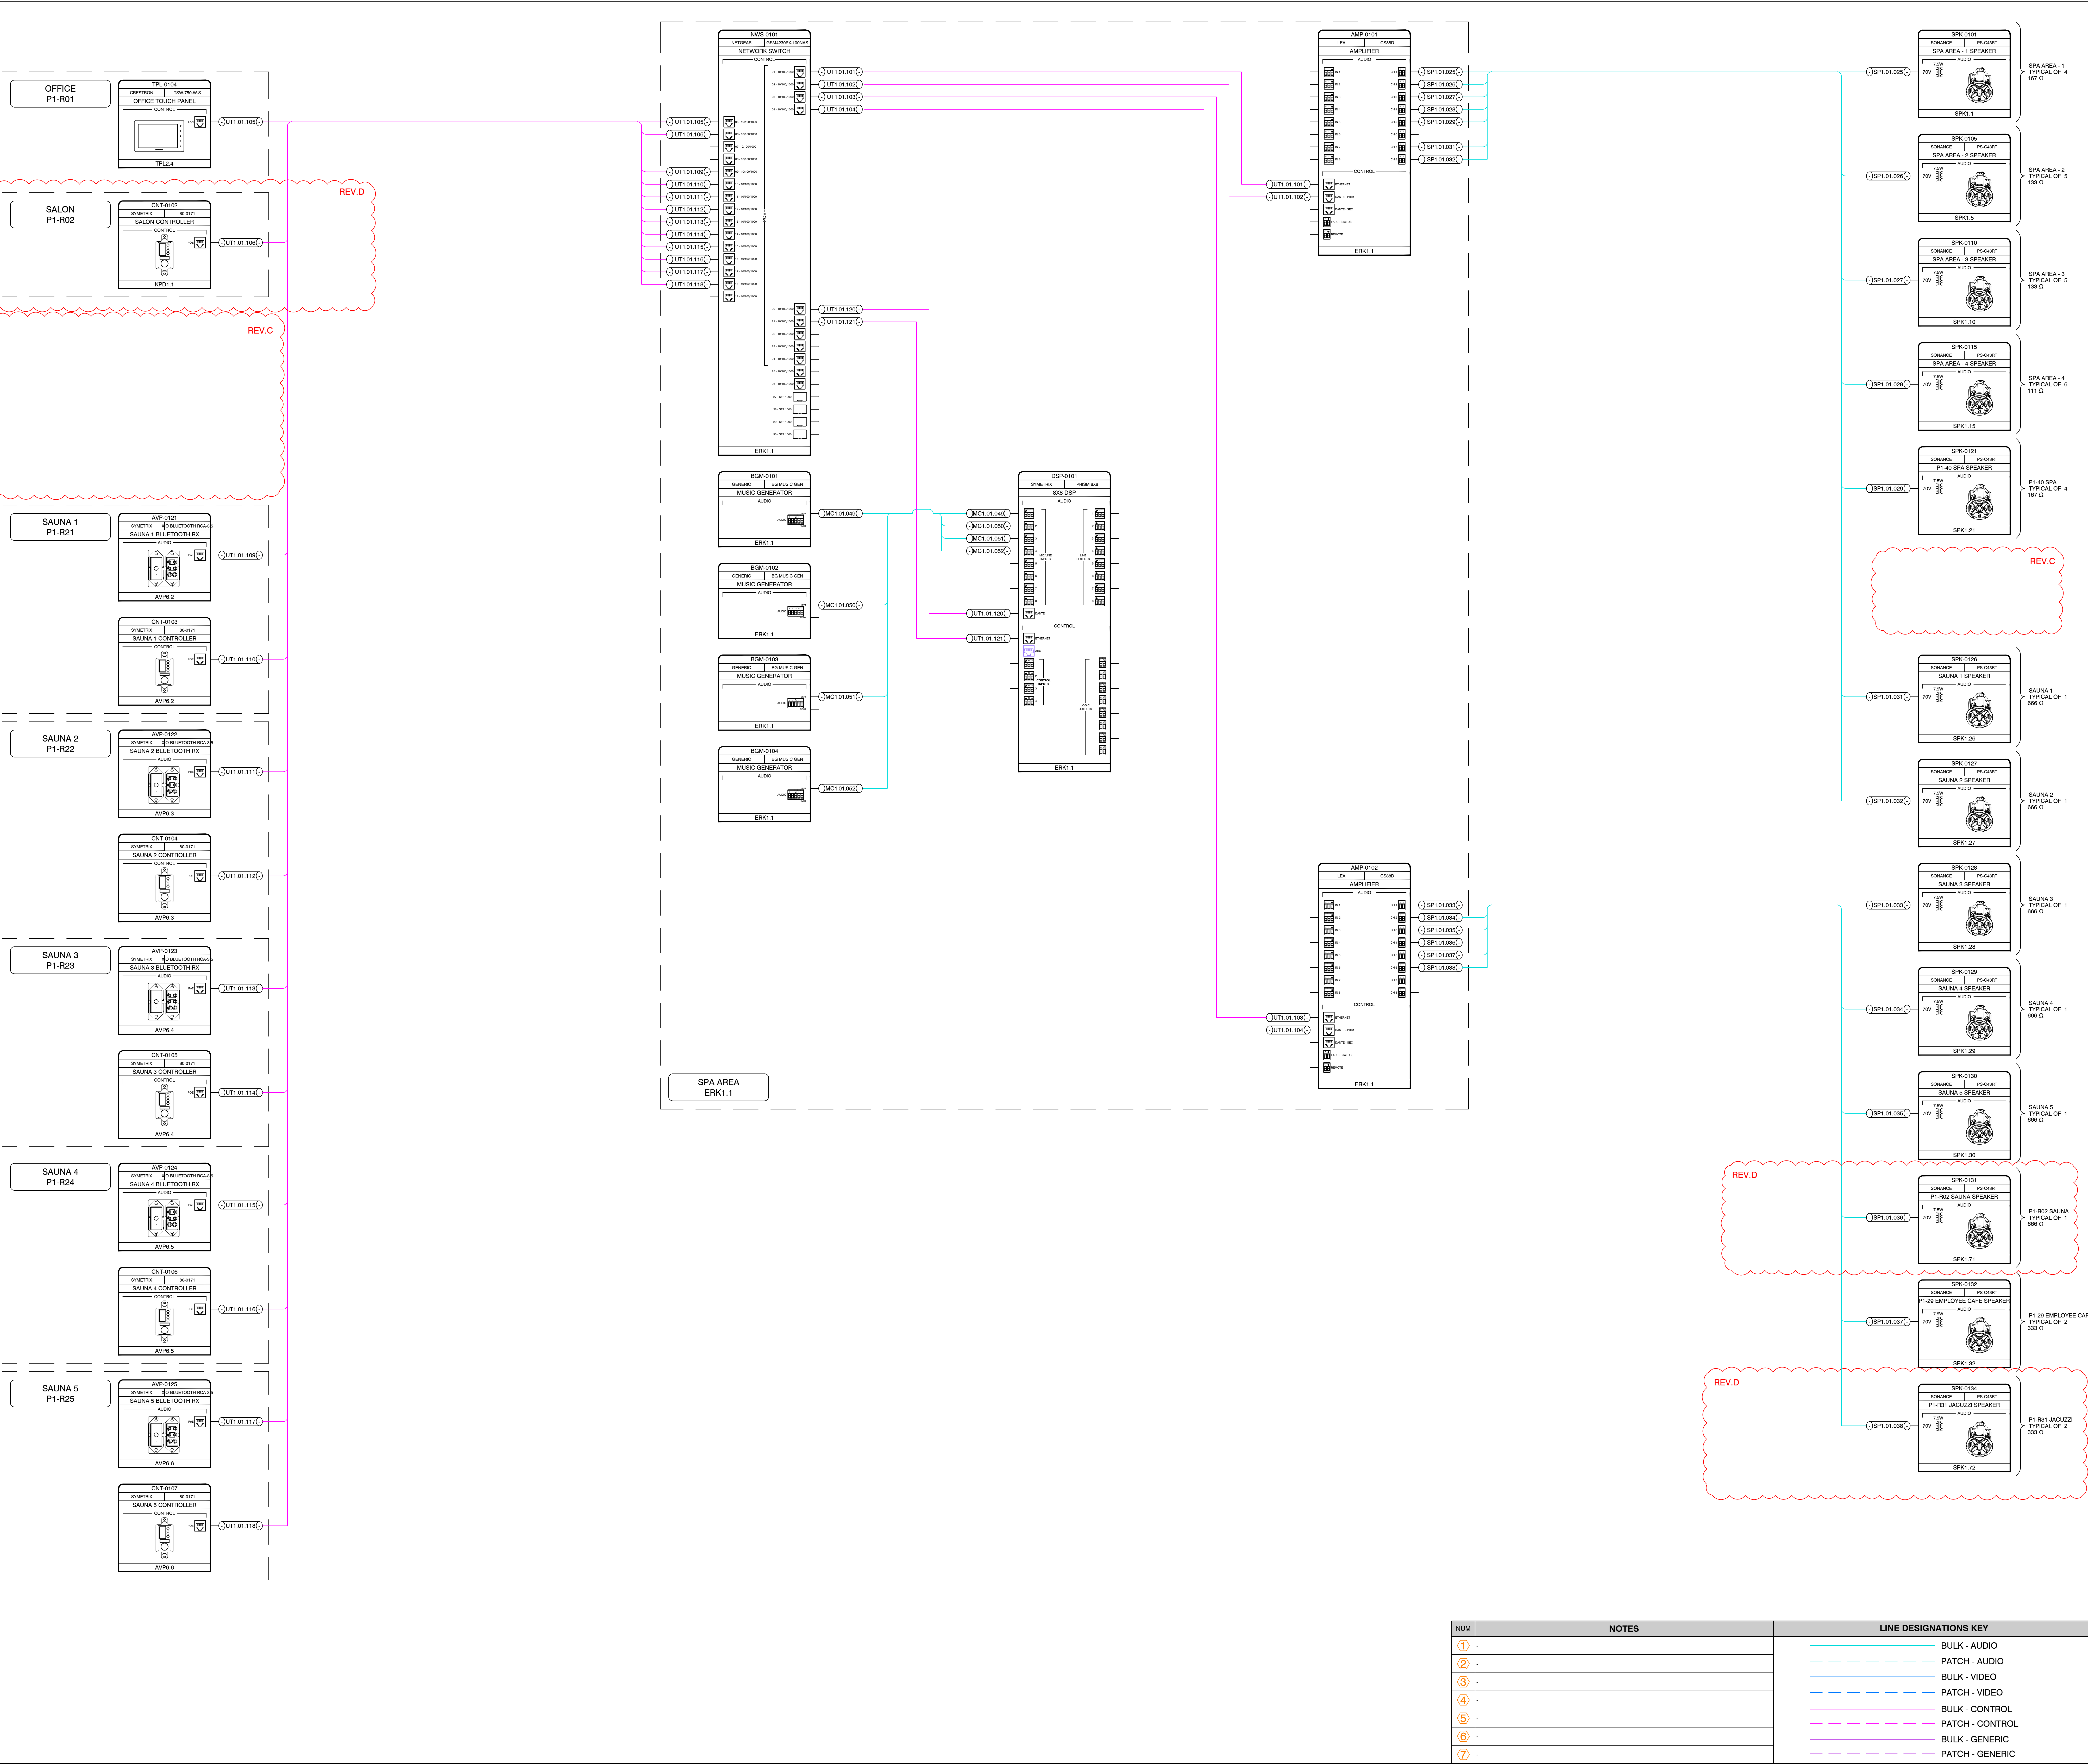

www.marshallind.com

PROJECT INFORMATION

5853

APPELLATION SUN VALLEY

AUDIO VIDEO INTEGRATION

CUSTOMER NAME:	HARRIMAN SUN VALLEY HOTEL	CUSTOMER NUMBER:	APH001
SITE NAME:	HARRIMAN SUN VALLEY HOTEL	SITE NUMBER:	72338311
SITE ADDRESS:	300 E RIVER ST KETCHUM, ID 83353		
SALES PERSON:	JEREMY WADDELL	ENGINEERED BY:	ADAM HANDY
DRAWN:	EU ANDERSON	PROJECT MANAGER:	JEREMY WADDELL

DRAWING SET INFORMATION

PHASE: CONSTRUCTION

PUBLISH DATE: 6/1/2026

PLOT SIZE: ARCH FULL BLEED E (36.00 X 48.00 INCHES)

PLOT SCALE: 1" = 1'-0"

APPROVED BY: _____

SHEET REVISION INFORMATION

REVISION	REVISION DATE	REVISION DESCRIPTION
---	---	---

REVISION & ISSUE HISTORY

ISSUED FOR:	REV.	DATE:
---	---	---

APPELLATION SUN VALLEY

SINGLE LINE DIAGRAMS


RESORT AV



LEVEL P1 RACK - SPA

NUM	NOTES	LINE DESIGNATIONS KEY
①	BULK - AUDIO	Solid Blue Line
②	PATCH - AUDIO	Dashed Blue Line
③	BULK - VIDEO	Solid Green Line
④	PATCH - VIDEO	Dashed Green Line
⑤	BULK - CONTROL	Solid Purple Line
⑥	PATCH - CONTROL	Dashed Purple Line
⑦	BULK - GENERIC	Solid Black Line
⑧	PATCH - GENERIC	Dashed Black Line

AV801.1

FILE NAME: AV800.DWG

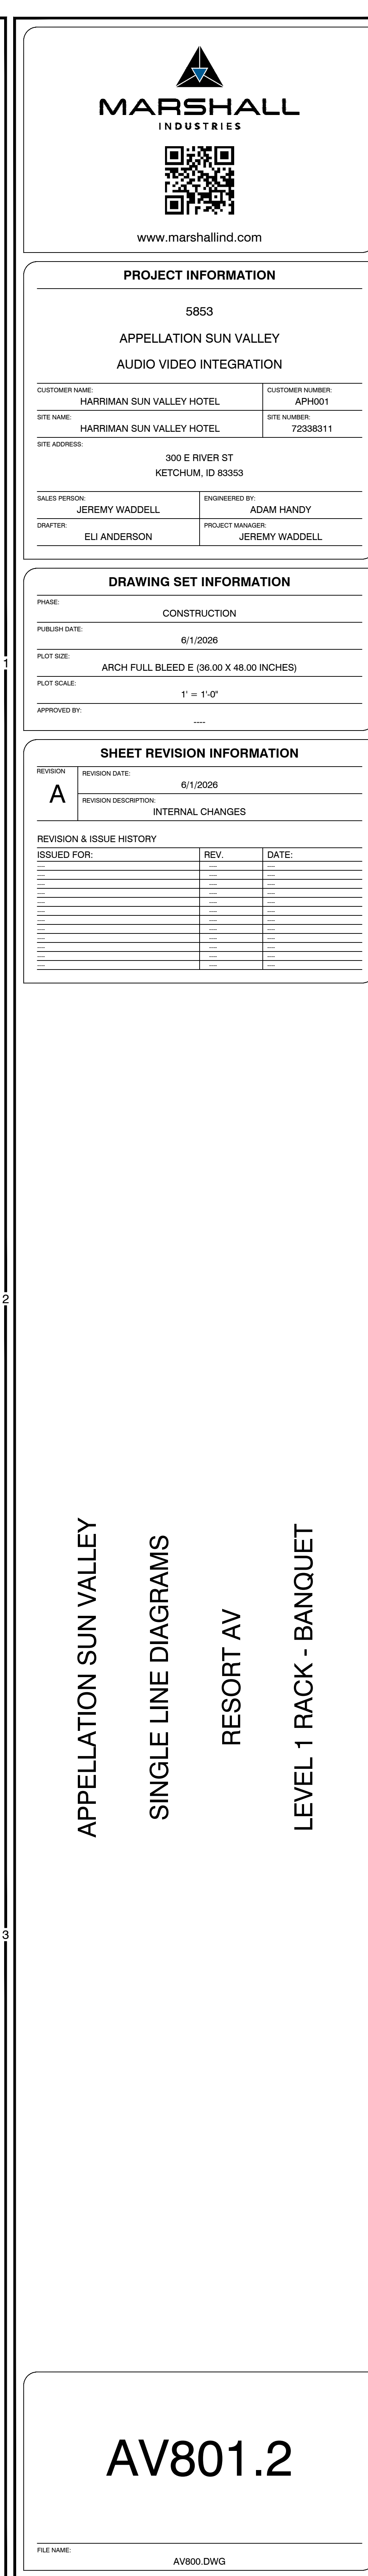

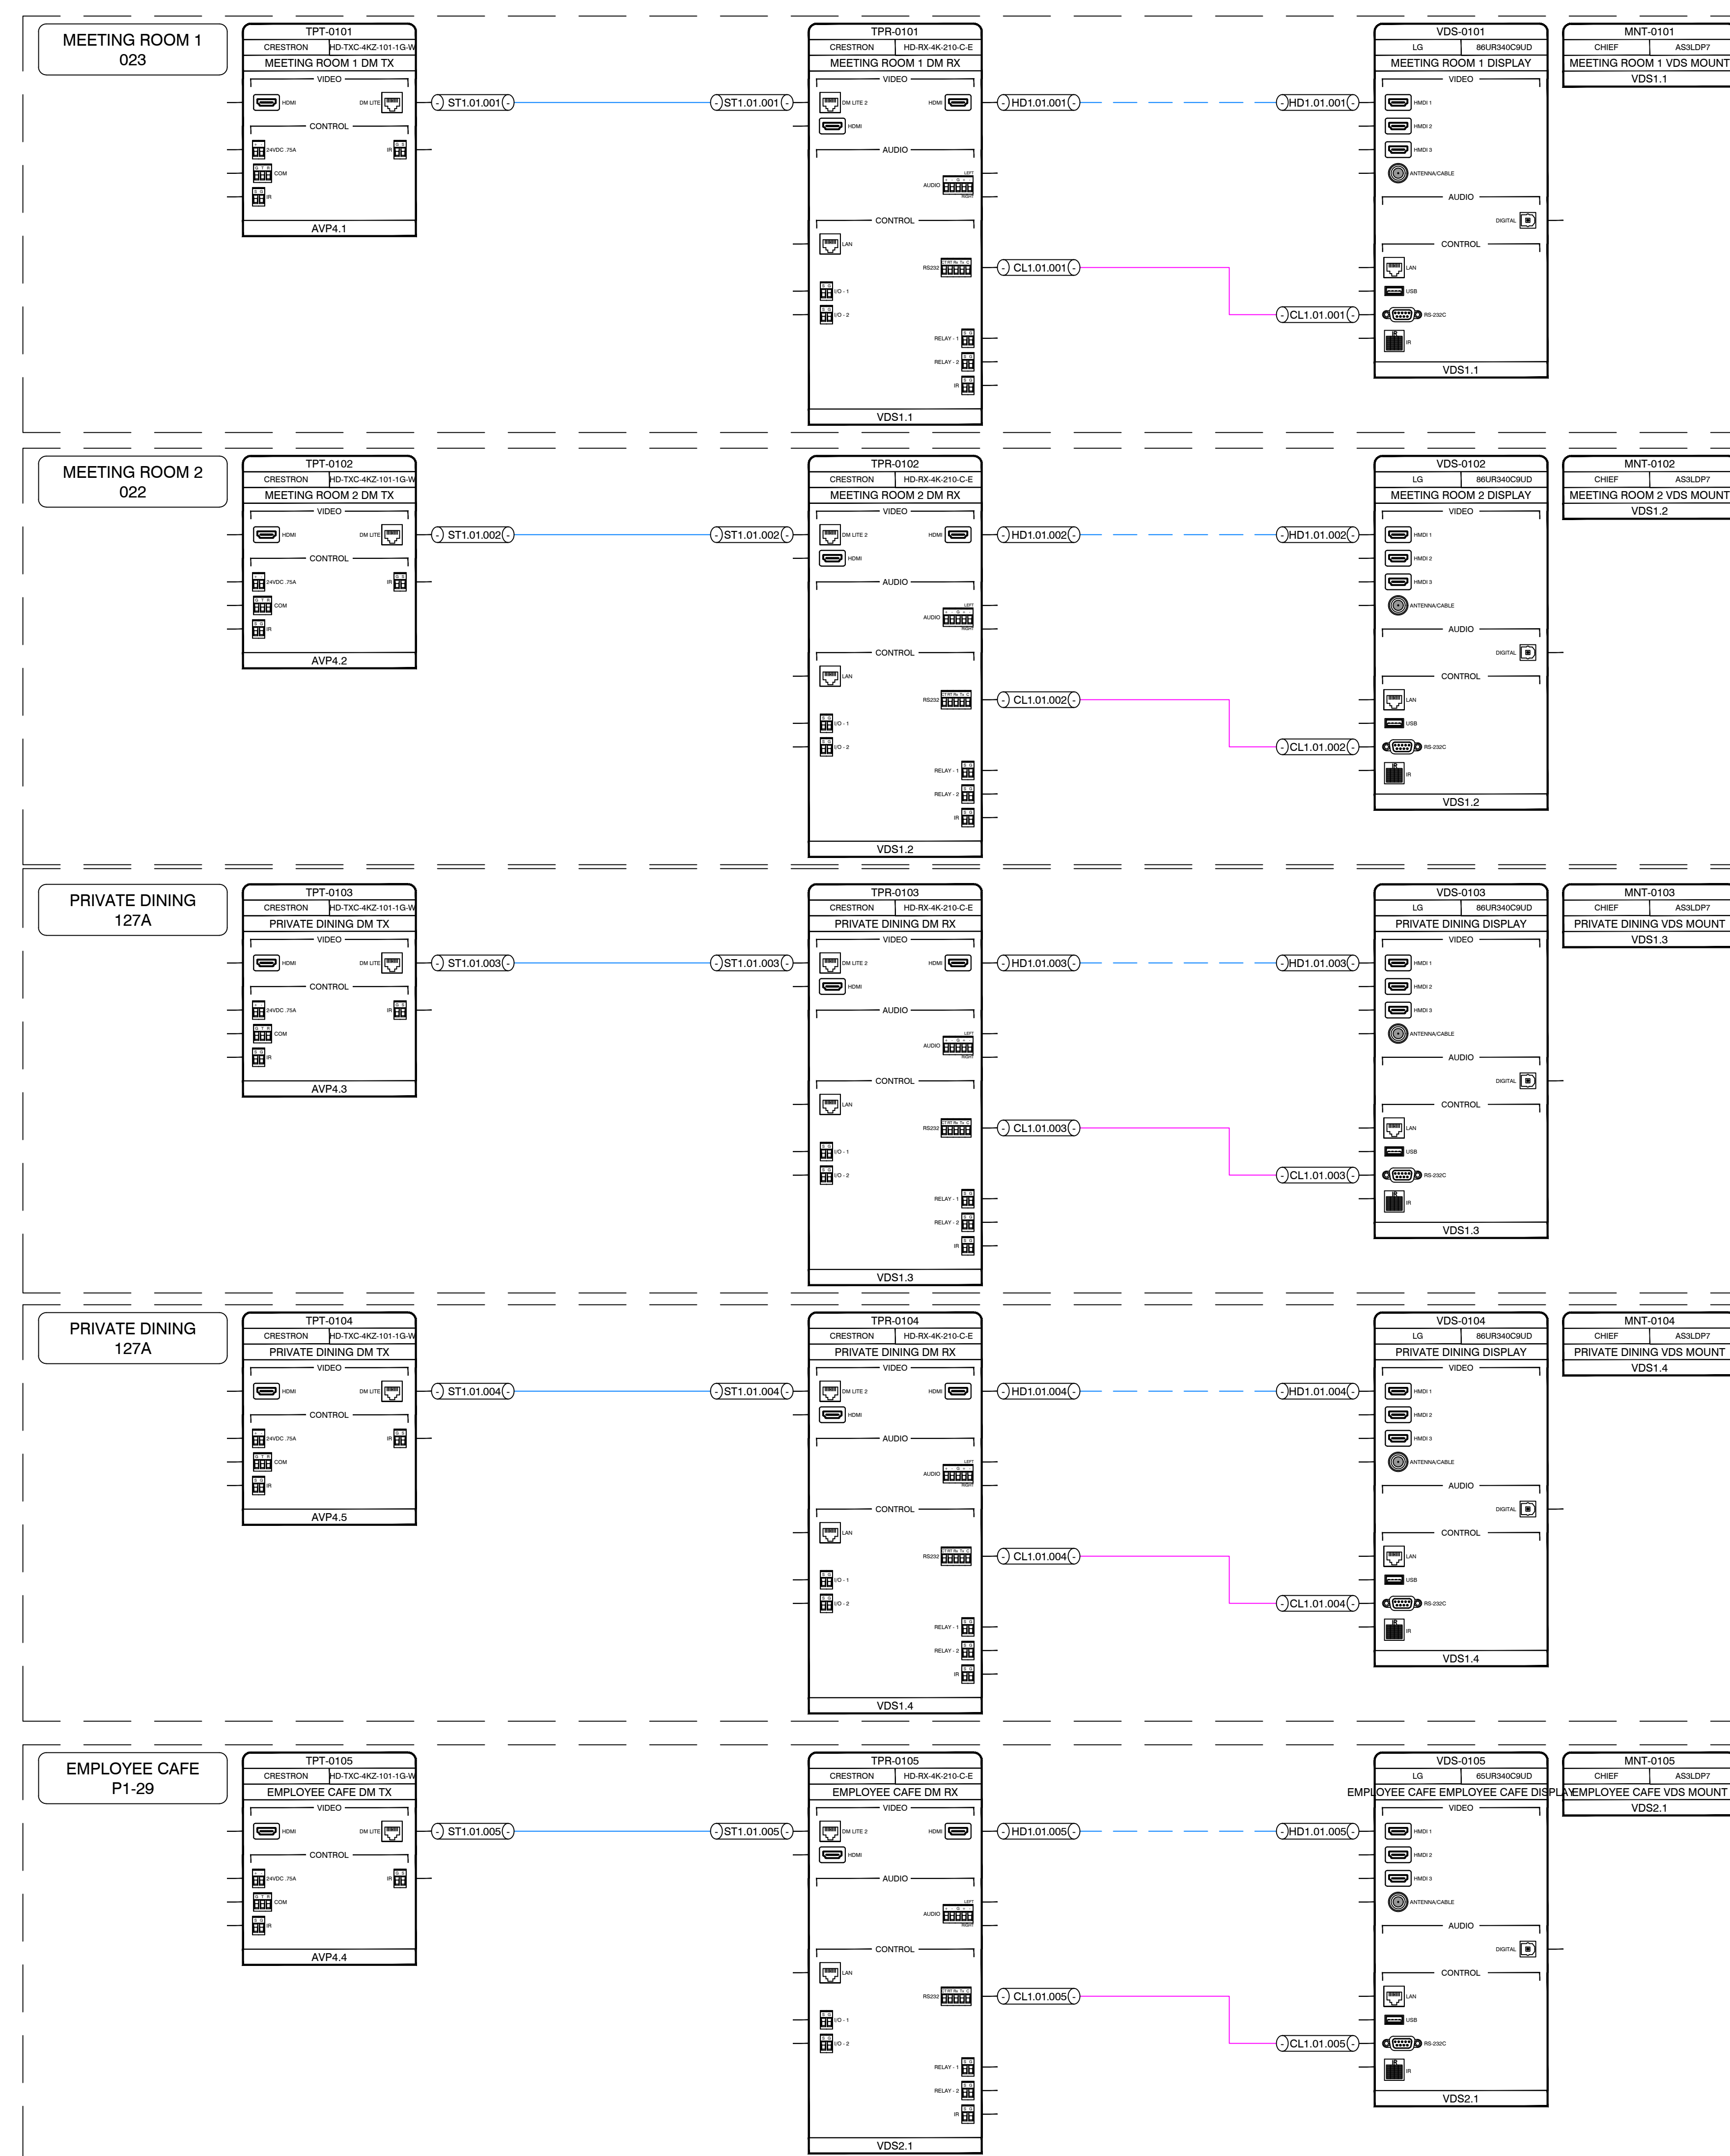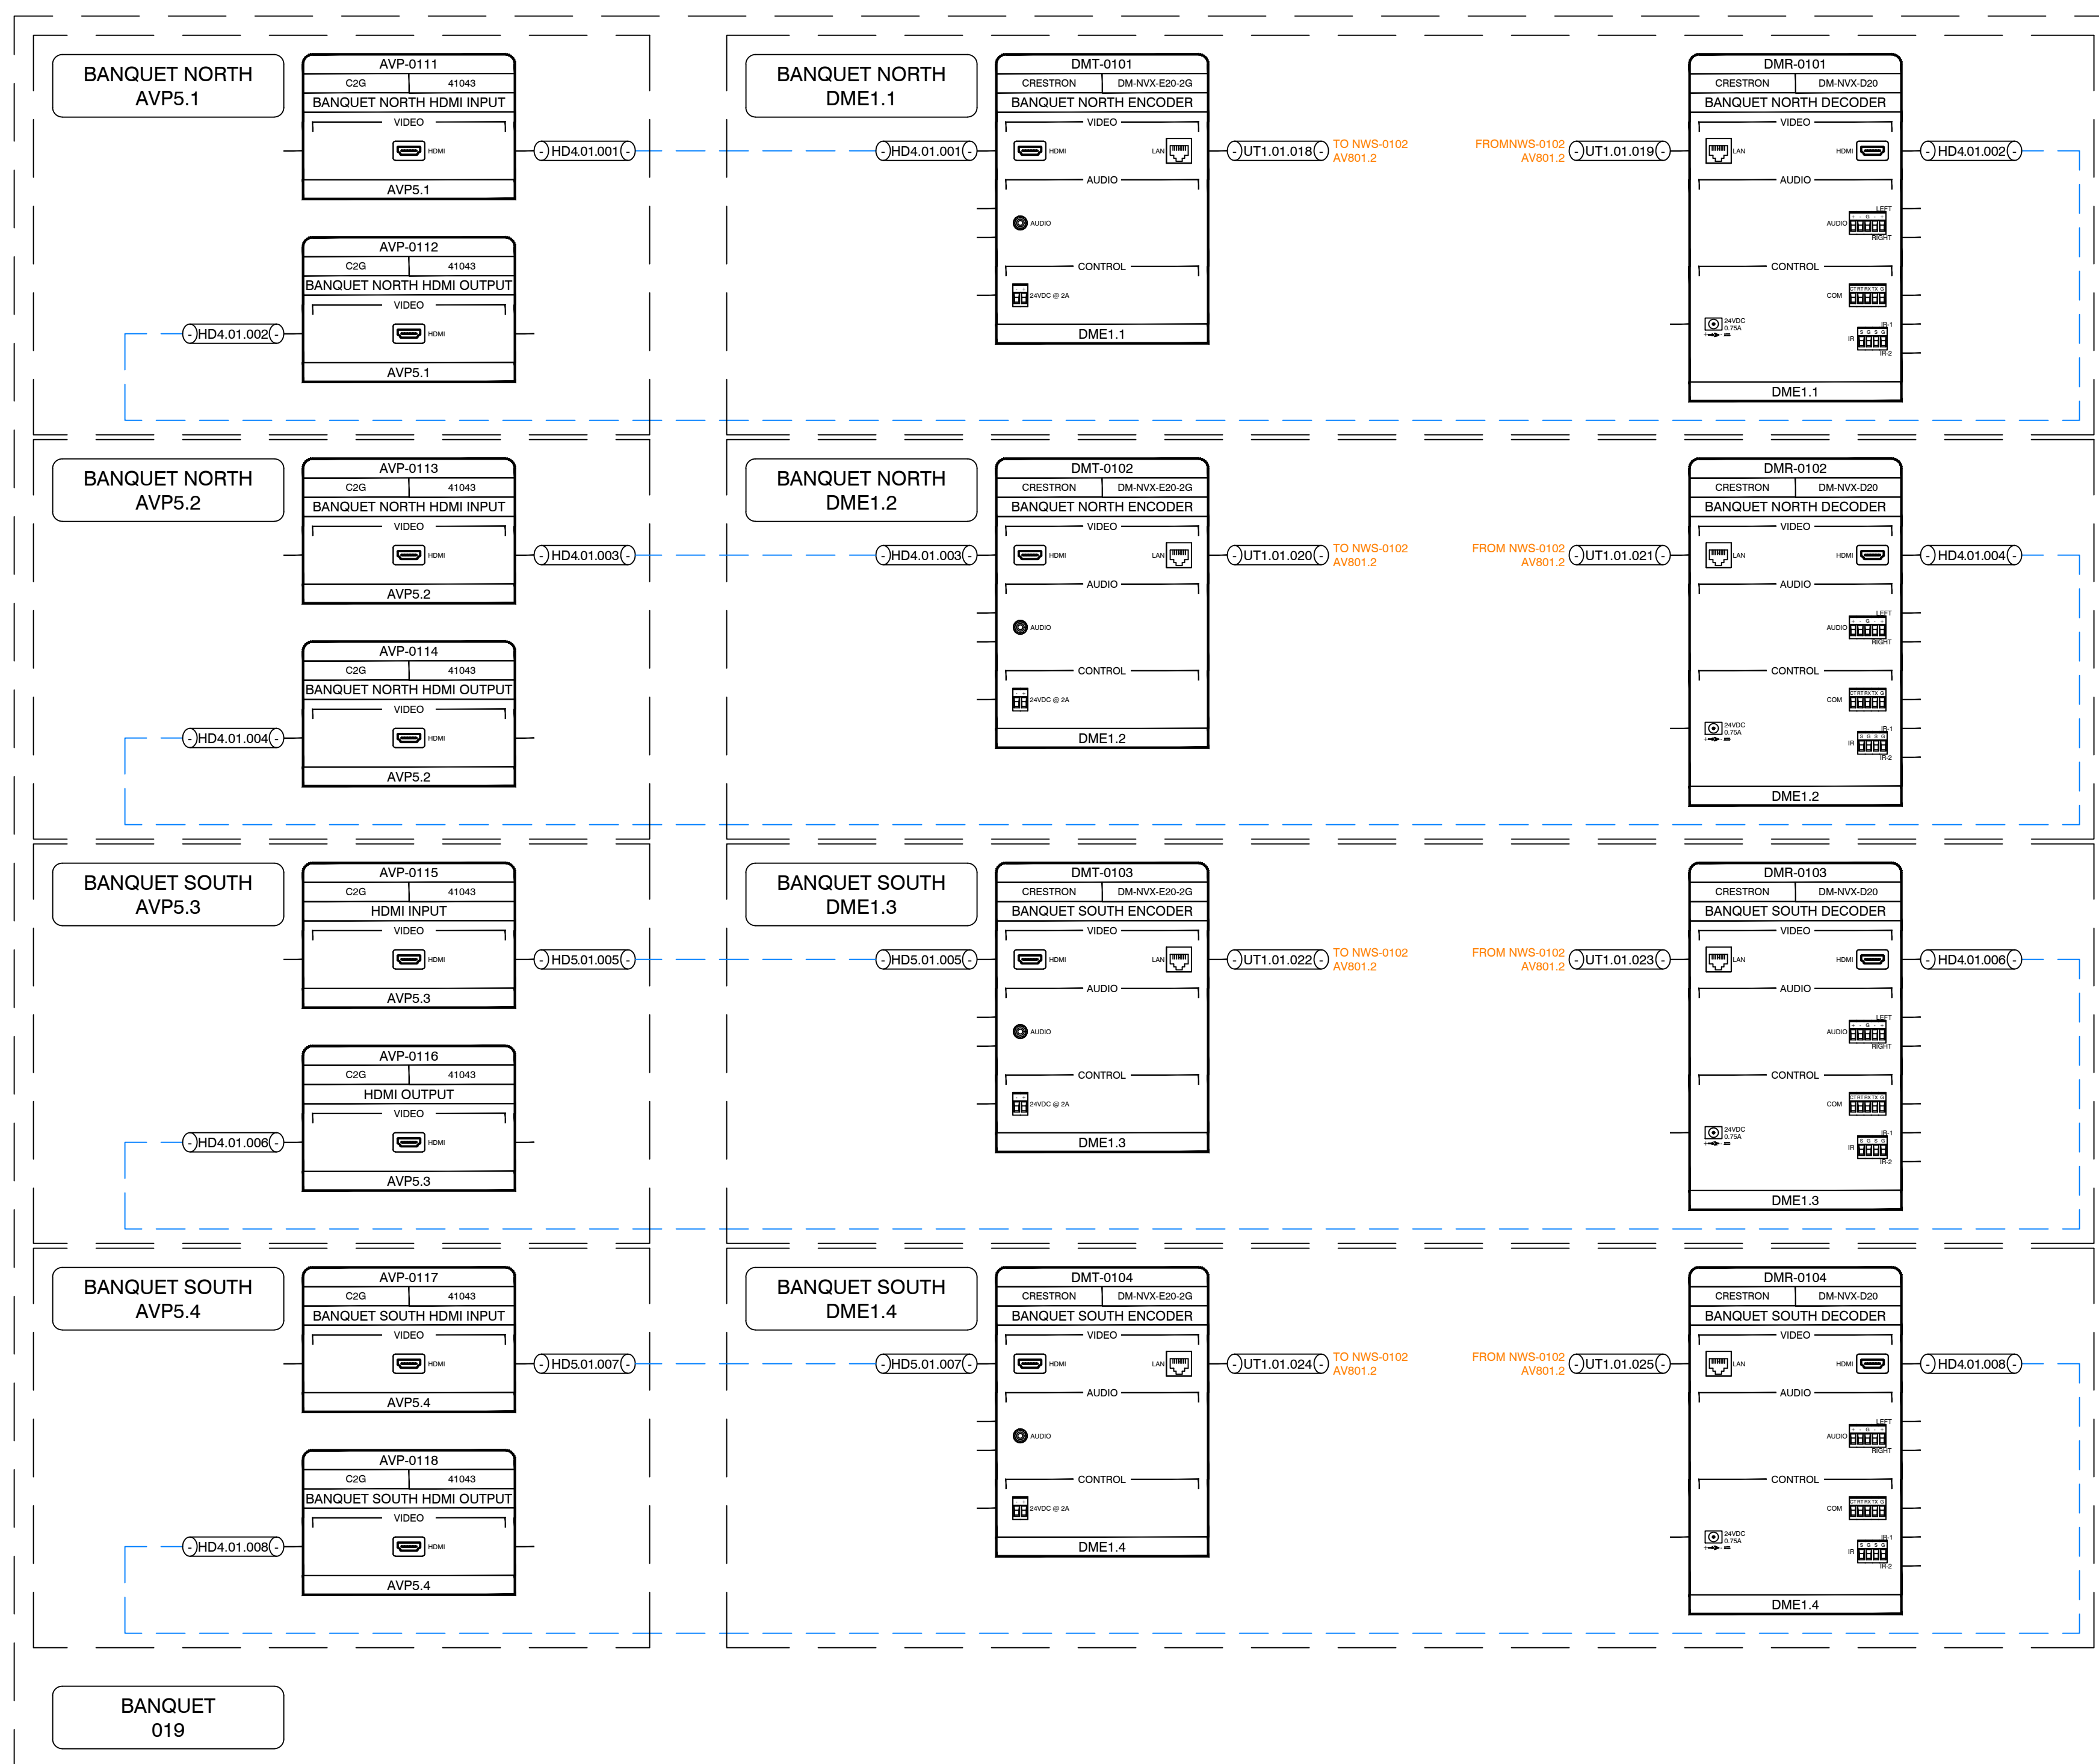[illegible]

NUM		NOTES	LINE DESIGNATIONS KEY	
①	-			BULK - AUDIO
②	-			PATCH - AUDIO
③	-			BULK - VIDEO
④	-			PATCH - VIDEO
⑤	-			BULK - CONTROL
⑥	-			PATCH - CONTROL
⑥	-			BULK - GENERIC
⑦	-			PATCH - GENERIC

